

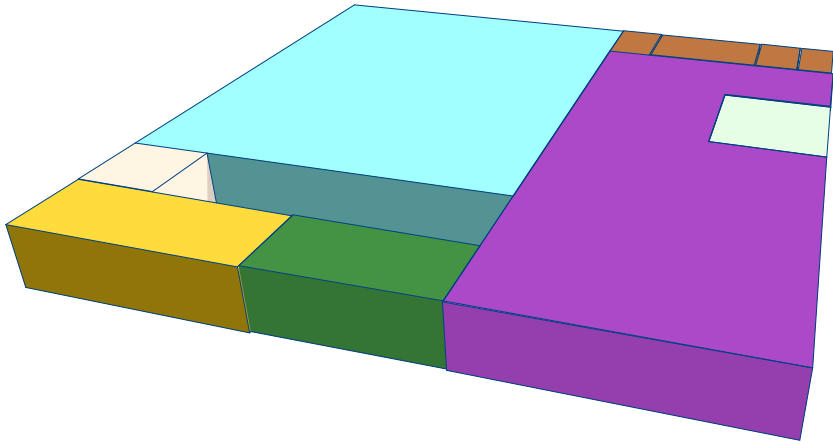
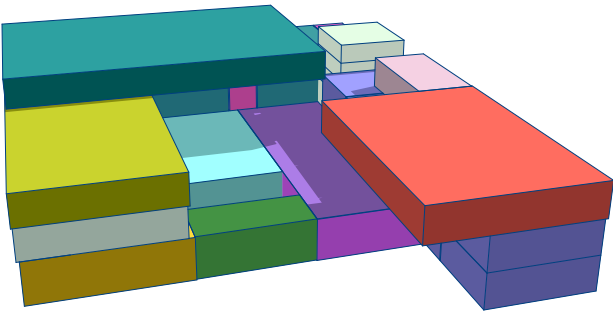


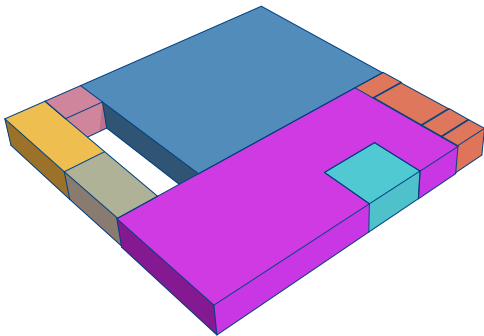

- |   |   |
|---|---|
|  PISCINA                 |  REFEITÓRIO / VIVENCIA |
|  DEPÓSITO PISCINA        |  SERVIÇOS E COZINHA    |
|  VESTIÁRIOS E SANITÁRIOS |  CIRCULAÇÃO VERTICAL   |
|  ENTRADA PRINCIPAL       |  SERVIÇOS E COZINHA    |

|                                                |         |            |
|------------------------------------------------|---------|------------|
| PROJETO                                        |         |            |
| <b>PROJETO PARA EDIFÍCIOS MULTI FUNCIONAIS</b> |         |            |
| NOME DO ALUNO                                  | RA      |            |
| MONICA CLEIA SOUSA CARVALHO                    | G73EAE6 |            |
| FASE PROJETO                                   |         |            |
| NP1                                            | ESCALA  | DATA       |
| CONTEÚDO                                       | 1:500   | 26/03/2025 |
| <b>IMPLANTAÇÃO</b>                             |         | FOLHA      |
| ARQUIVO DIGITAL                                |         | <b>01</b>  |
| terreno modelado2.pln                          |         |            |

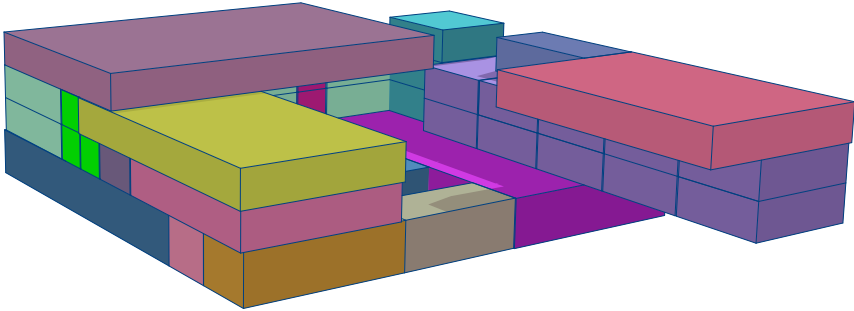

- |   |   |
|---|---|
|  PISCINA                 |  REFEITÓRIO / VIVENCIA |
|  DEPÓSITO PISCINA        |  SERVIÇOS E COZINHA    |
|  VESTIÁRIOS E SANITÁRIOS |  CIRCULAÇÃO VERTICAL   |
|  ENTRADA PRINCIPAL       |  SERVIÇOS E COZINHA    |

|                                                |         |            |
|------------------------------------------------|---------|------------|
| PROJETO                                        |         |            |
| <b>PROJETO PARA EDIFÍCIOS MULTI FUNCIONAIS</b> |         |            |
| NOME DO ALUNO                                  | RA      |            |
| MONICA CLEIA SOUSA CARVALHO                    | G73EAE6 |            |
| FASE PROJETO                                   |         |            |
| NP1                                            | ESCALA  | DATA       |
| CONTEÚDO                                       | 1:500   | 26/03/2025 |
| <b>IMPLANTAÇÃO</b>                             |         | FOLHA      |
| ARQUIVO DIGITAL                                |         | <b>01</b>  |
| terreno modelado2.pln                          |         |            |

1. Identificação do Terreno:


- Área Total do Terreno: 2.856,00 m²


2. Índices Urbanísticos Fornecidos:

- Taxa de Ocupação (TO): 0.43 (1.235,35 m²)
- Coeficiente de Aproveitamento (CA): 4.3 (12.353,50m²)
- Taxa de Permeabilidade (TP): 27 % (796,65 m²)

3. Segurança e Acessibilidade:

- Escadas de Emergência: Foram previstas 2 (duas) escadas de emergência com largura de 2,00 metros cada.
- Banheiros Accessíveis em todos os andares: Essa medida está em conformidade com a ABNT NBR 9050 (Acessibilidade a edificações, mobiliário, espaços e equipamentos urbanos) e com a legislação de acessibilidade vigente

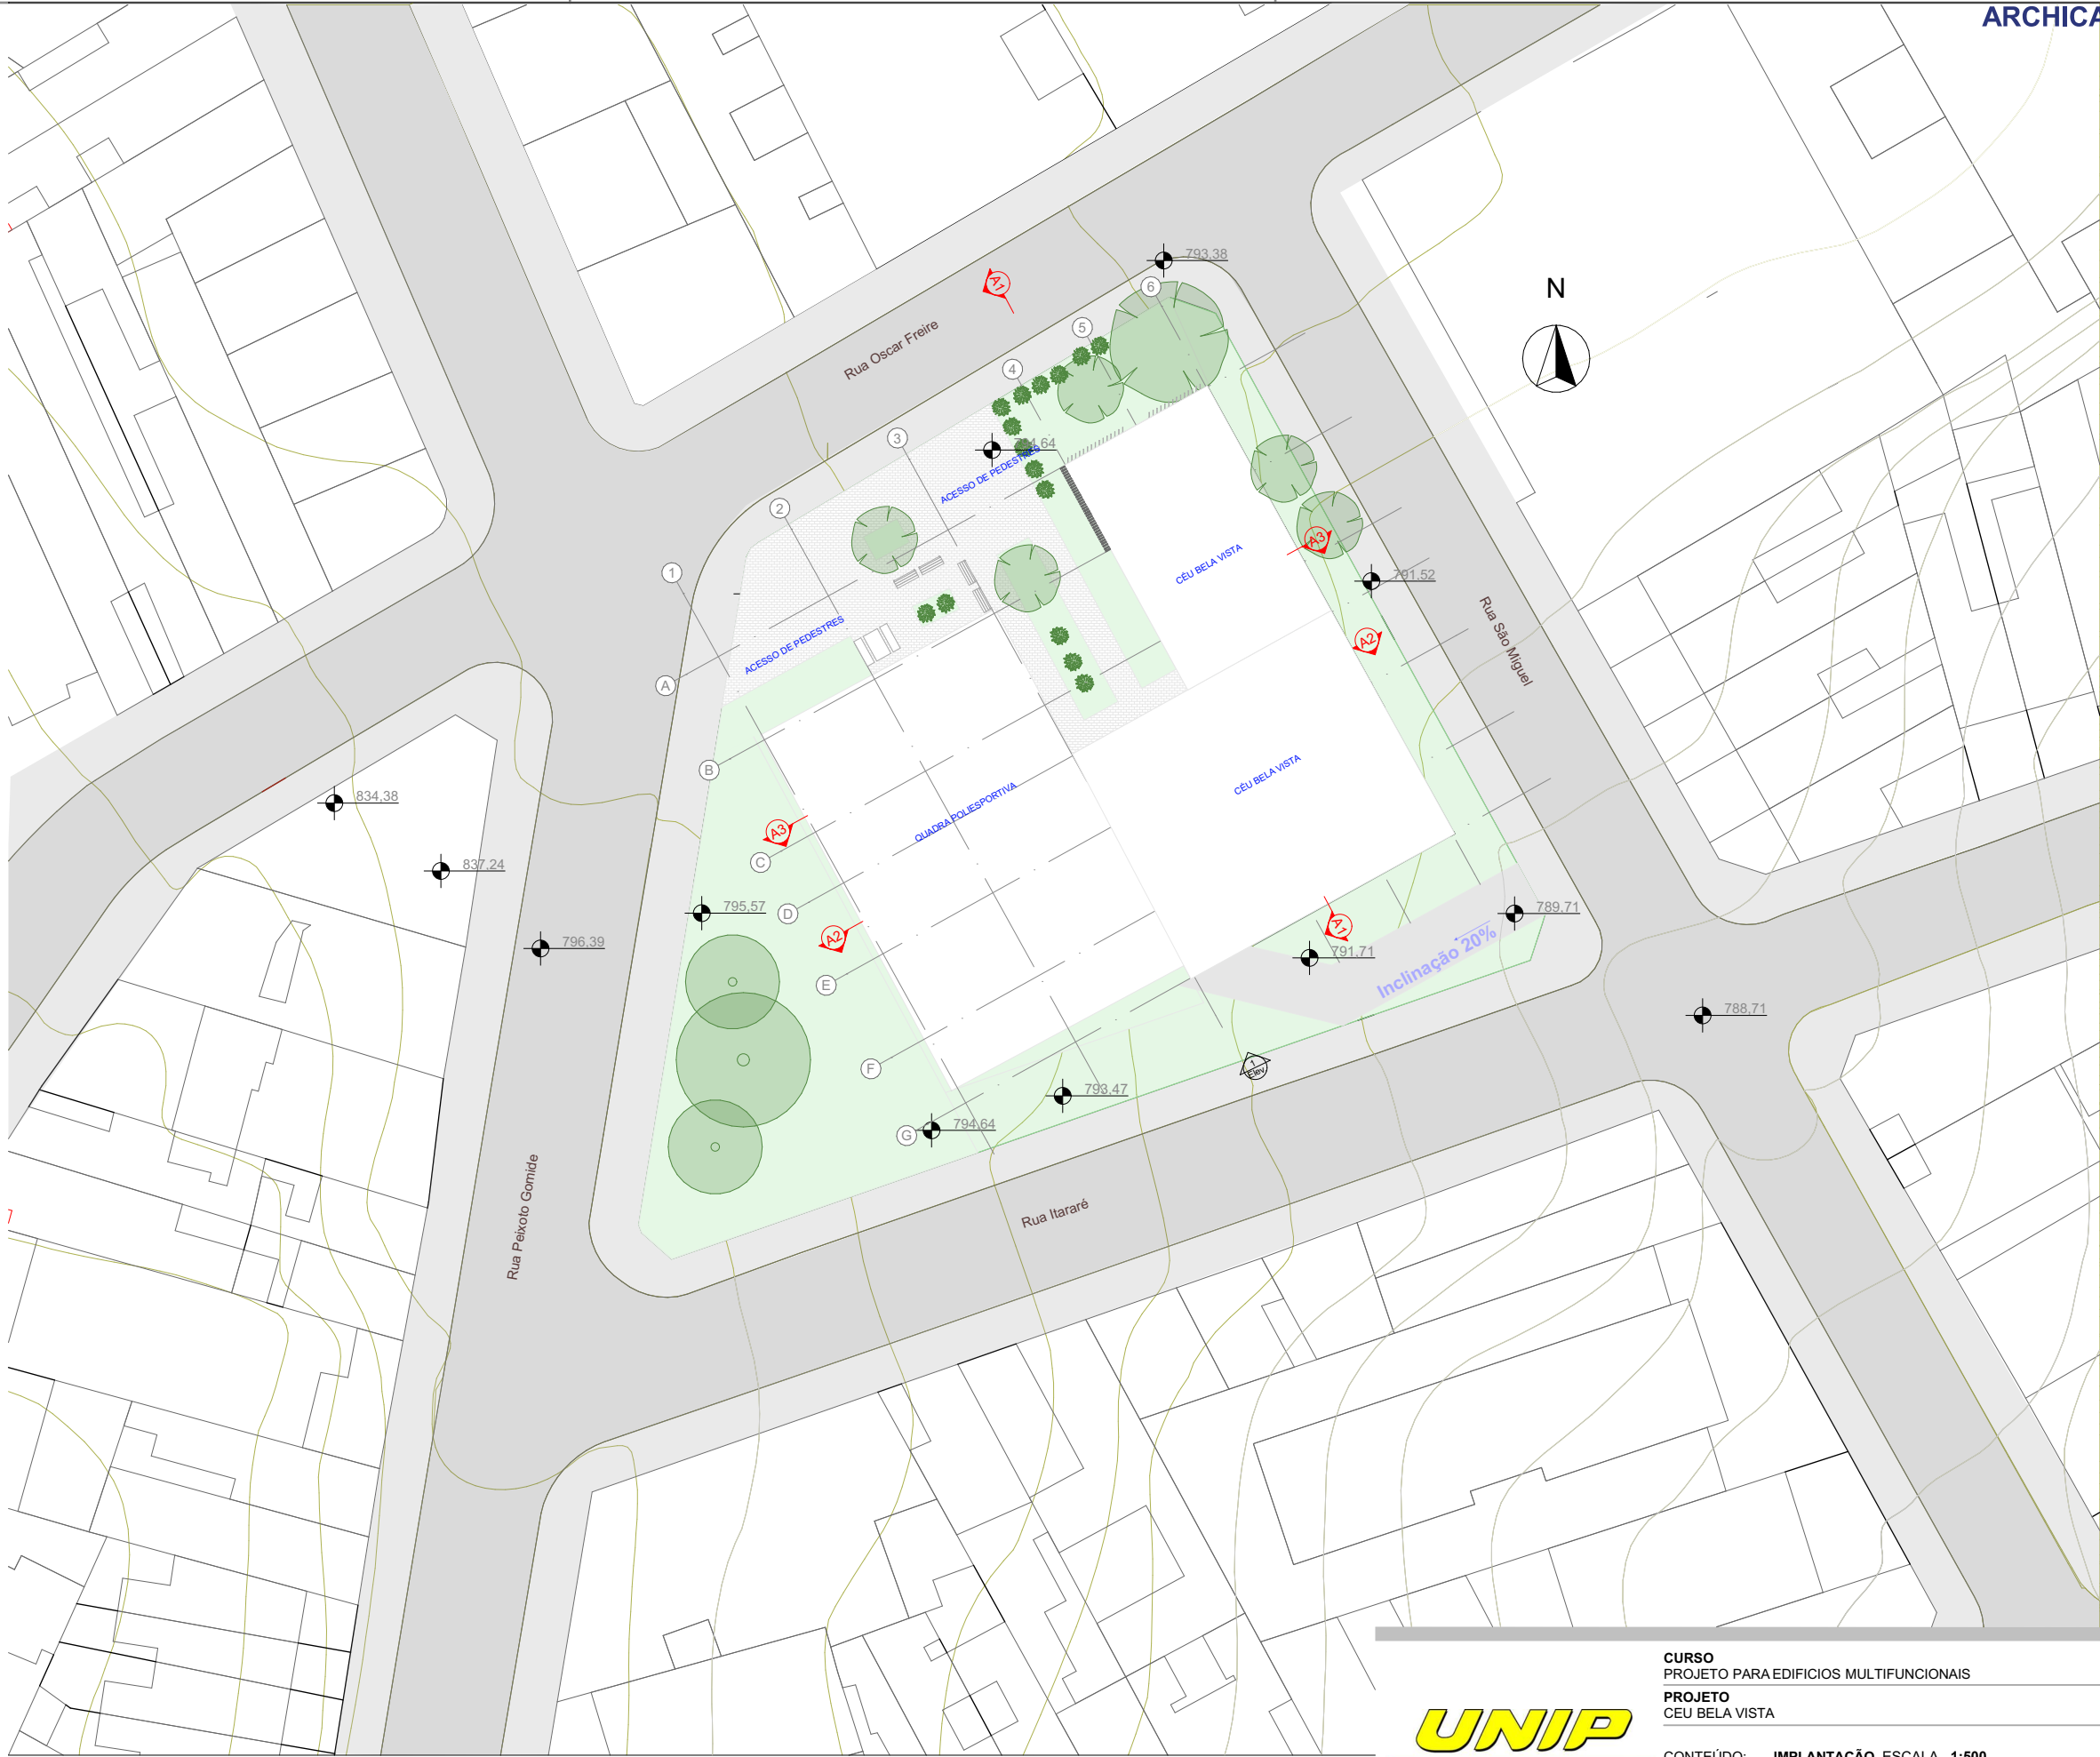

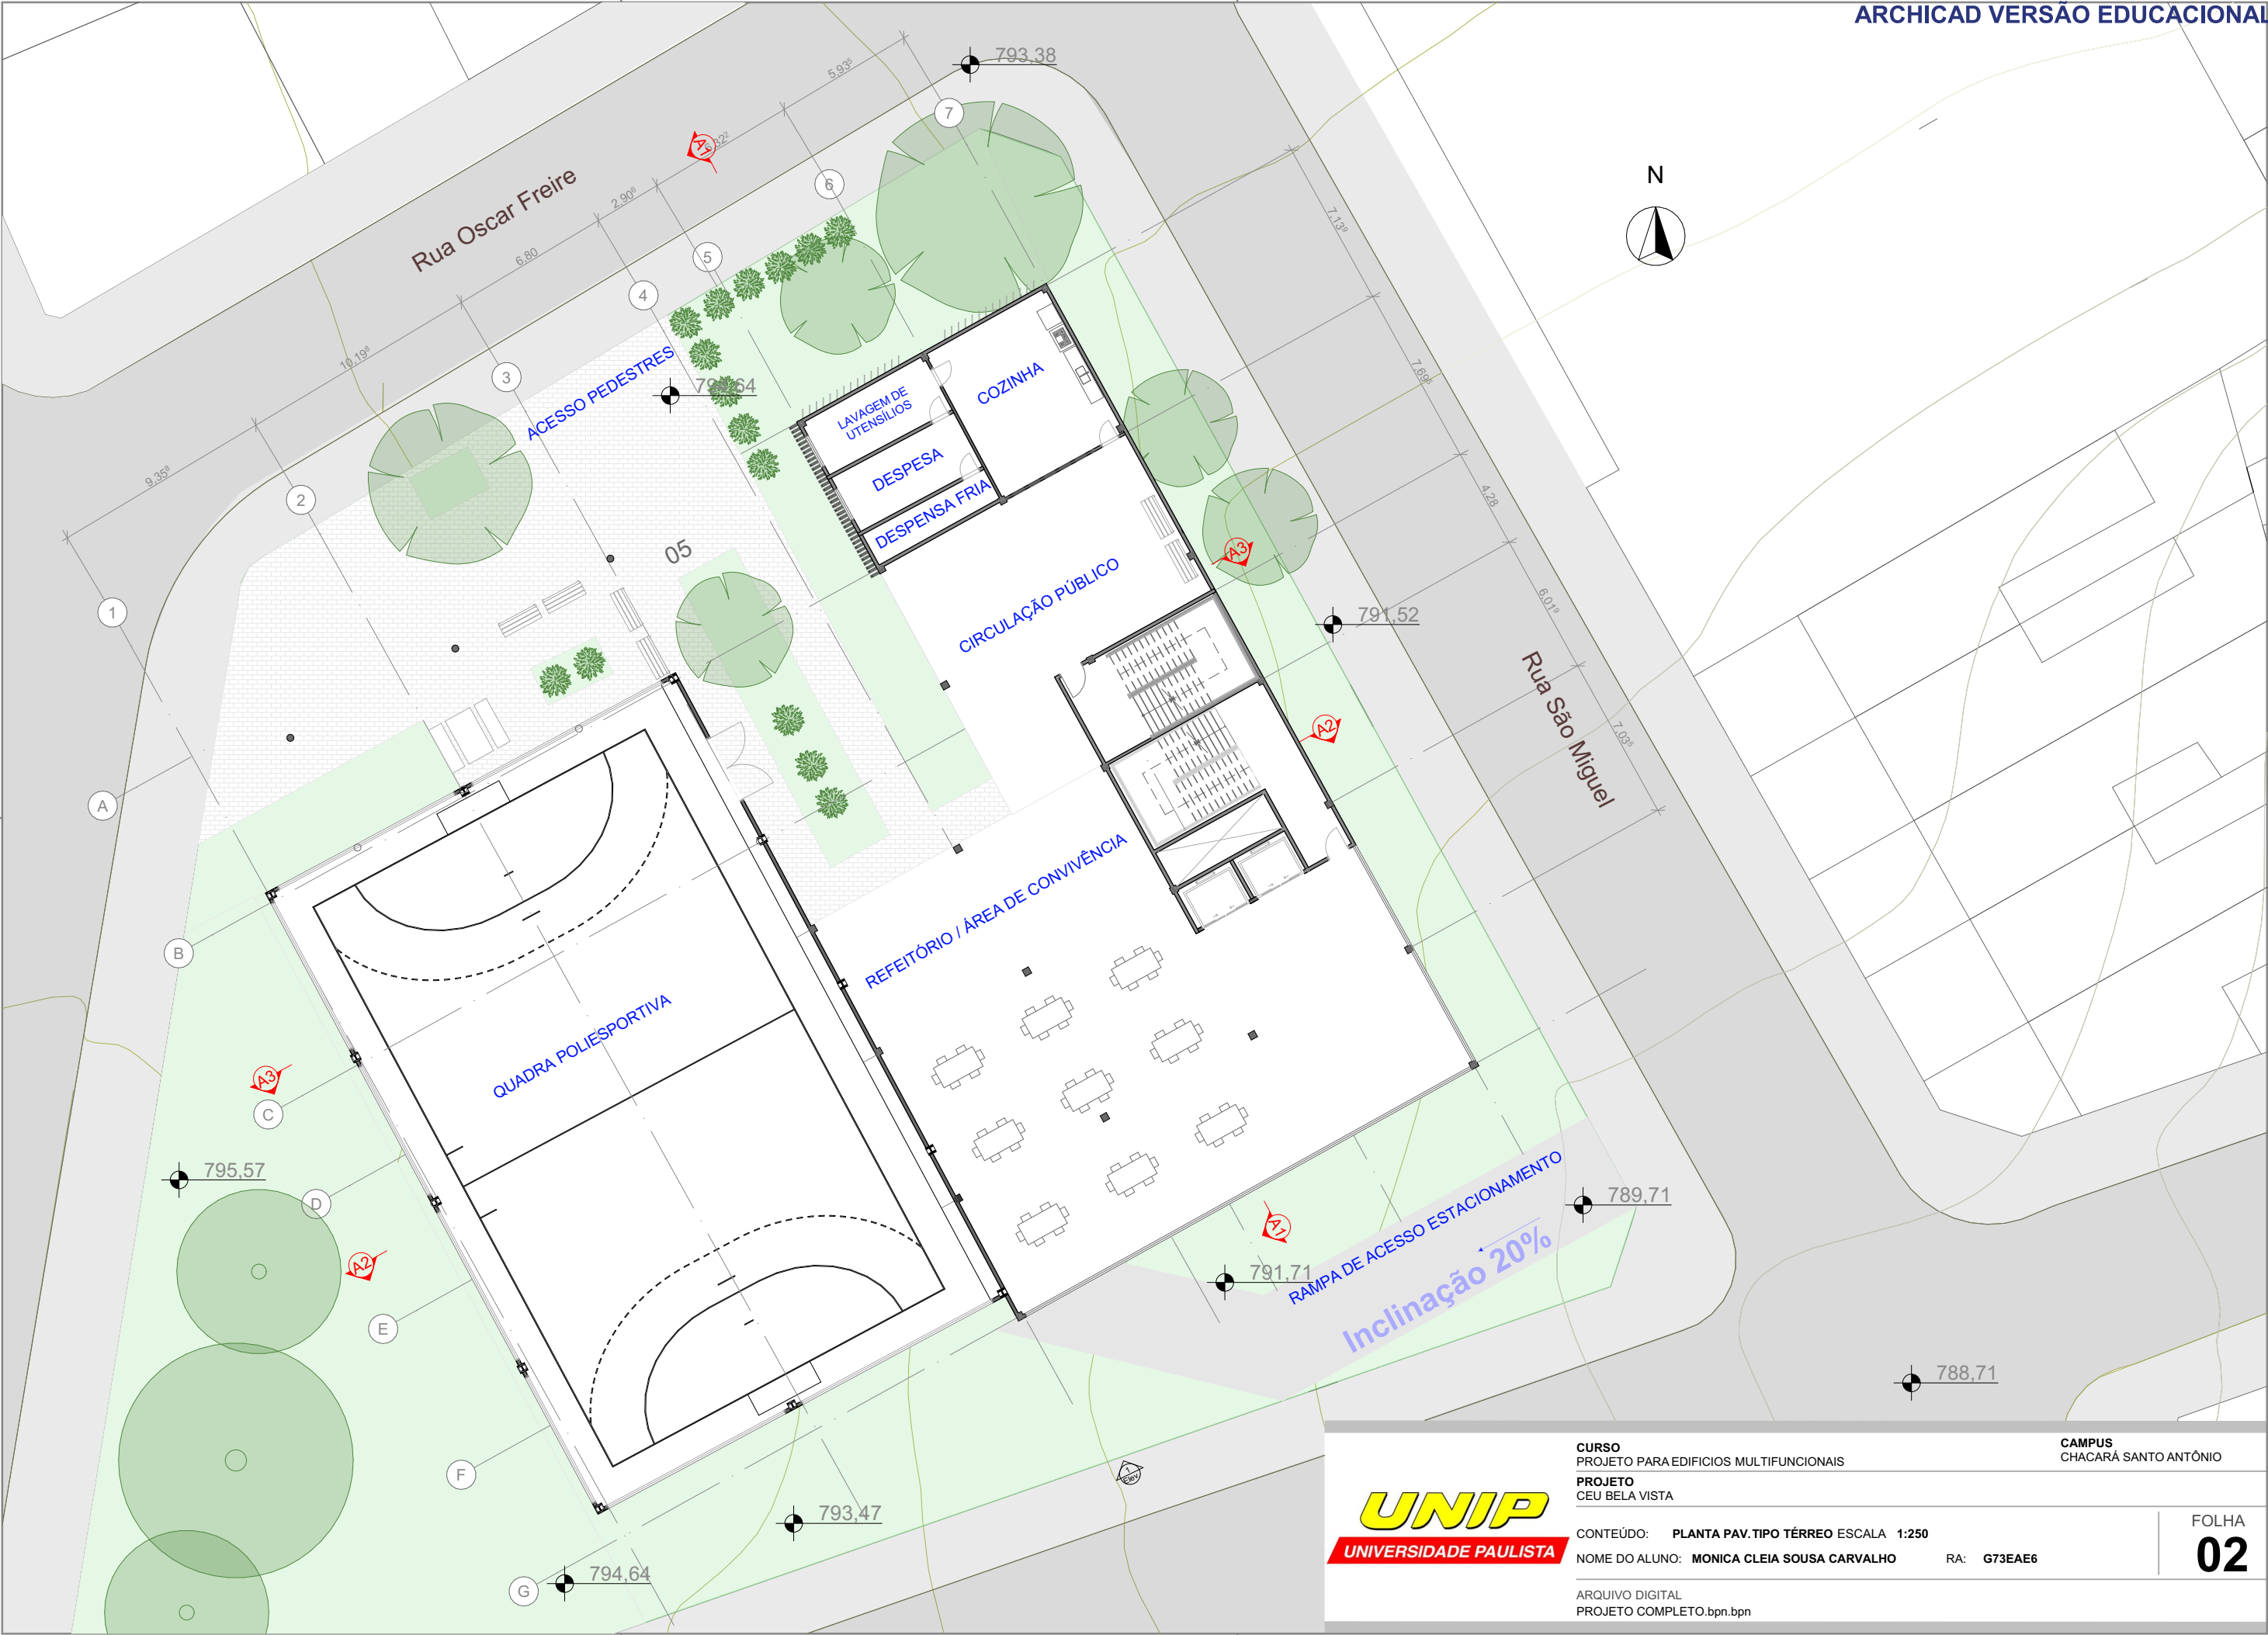

CURSO  
PROJETO PARA EDIFÍCIOS MULTIFUNCIONAIS  
PROJETO  
CEU BELA VISTA


CAMPUS  
CHACARA SANTO ANTÔNIO


CONTEÚDO: PLANTA PAV. TIPO TÉRREO ESCALA 1:250


NOME DO ALUNO: MONICA CLEIA SOUSA CARVALHO

RA: G73EAE6

ARQUIVO DIGITAL  
PROJETO COMPLETO.bpn.bpn

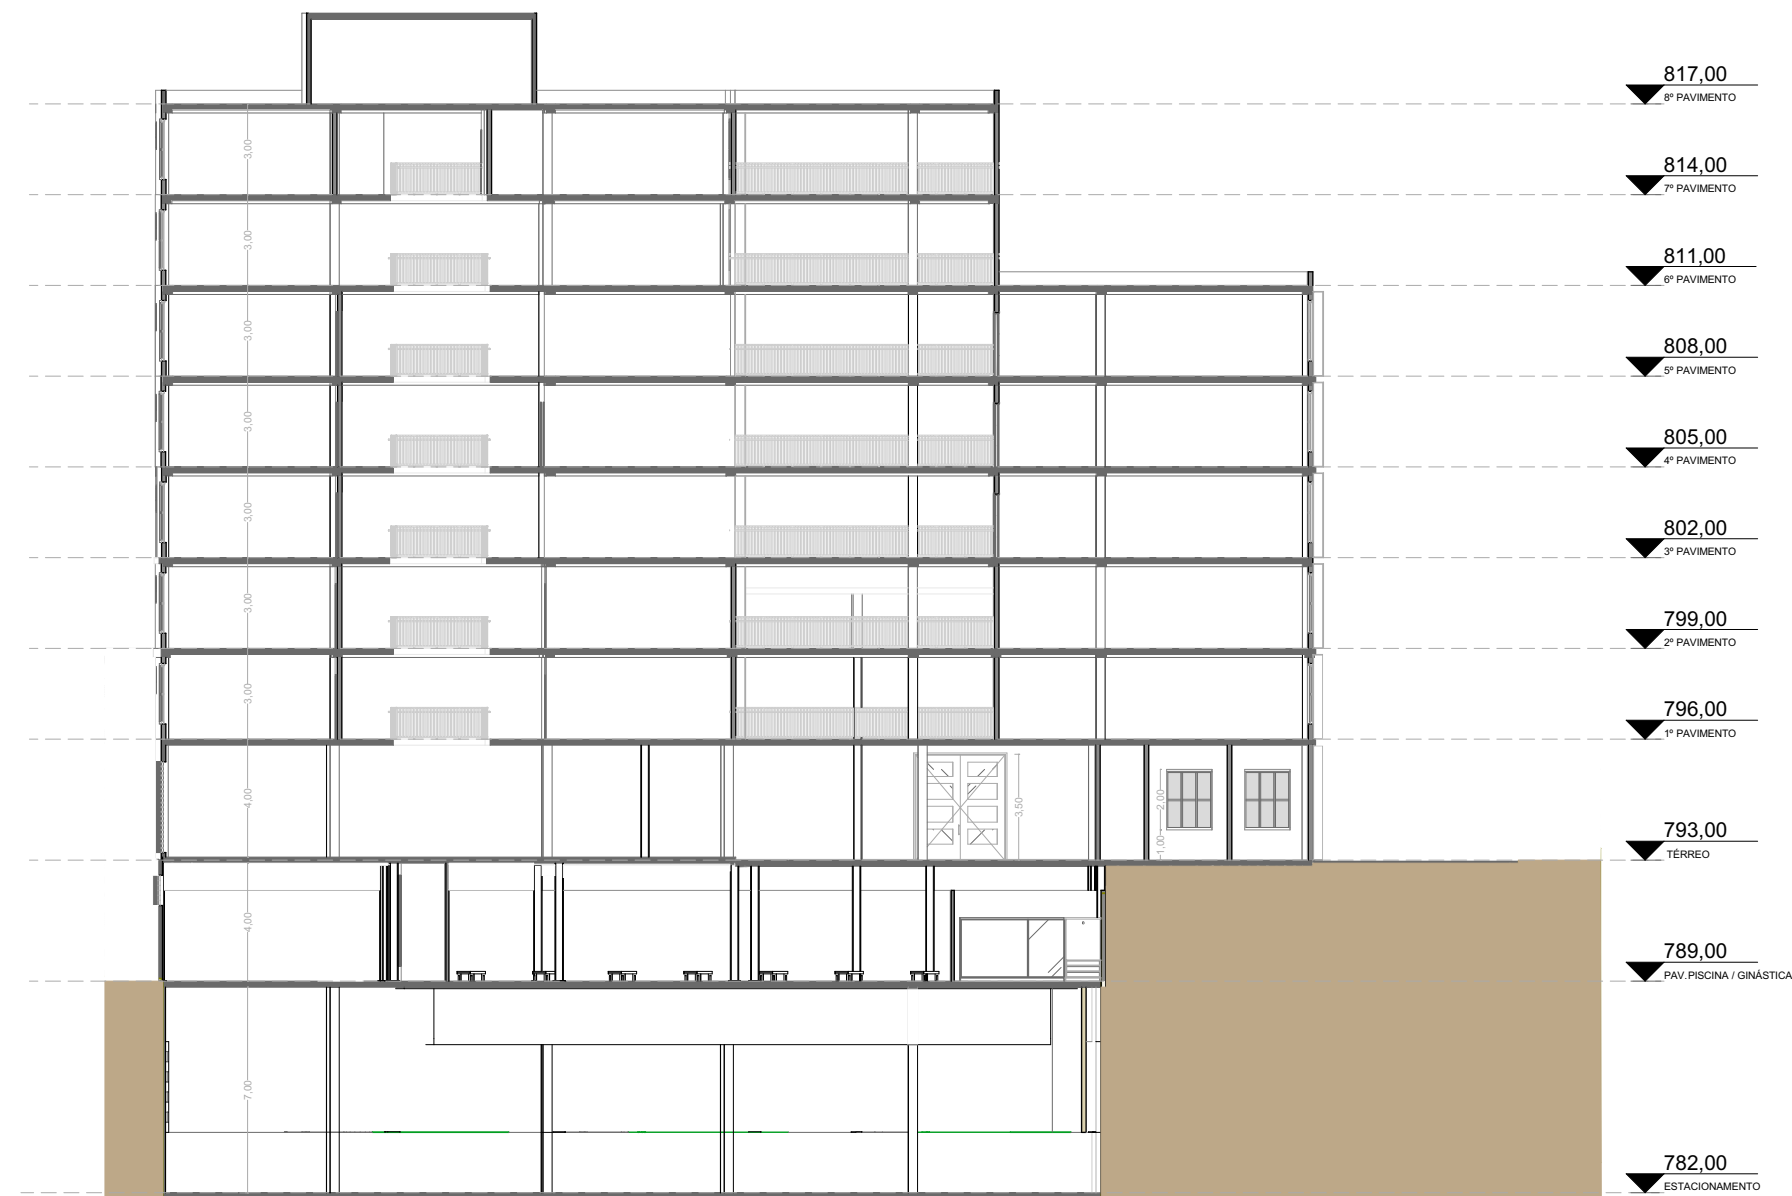

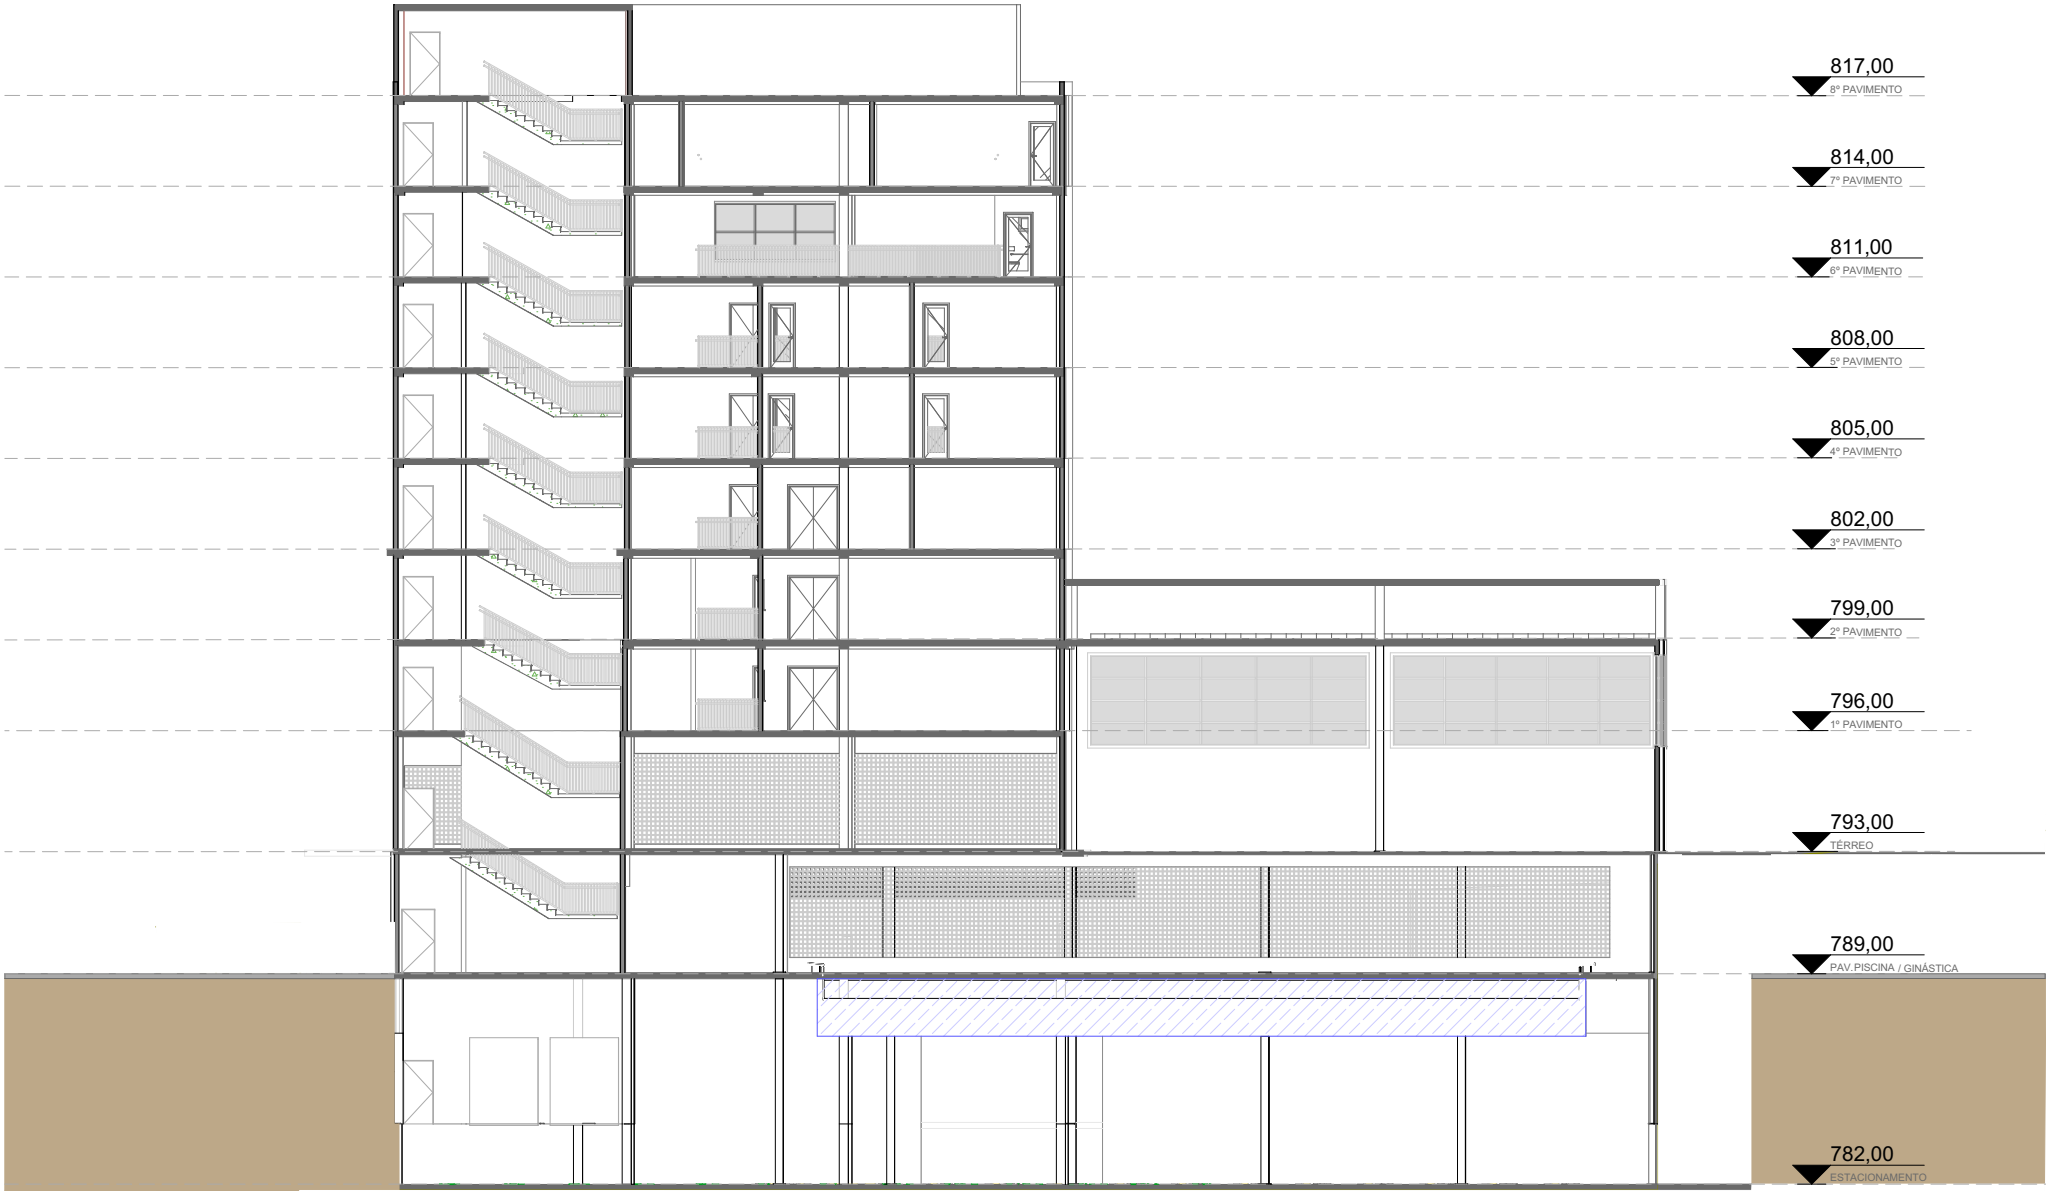

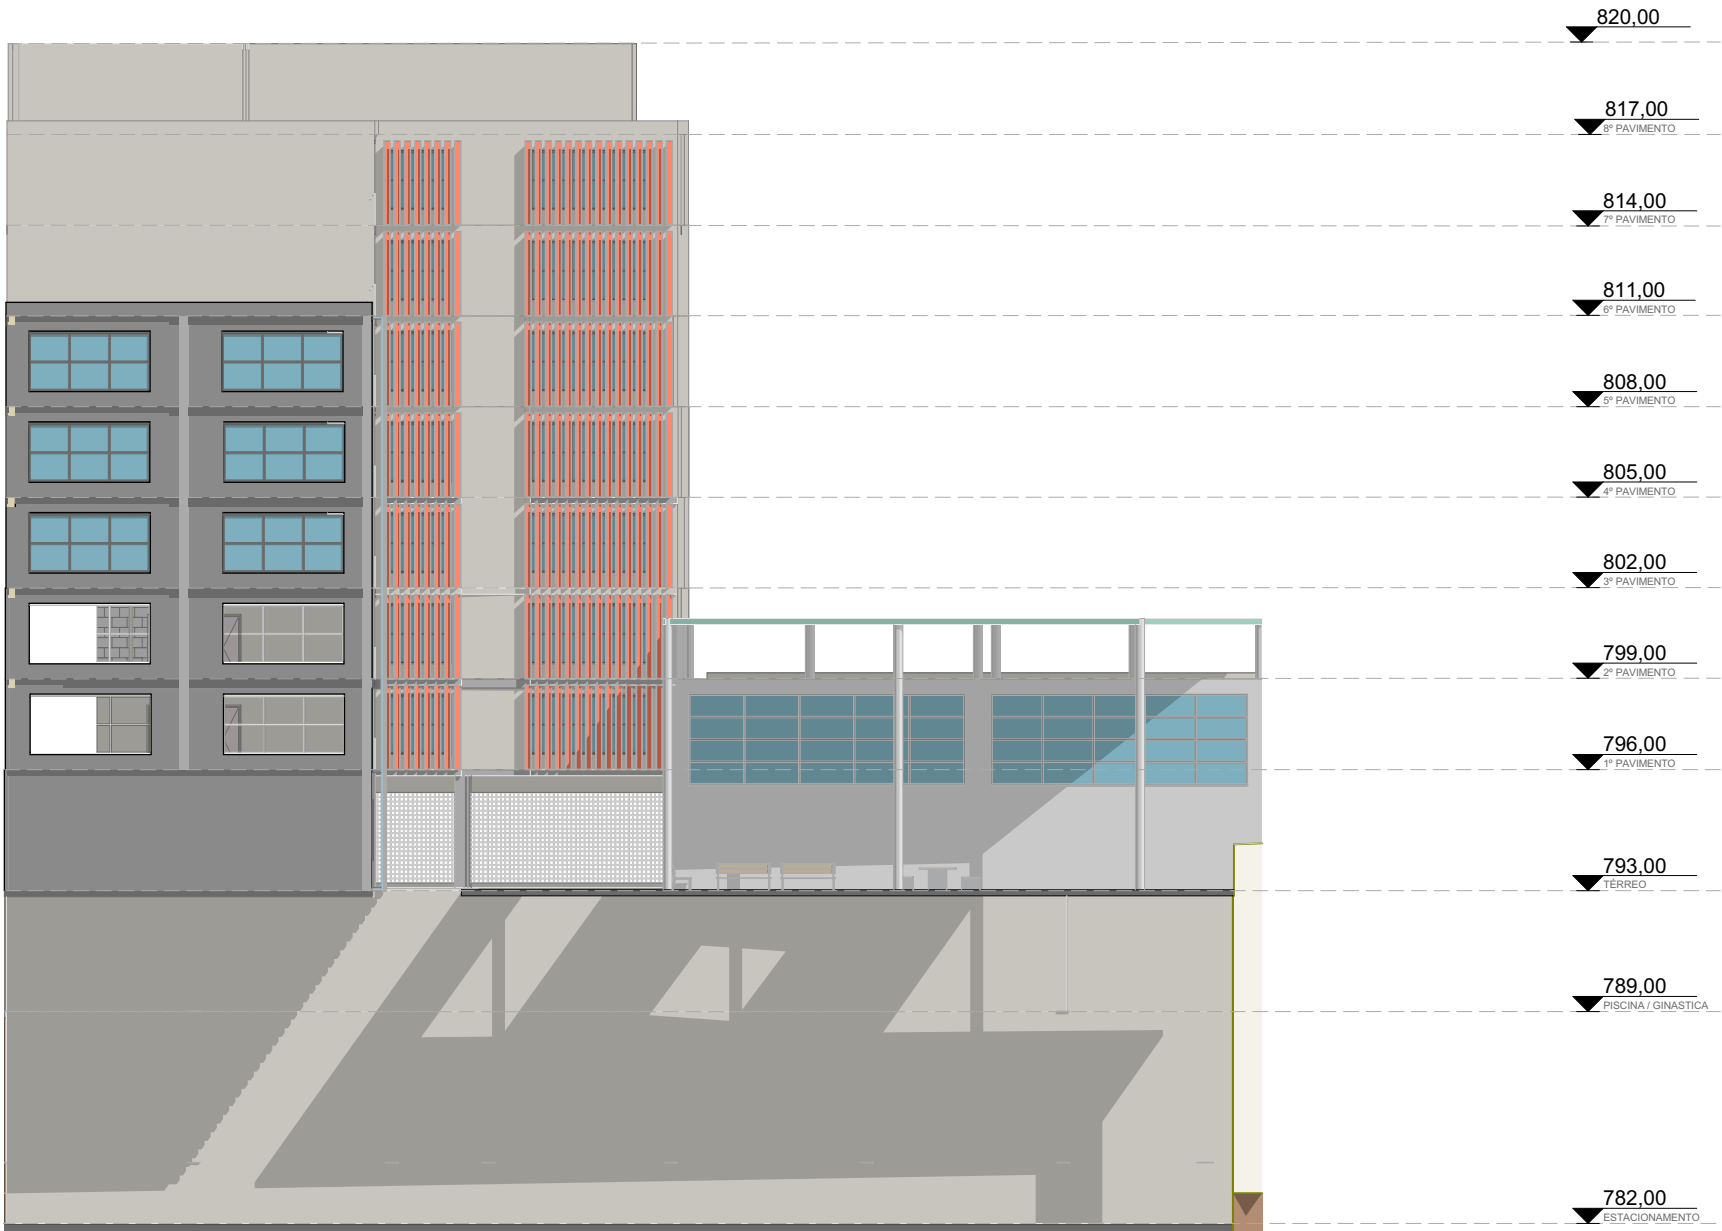

CURSO  
PROJETO PARA EDIFÍCIOS MULTIFUNCIONAIS  
PROJETO  
CEU BELA VISTA

CAMPUS  
CHACARÁ SANTO ANTÔNIO

CONTEÚDO: ELEVÇÃO A2 ESCALA 1:250

NOME DO ALUNO: MONICA CLEIA SOUSA CARVALHO

RA: G73EAE6

ARQUIVO DIGITAL  
IMPLANTAÇÃO E CORTES.bpn

