


RUA DR. ANTÔNIO BENTO

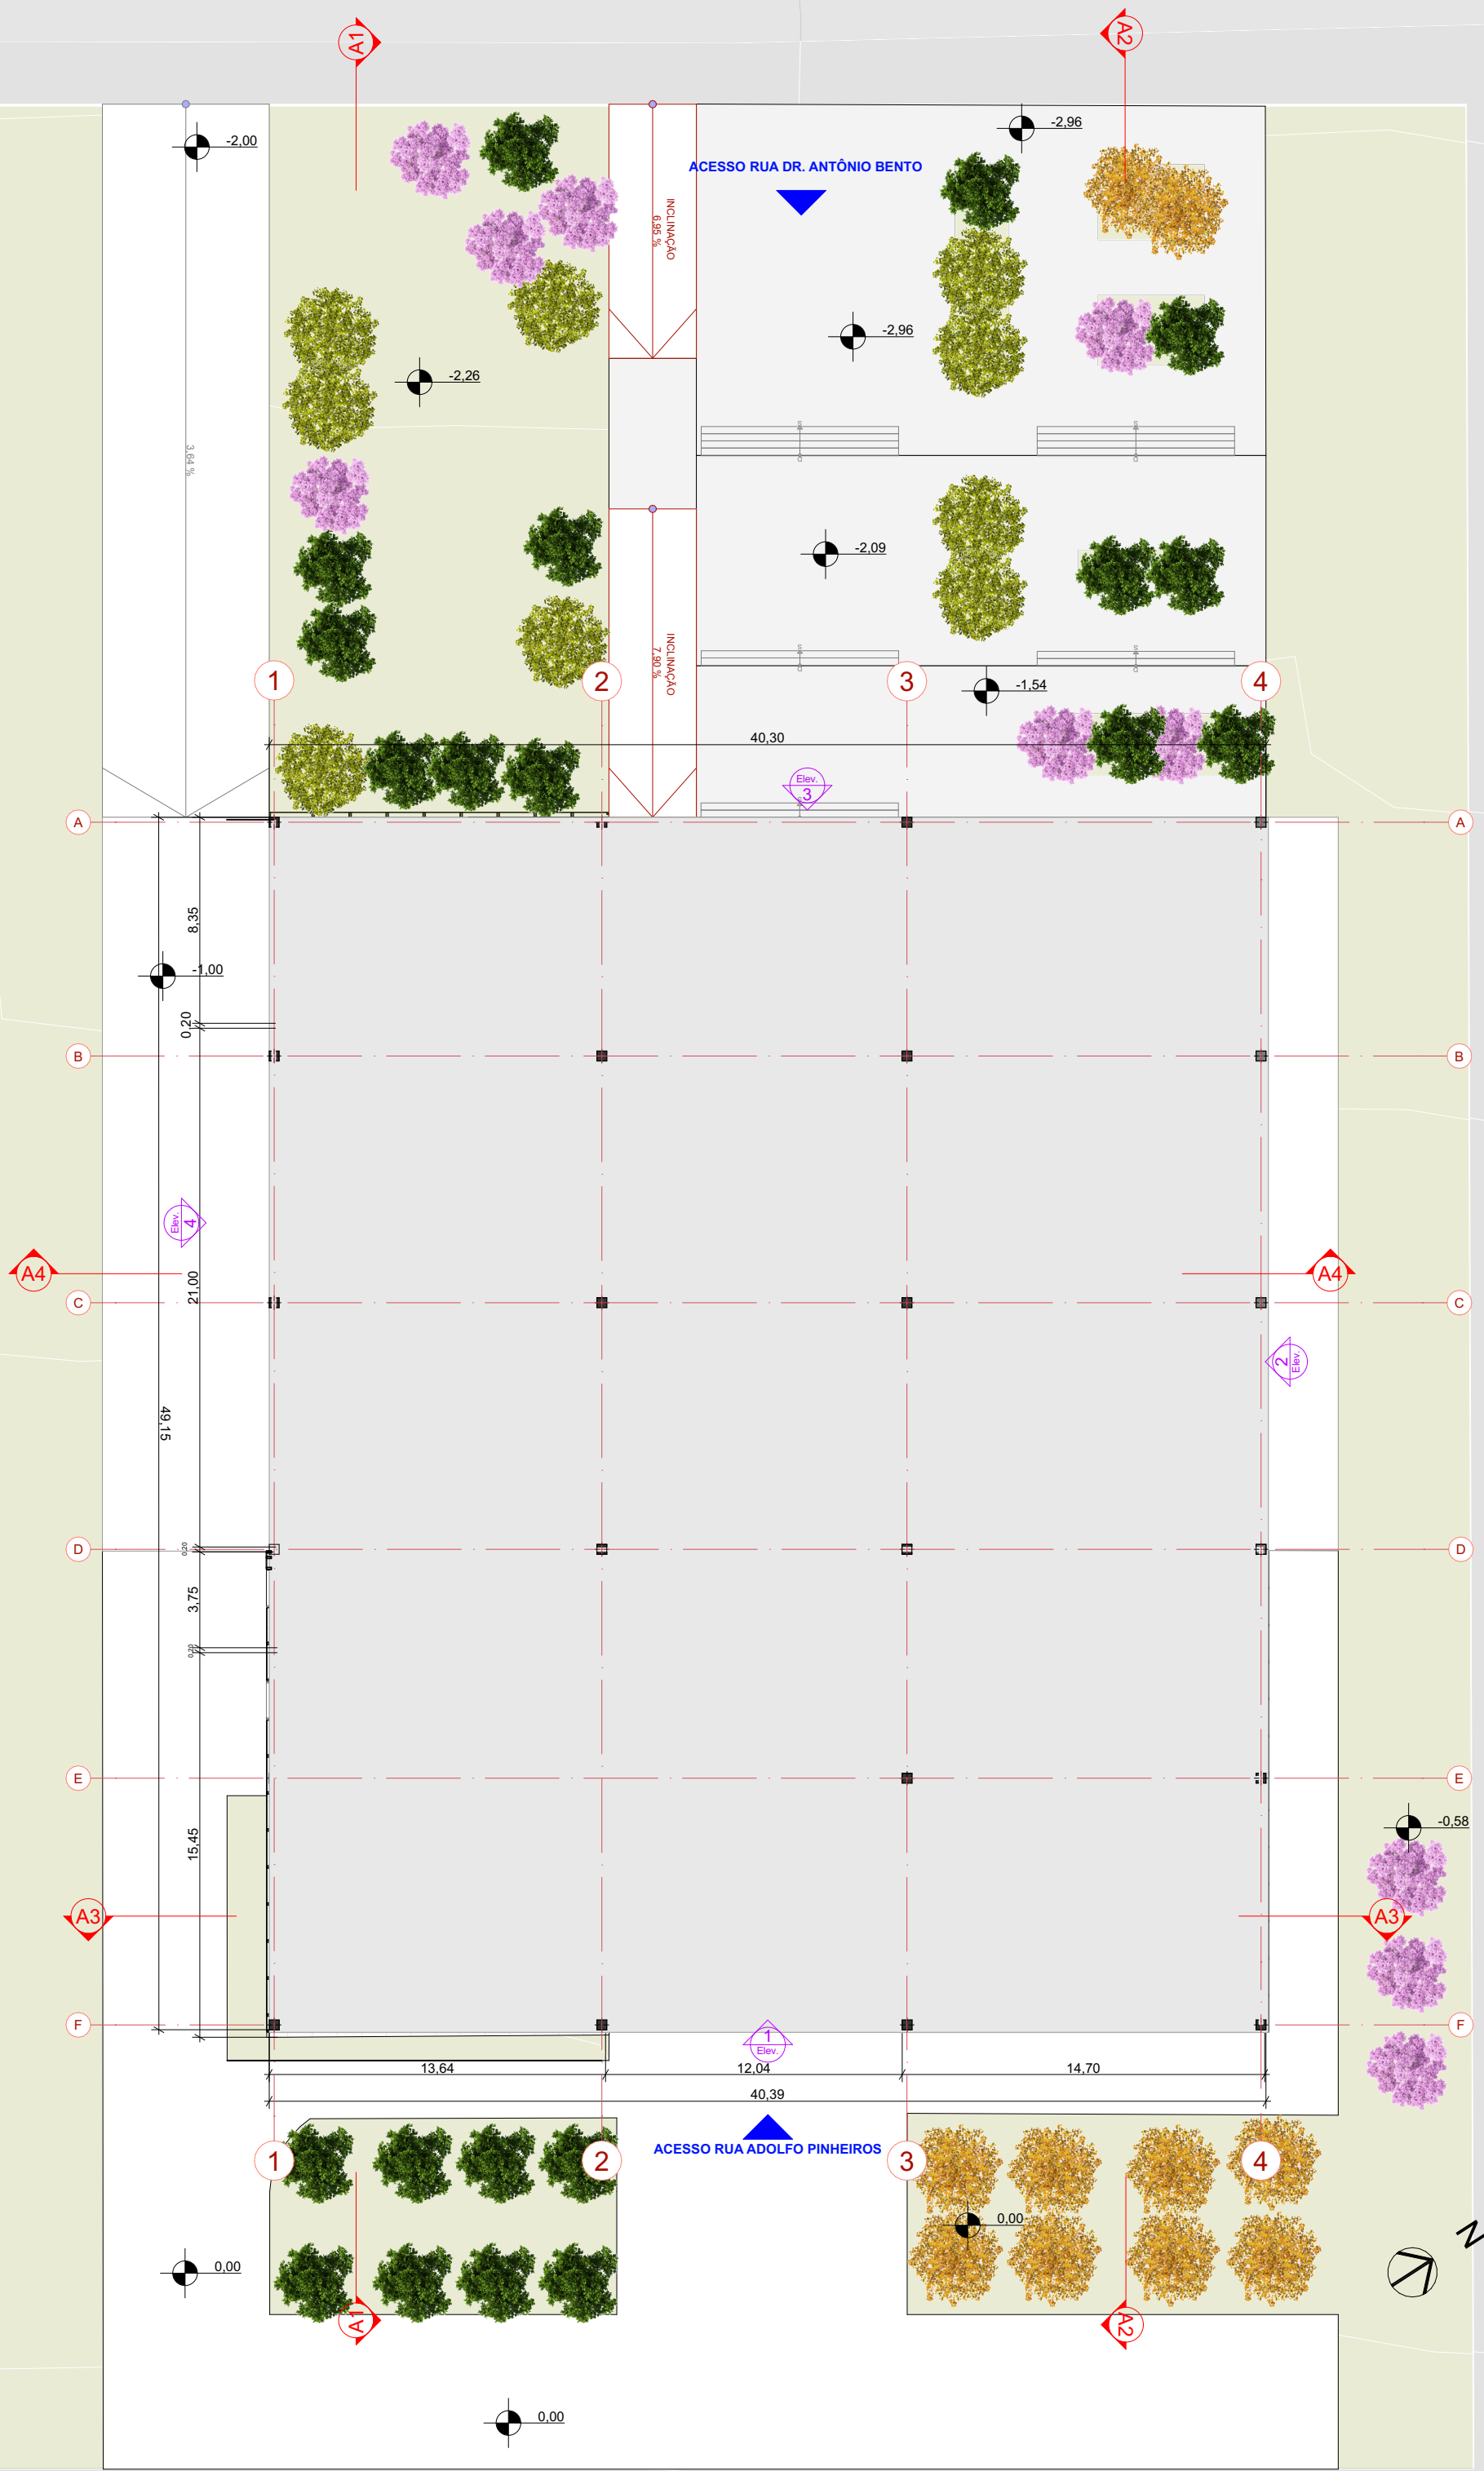



AVENIDA ADOLFO PINHEIROS

RUA SALOMÃO KARLIK

RUA CONDE DE ITU

AVENIDA ADOLFO PINHEIROS

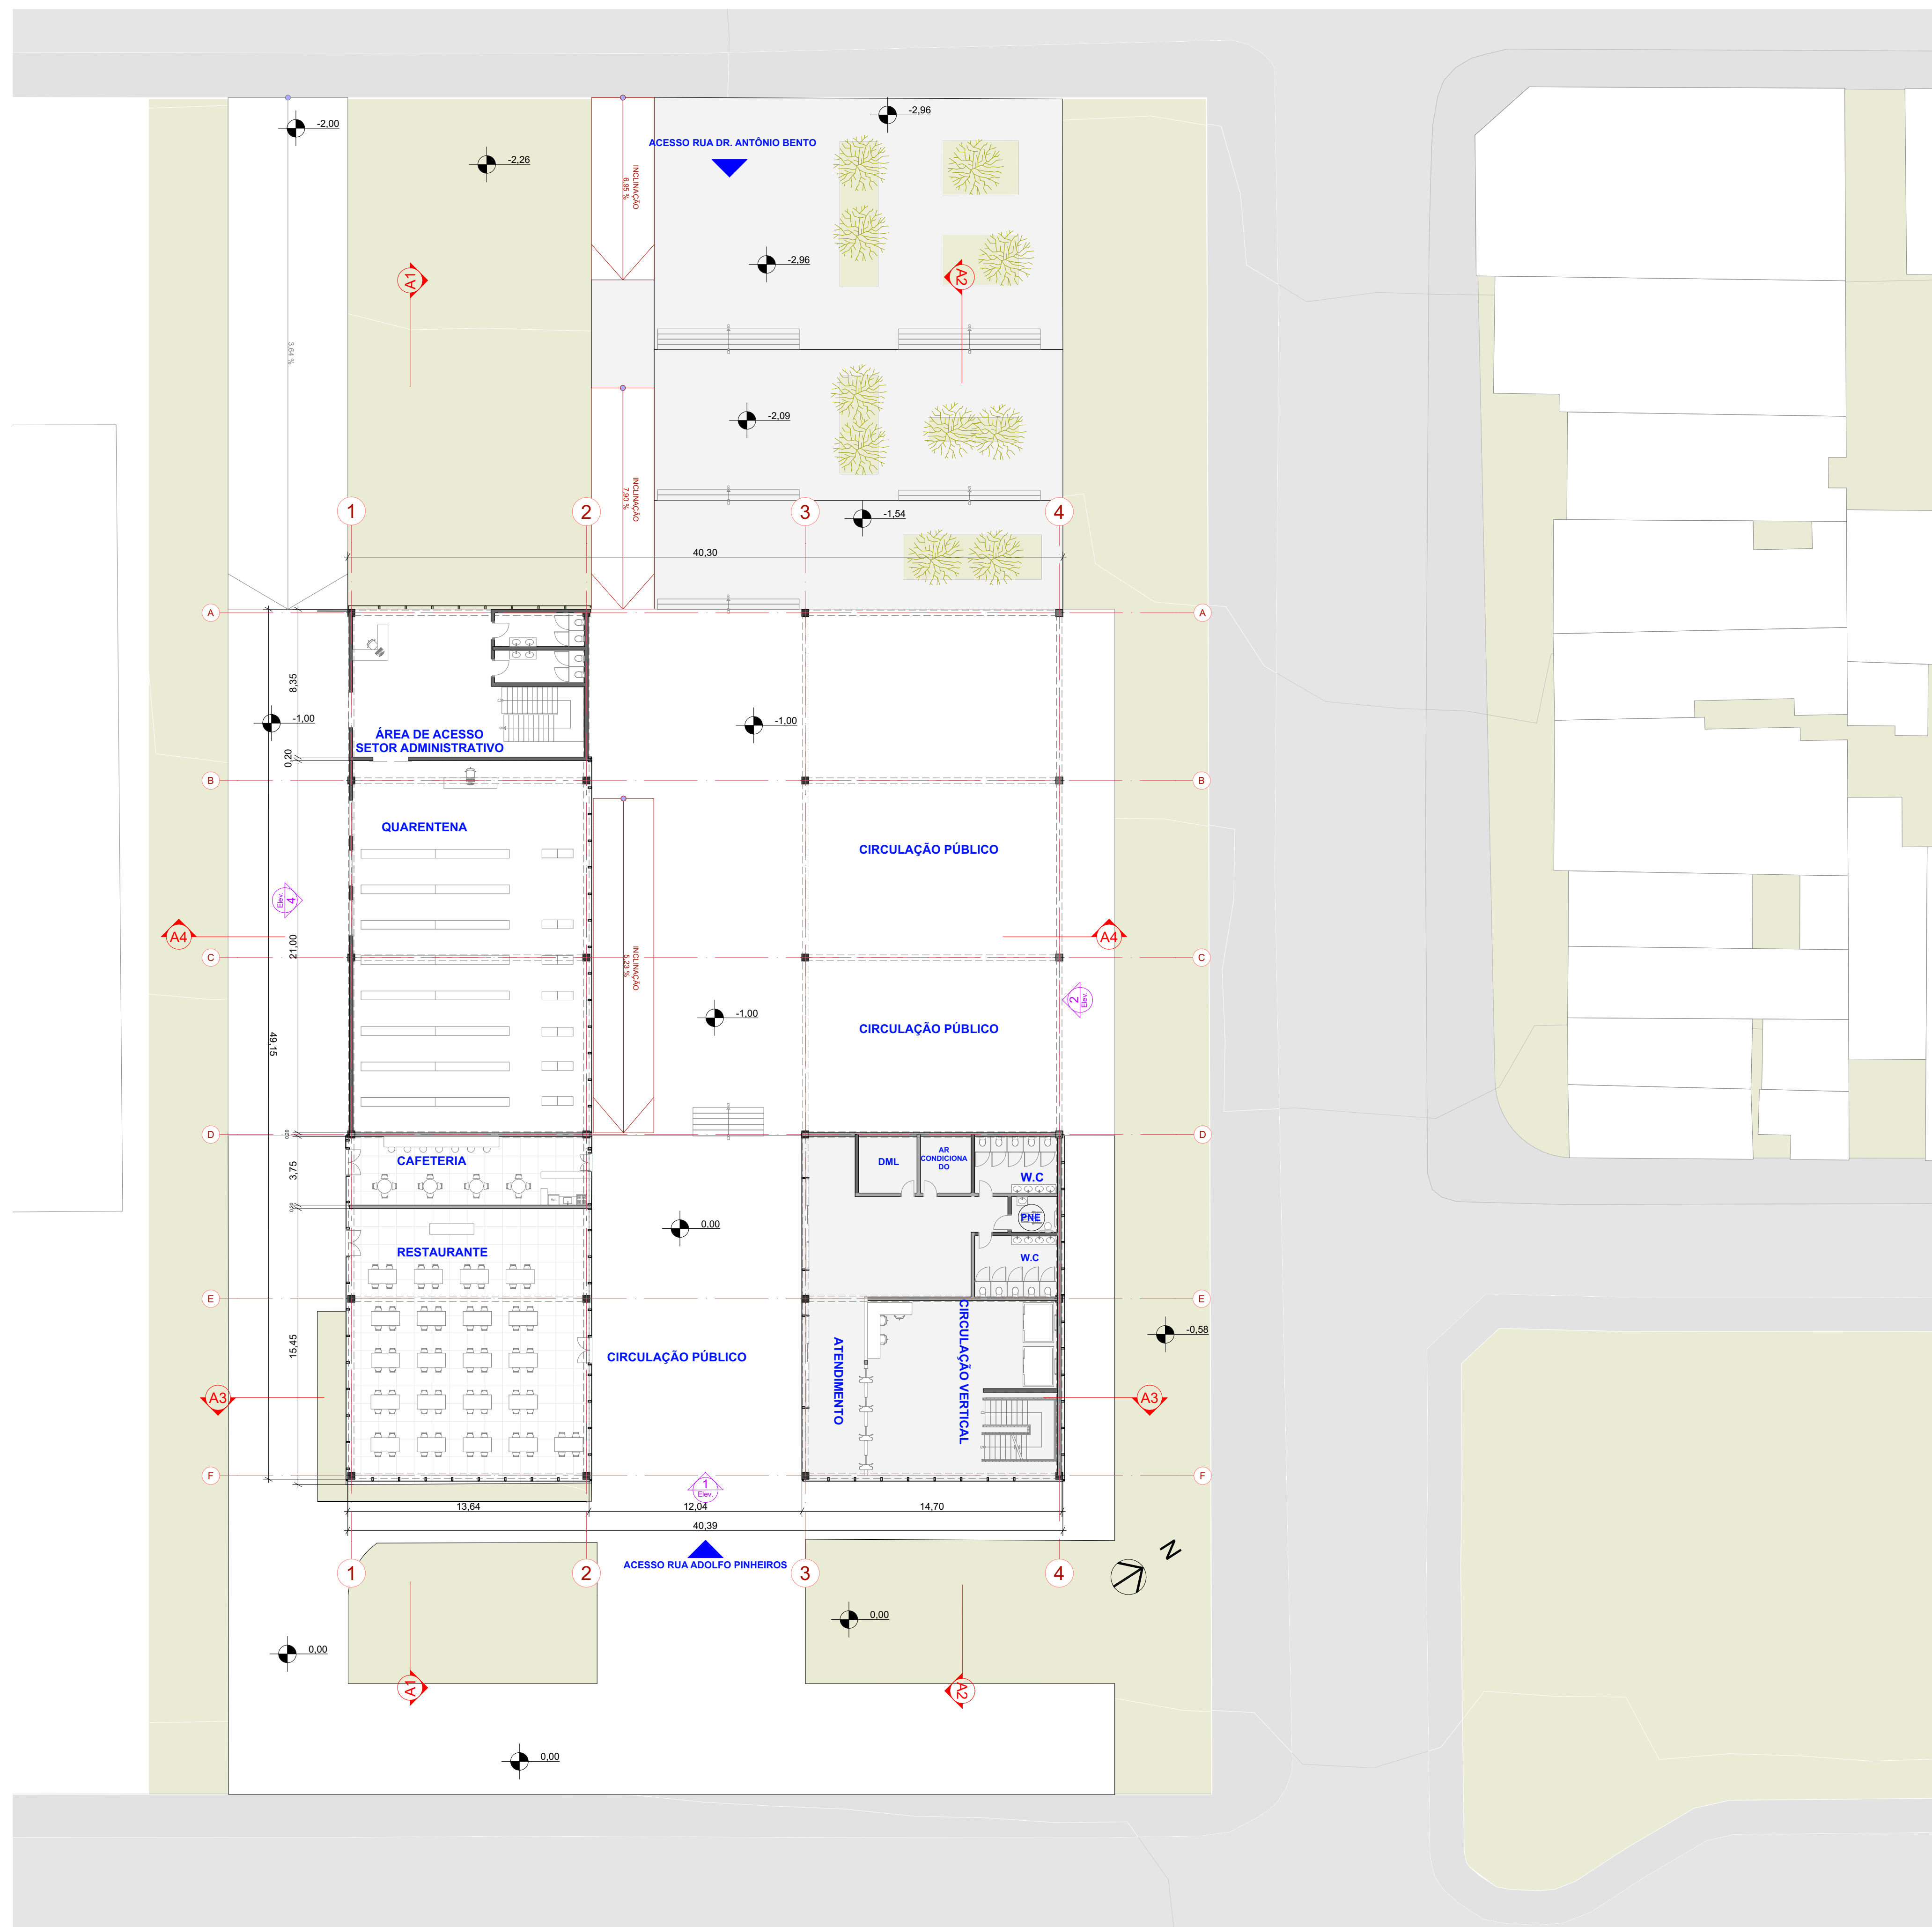


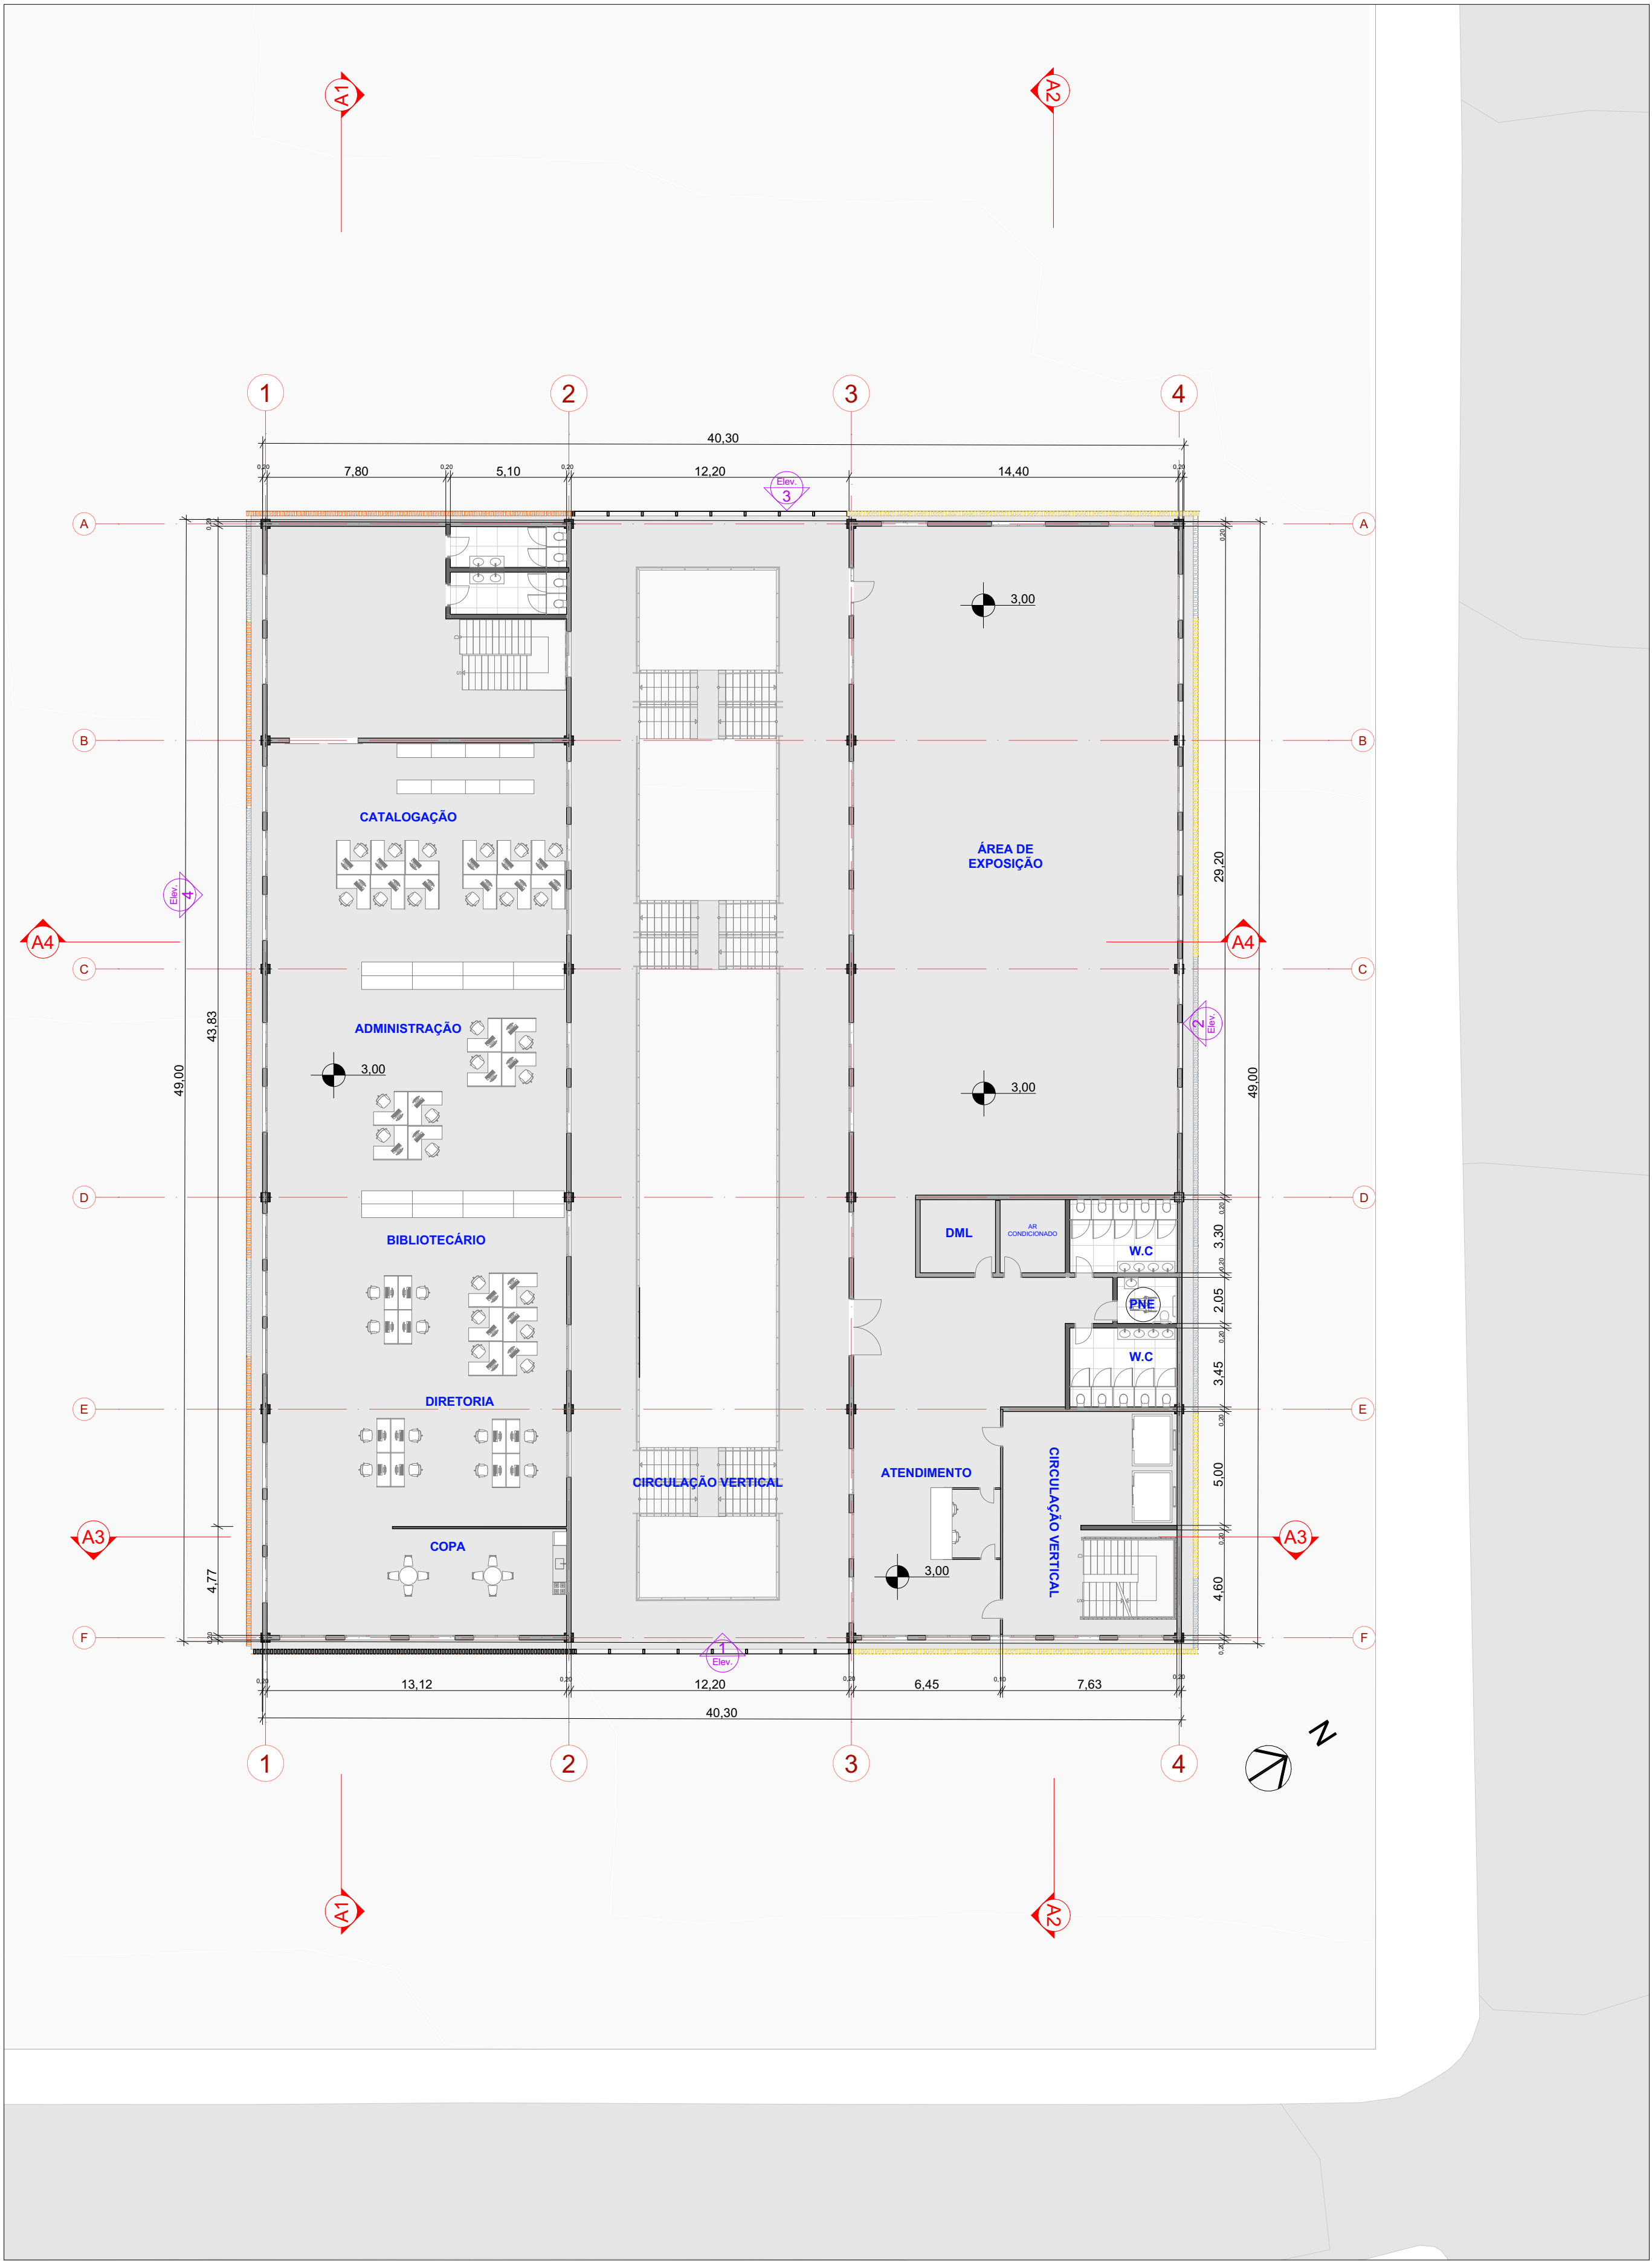

01

PLANTA 1º PAVIMENTO


1:200

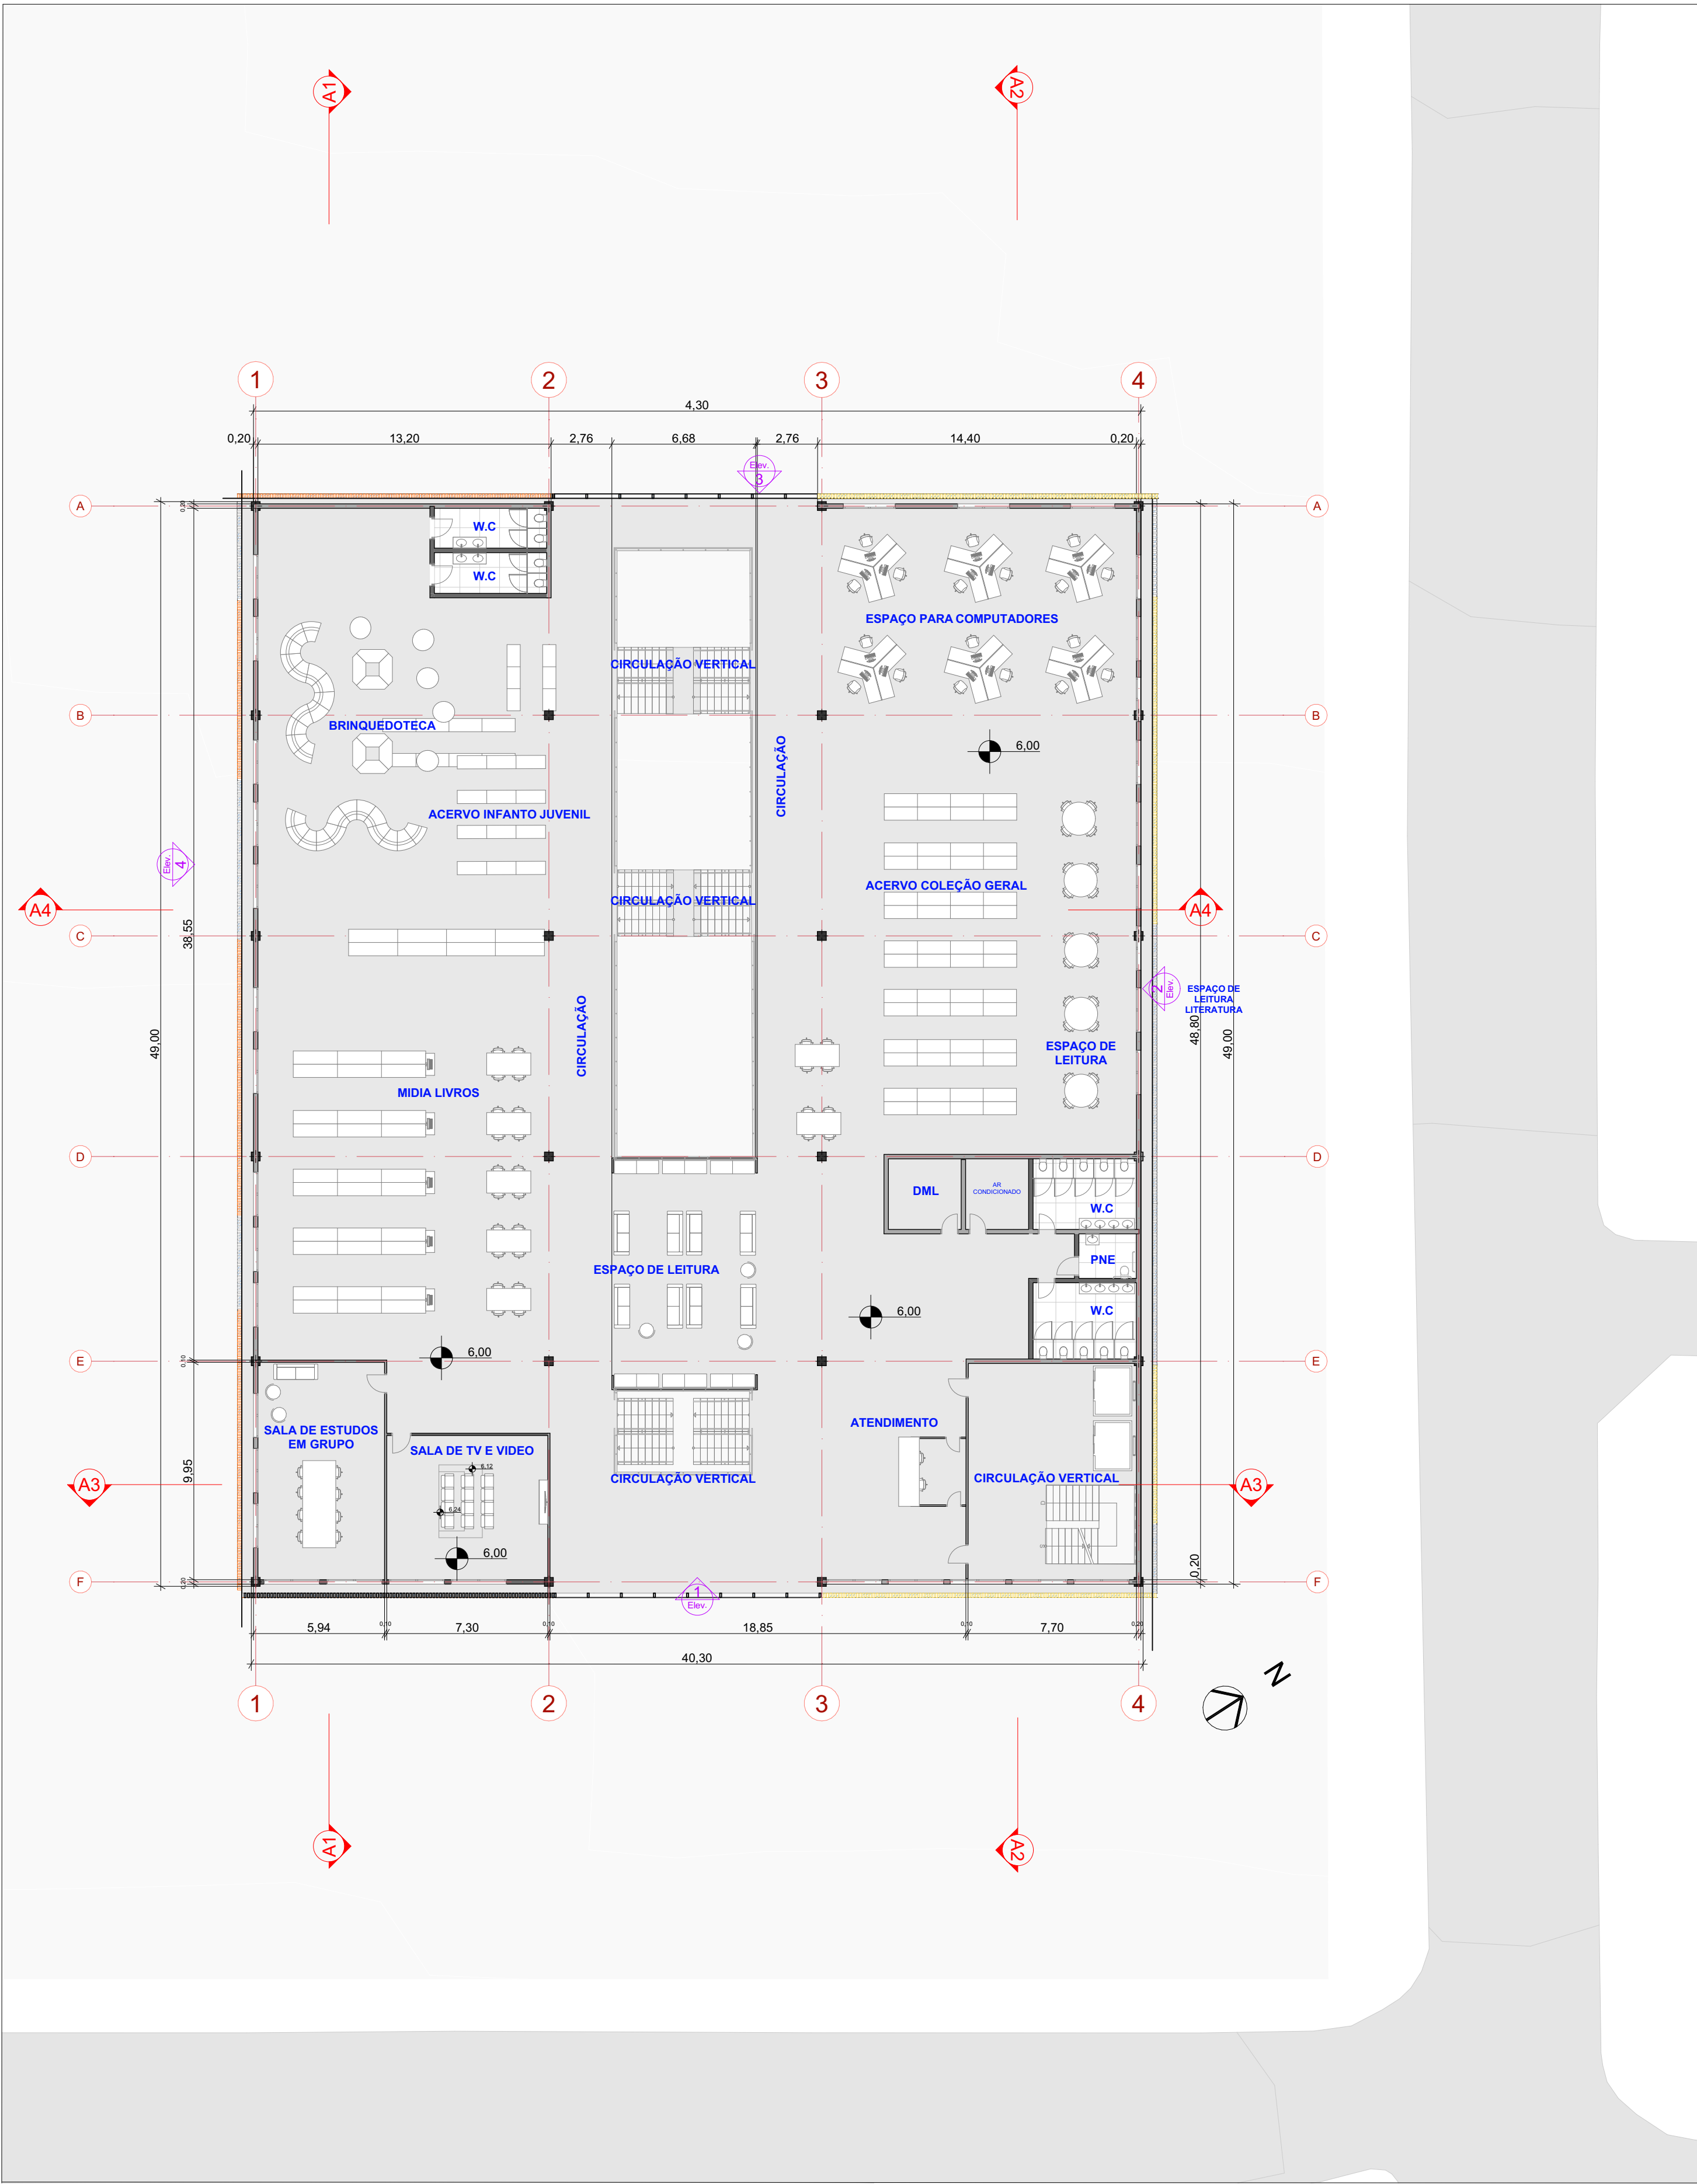

02


PLANTA 2º PAVIMENTO

1:200

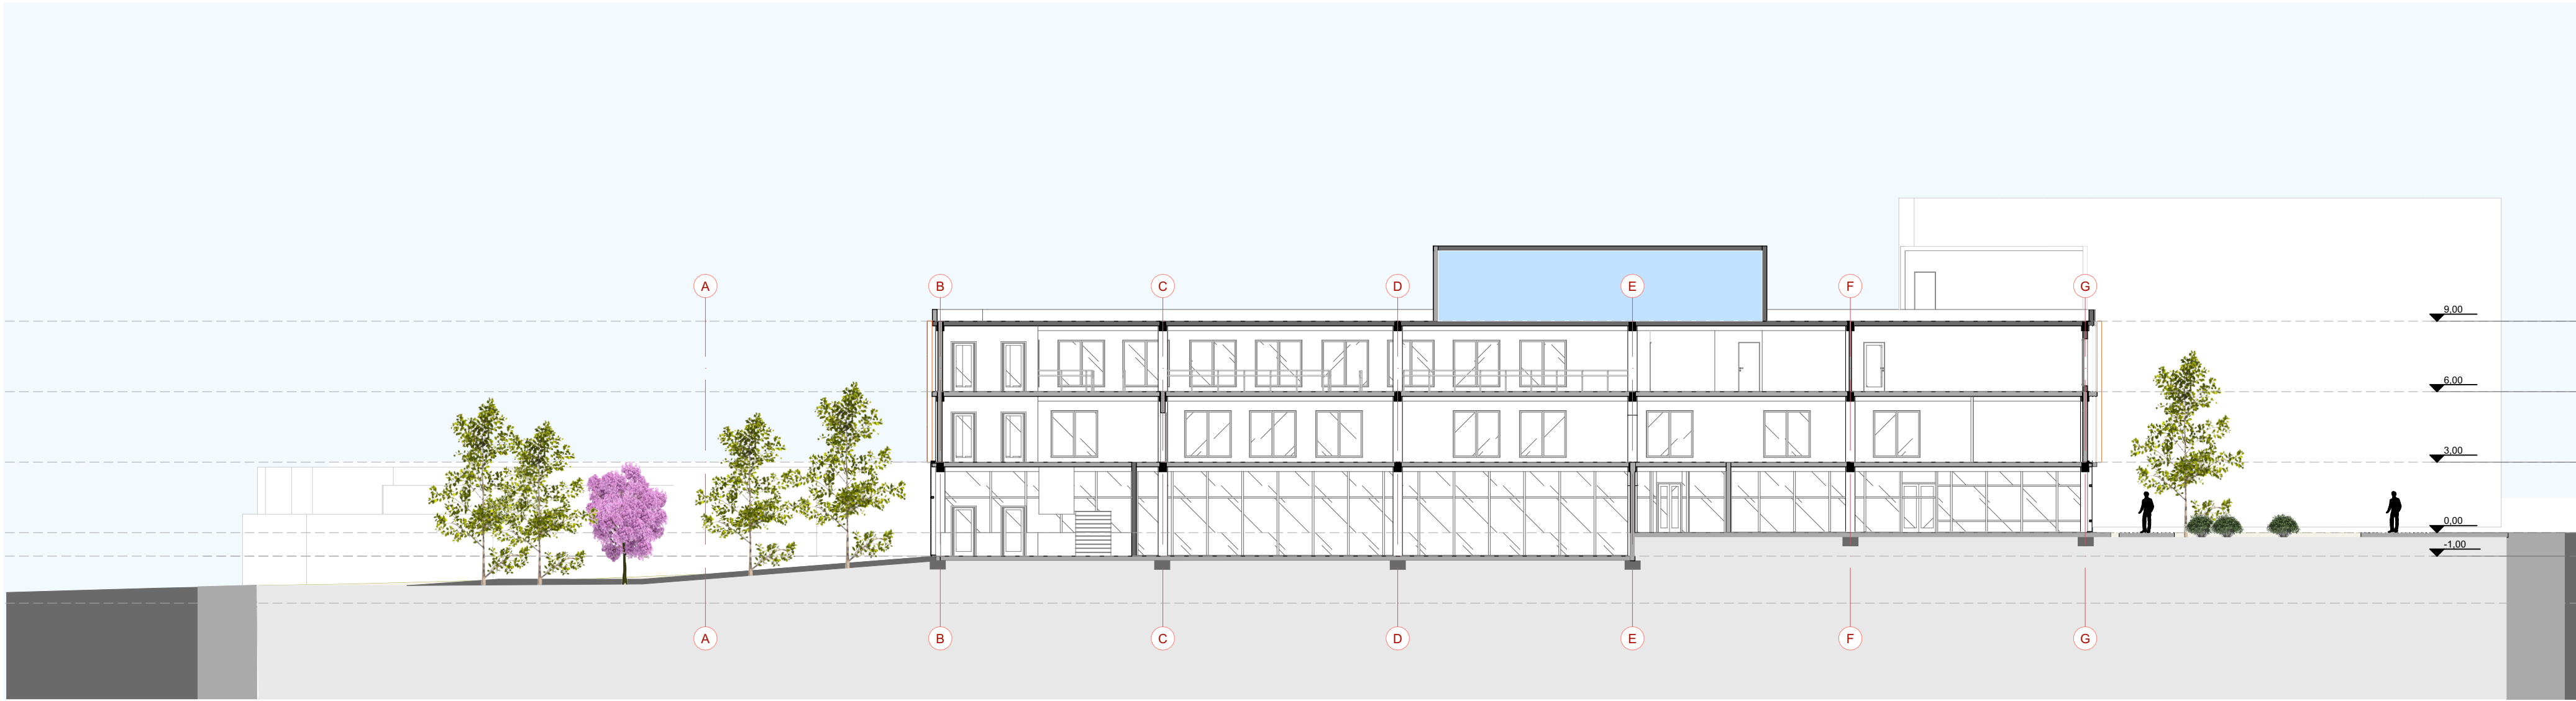


A1

CORTE A1
1:200

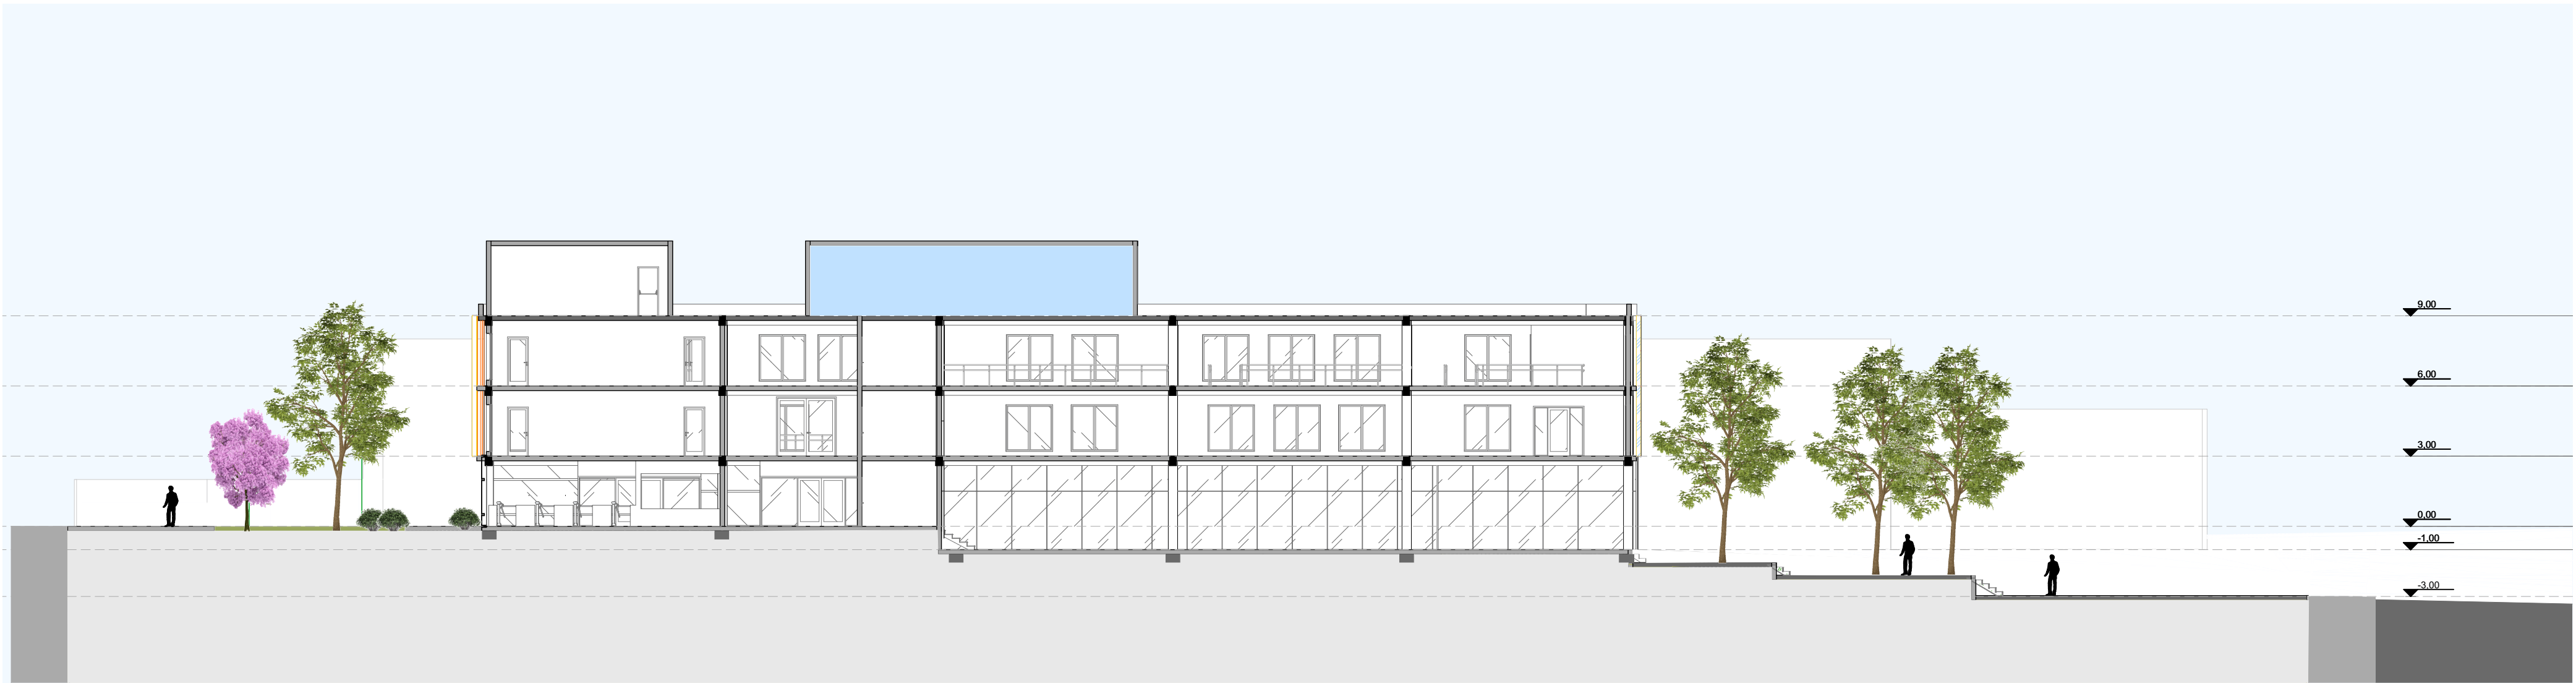


A2

CORTE A2
1:200

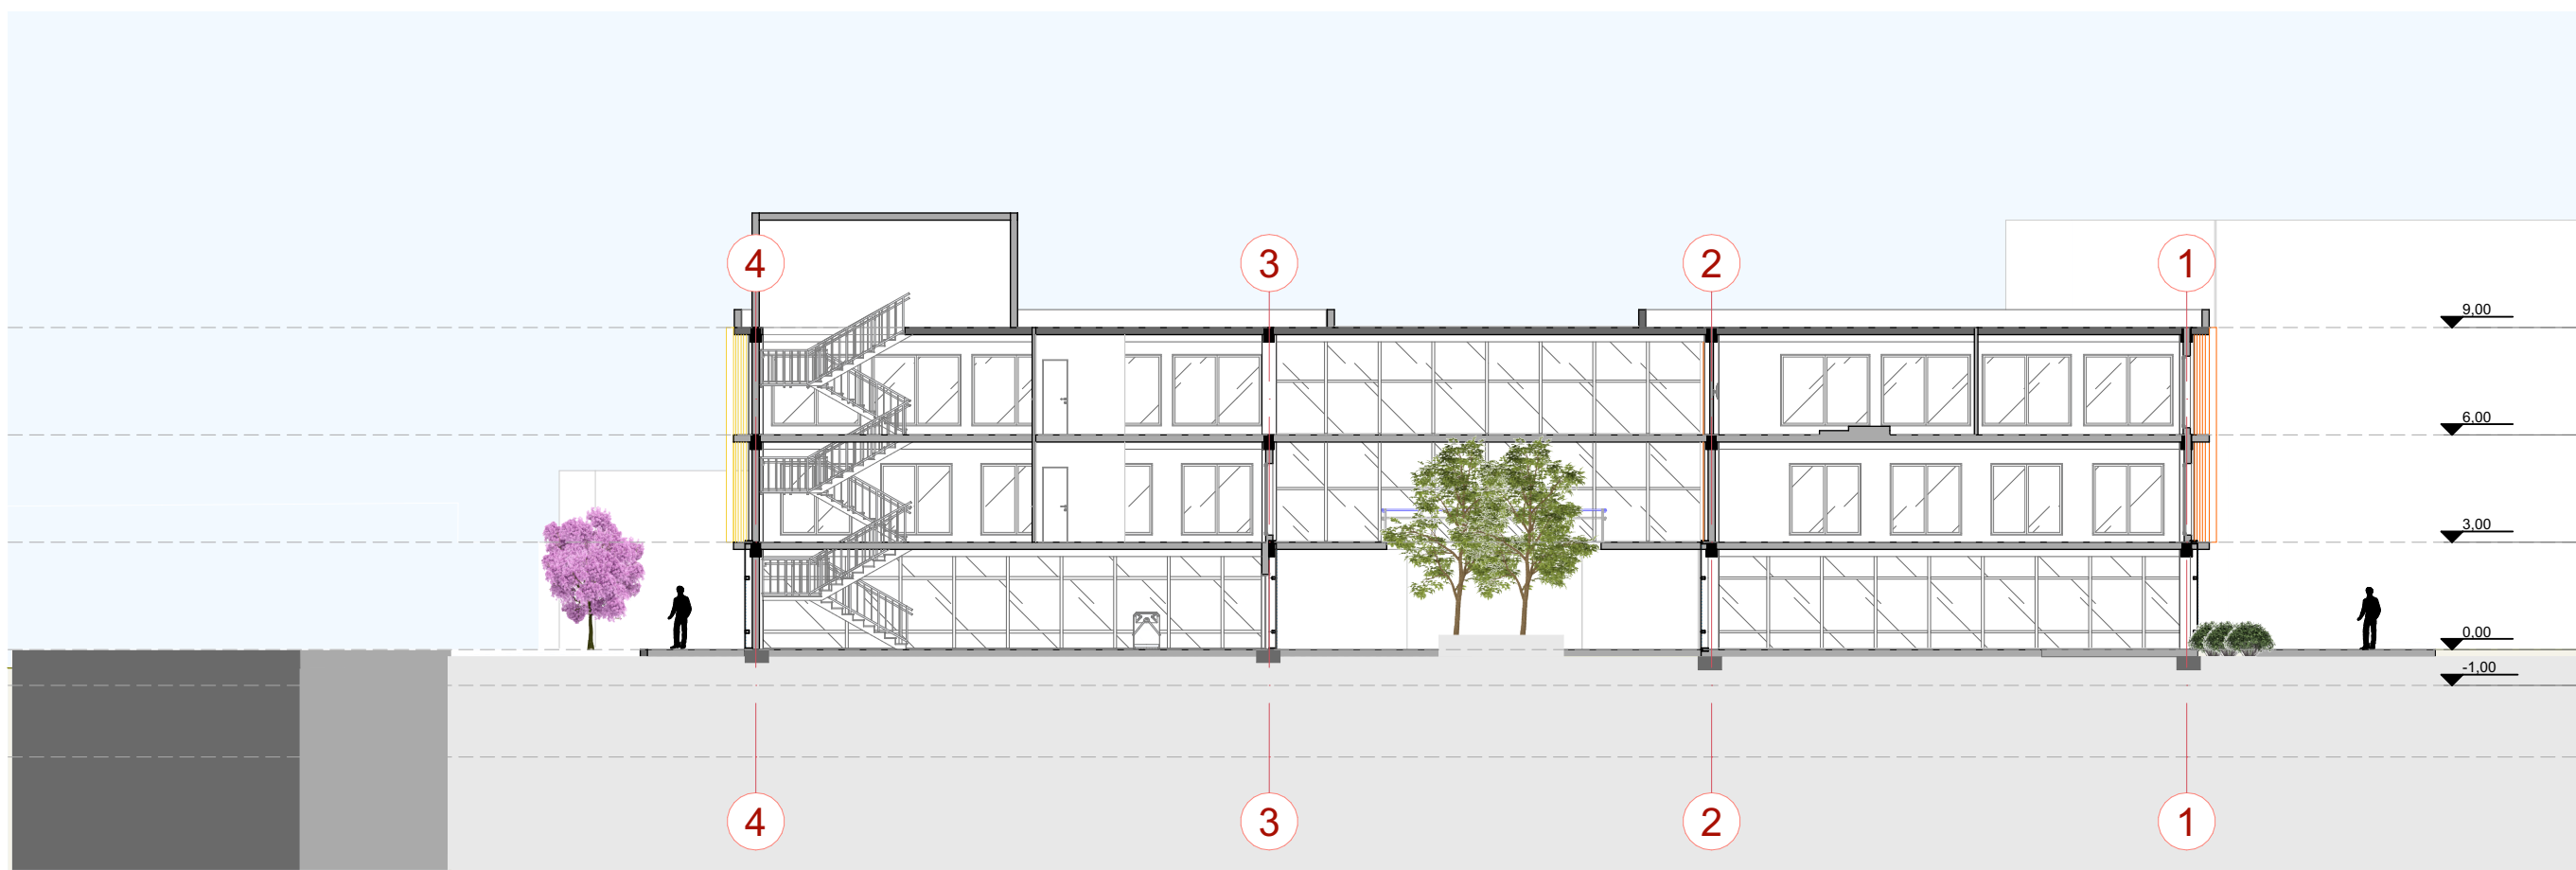

A3

CORTE A3
1:200

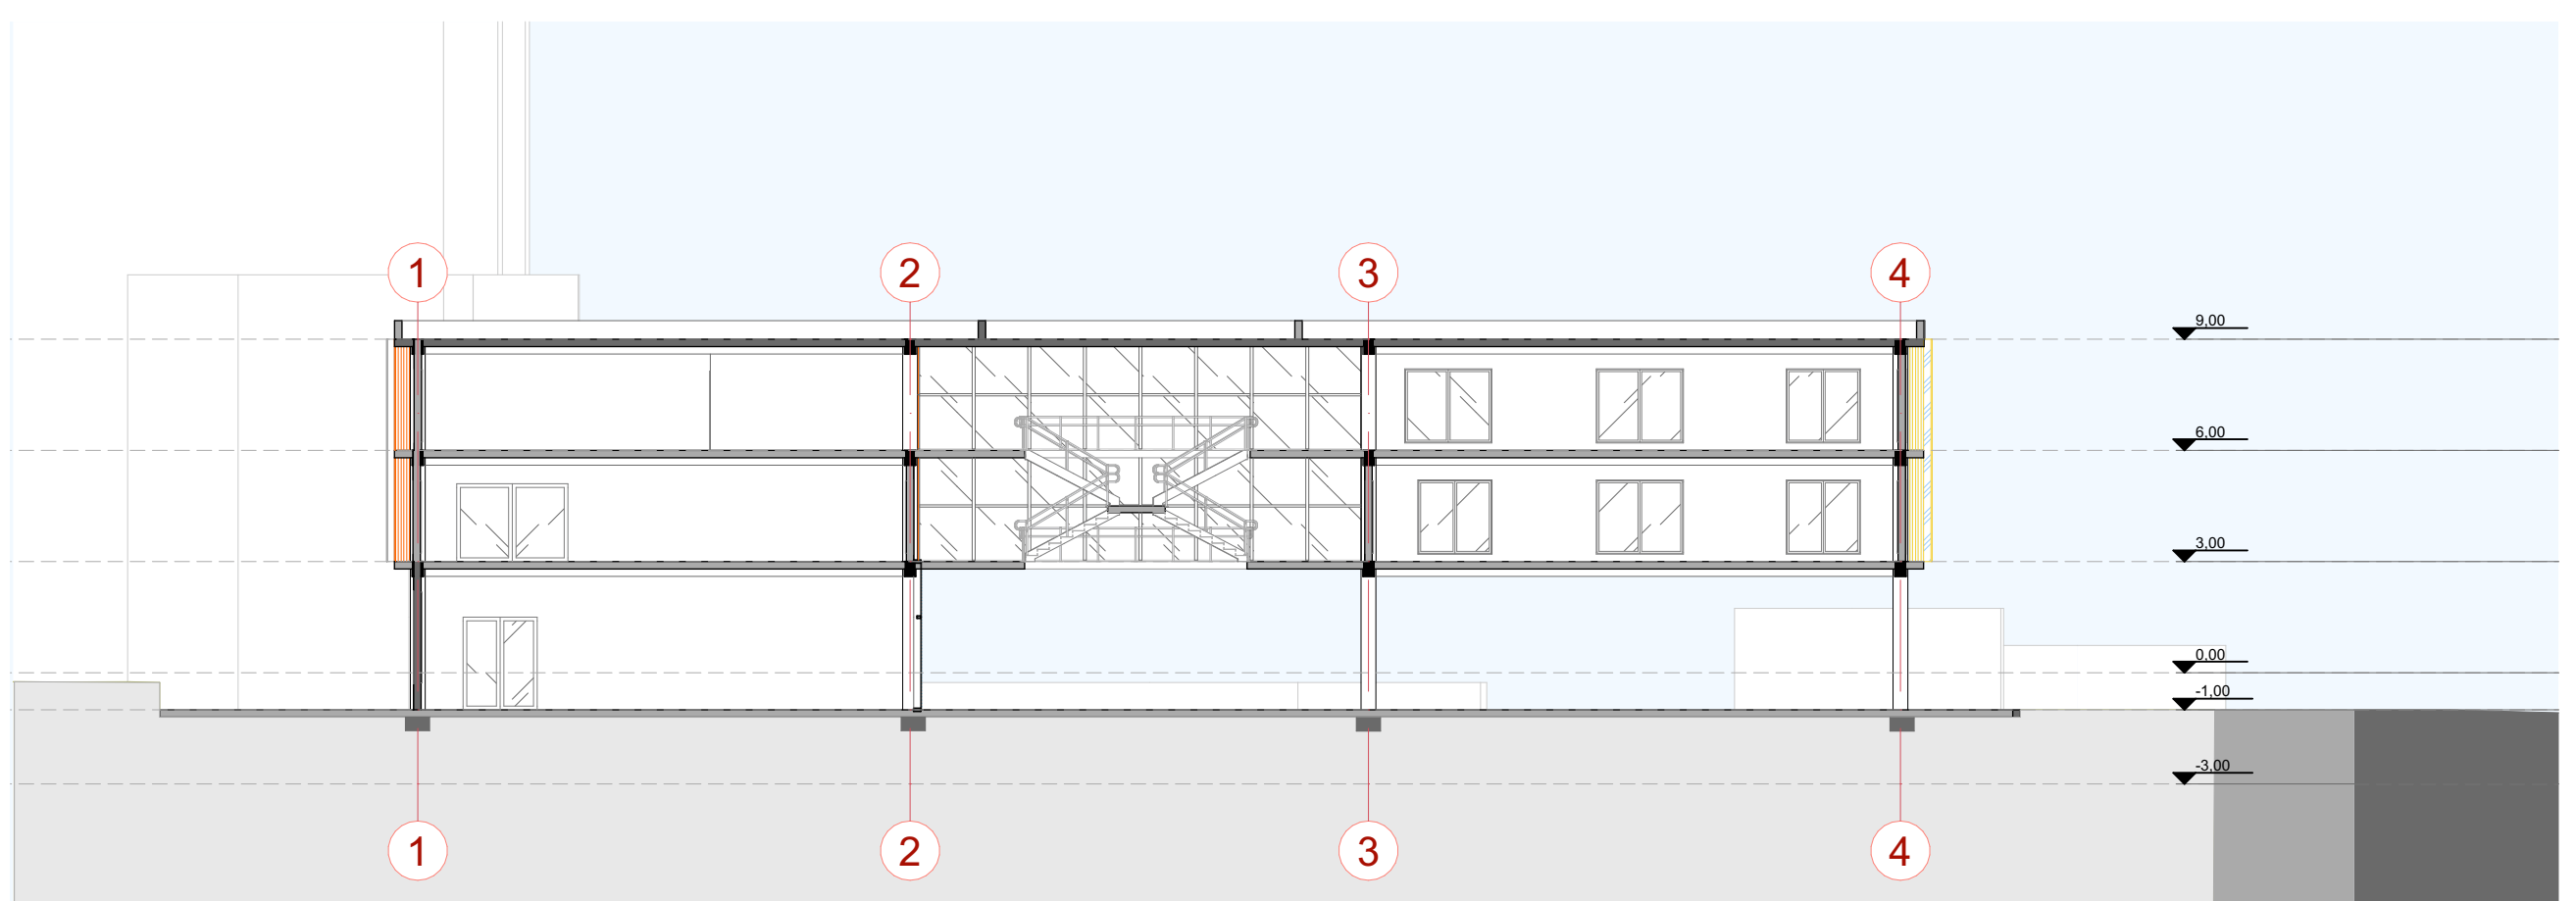

A4

CORTE A4
1:200

INSTITUIÇÃO
UNIP
UNIVERSIDADE PAULISTA

DISCIPLINA
PROJETO ARQUITETÔNICO
INTERVENÇÃO URBANA
PROFESSORA
ARNALDO MACHADO

CURSO
ARQUITETURA & URBANISMO
CAMPUS
CHACARA SANTO ANTÔNIO III
TURMA
AU7P40

TÍTULO
CORTES A1 A2 A3 A4

FOLHA
04


AUTORA:
MONICA CLEIA SOUSA CARVALHO

ESCALA:
G73EAE6


ANO
2026




1 ELEVÇÃO 01
1:200

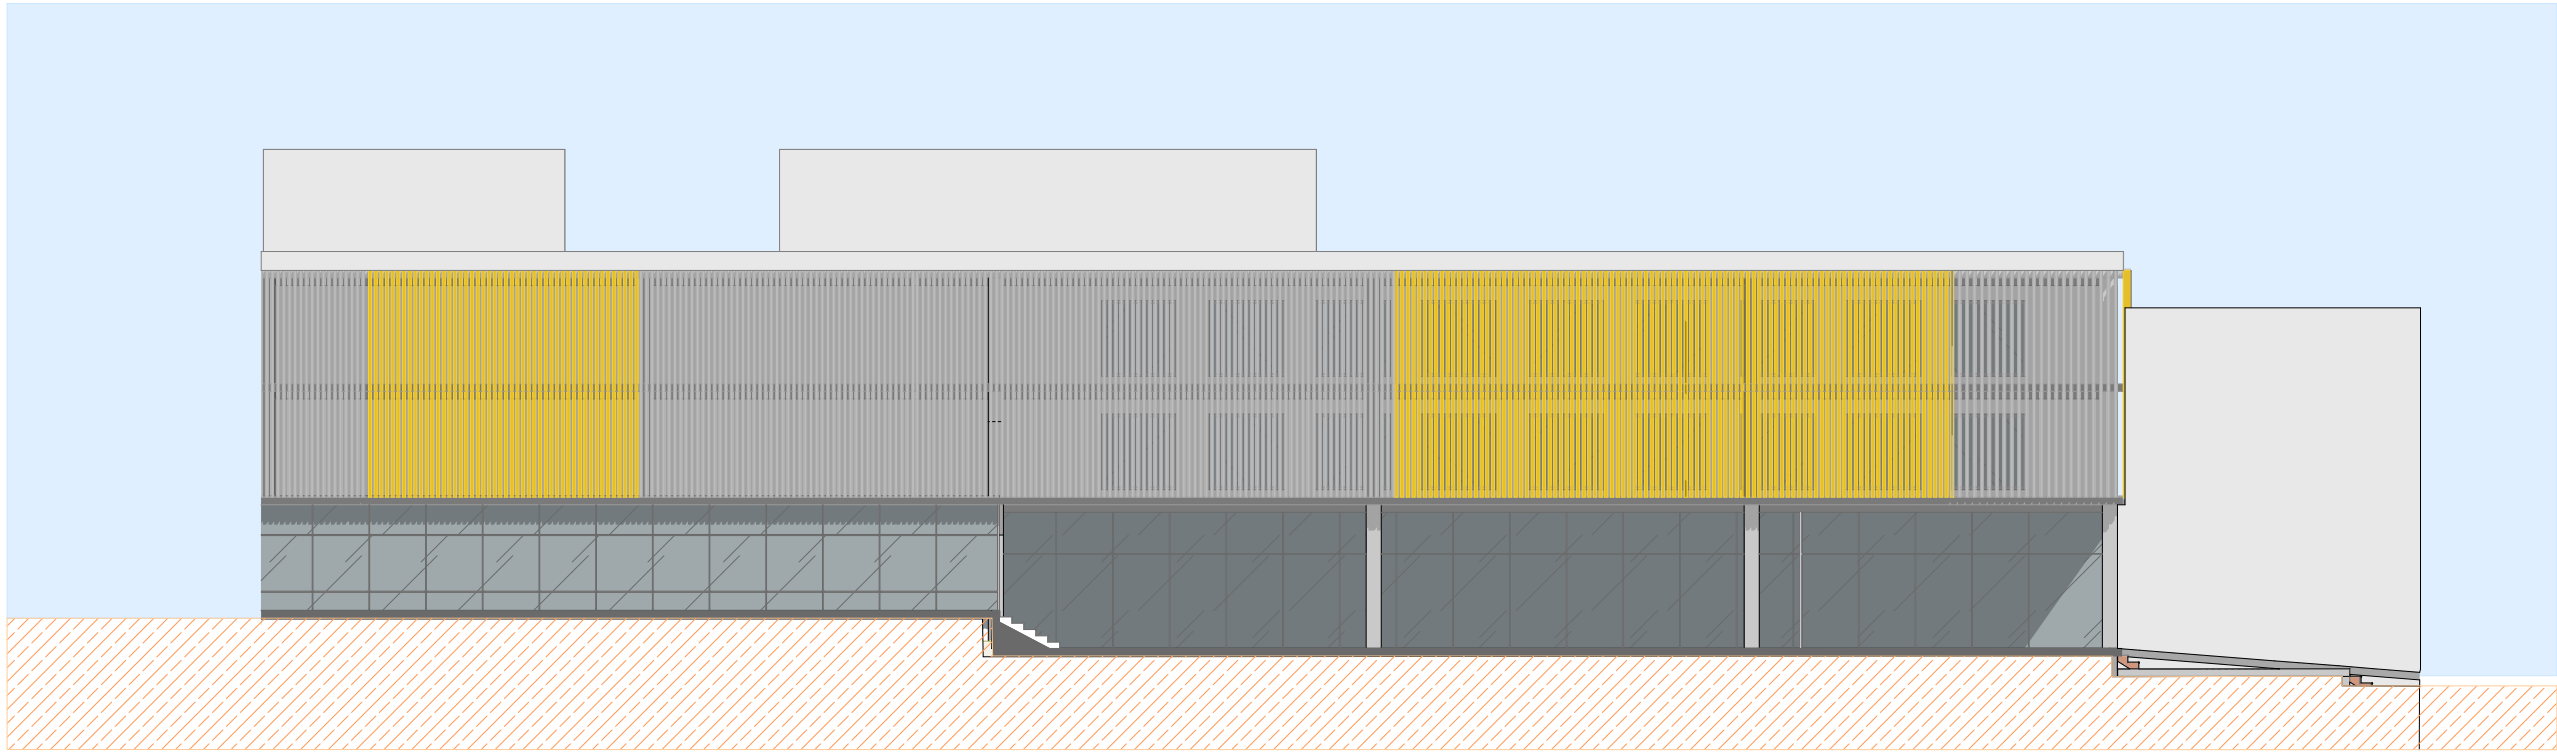


2 ELEVÇÃO 02
1:200

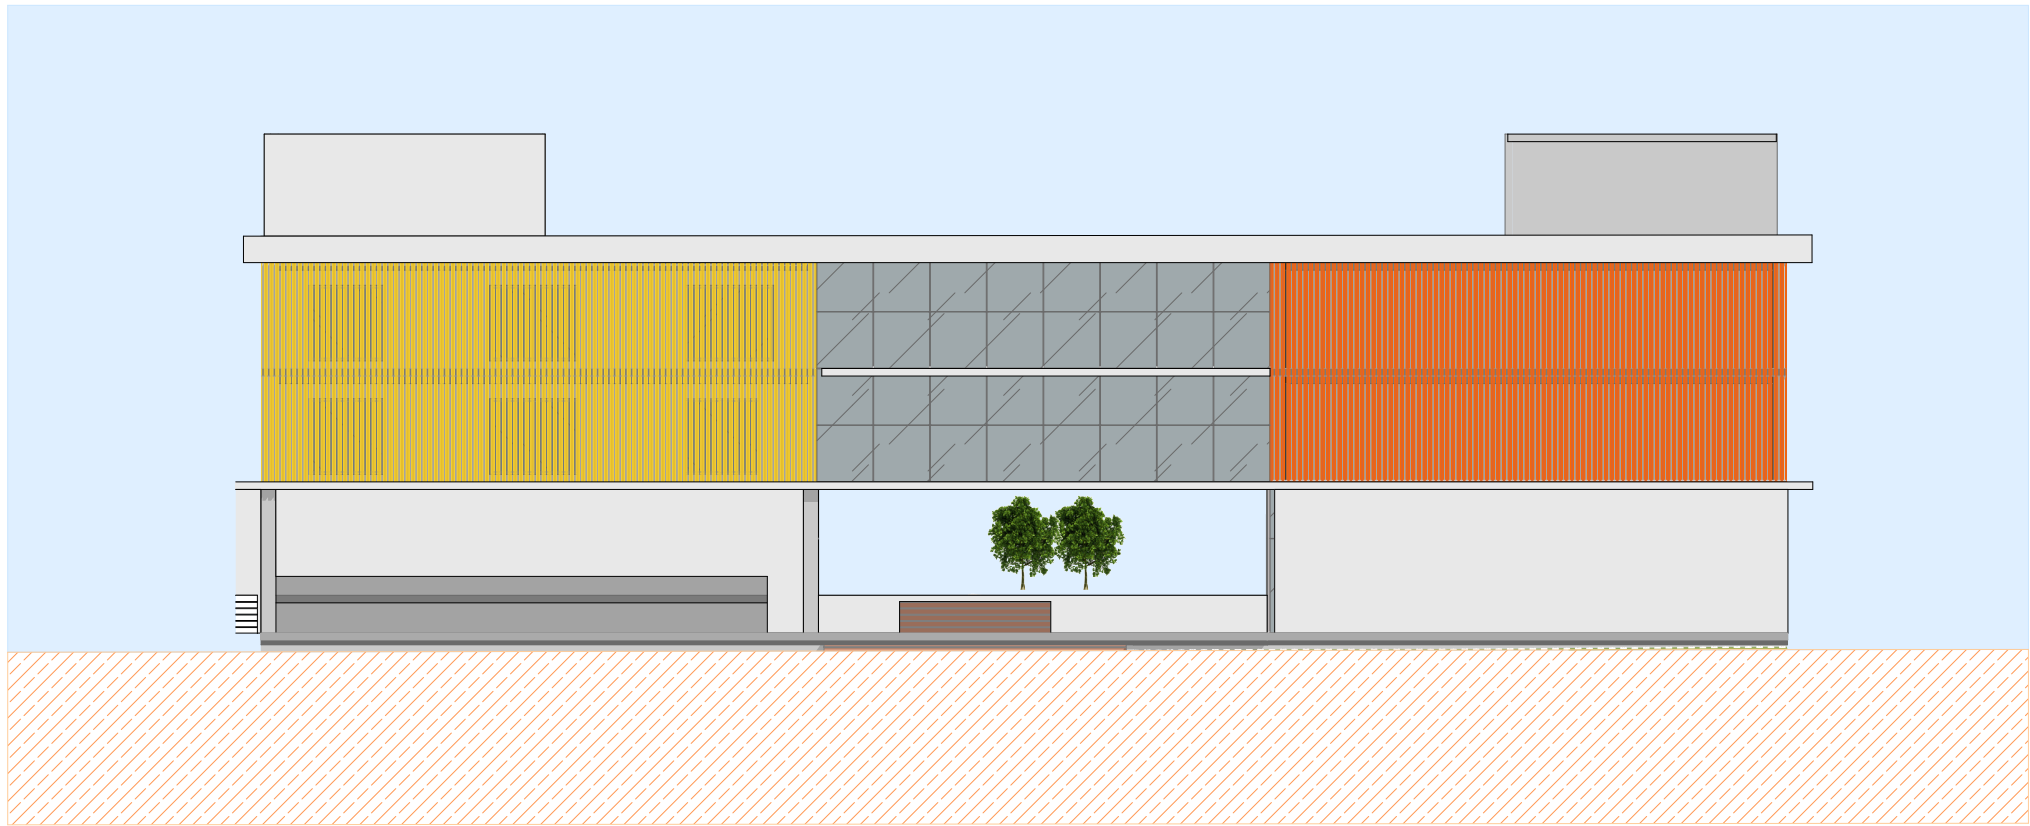


3 ELEVÇÃO 03
1:200

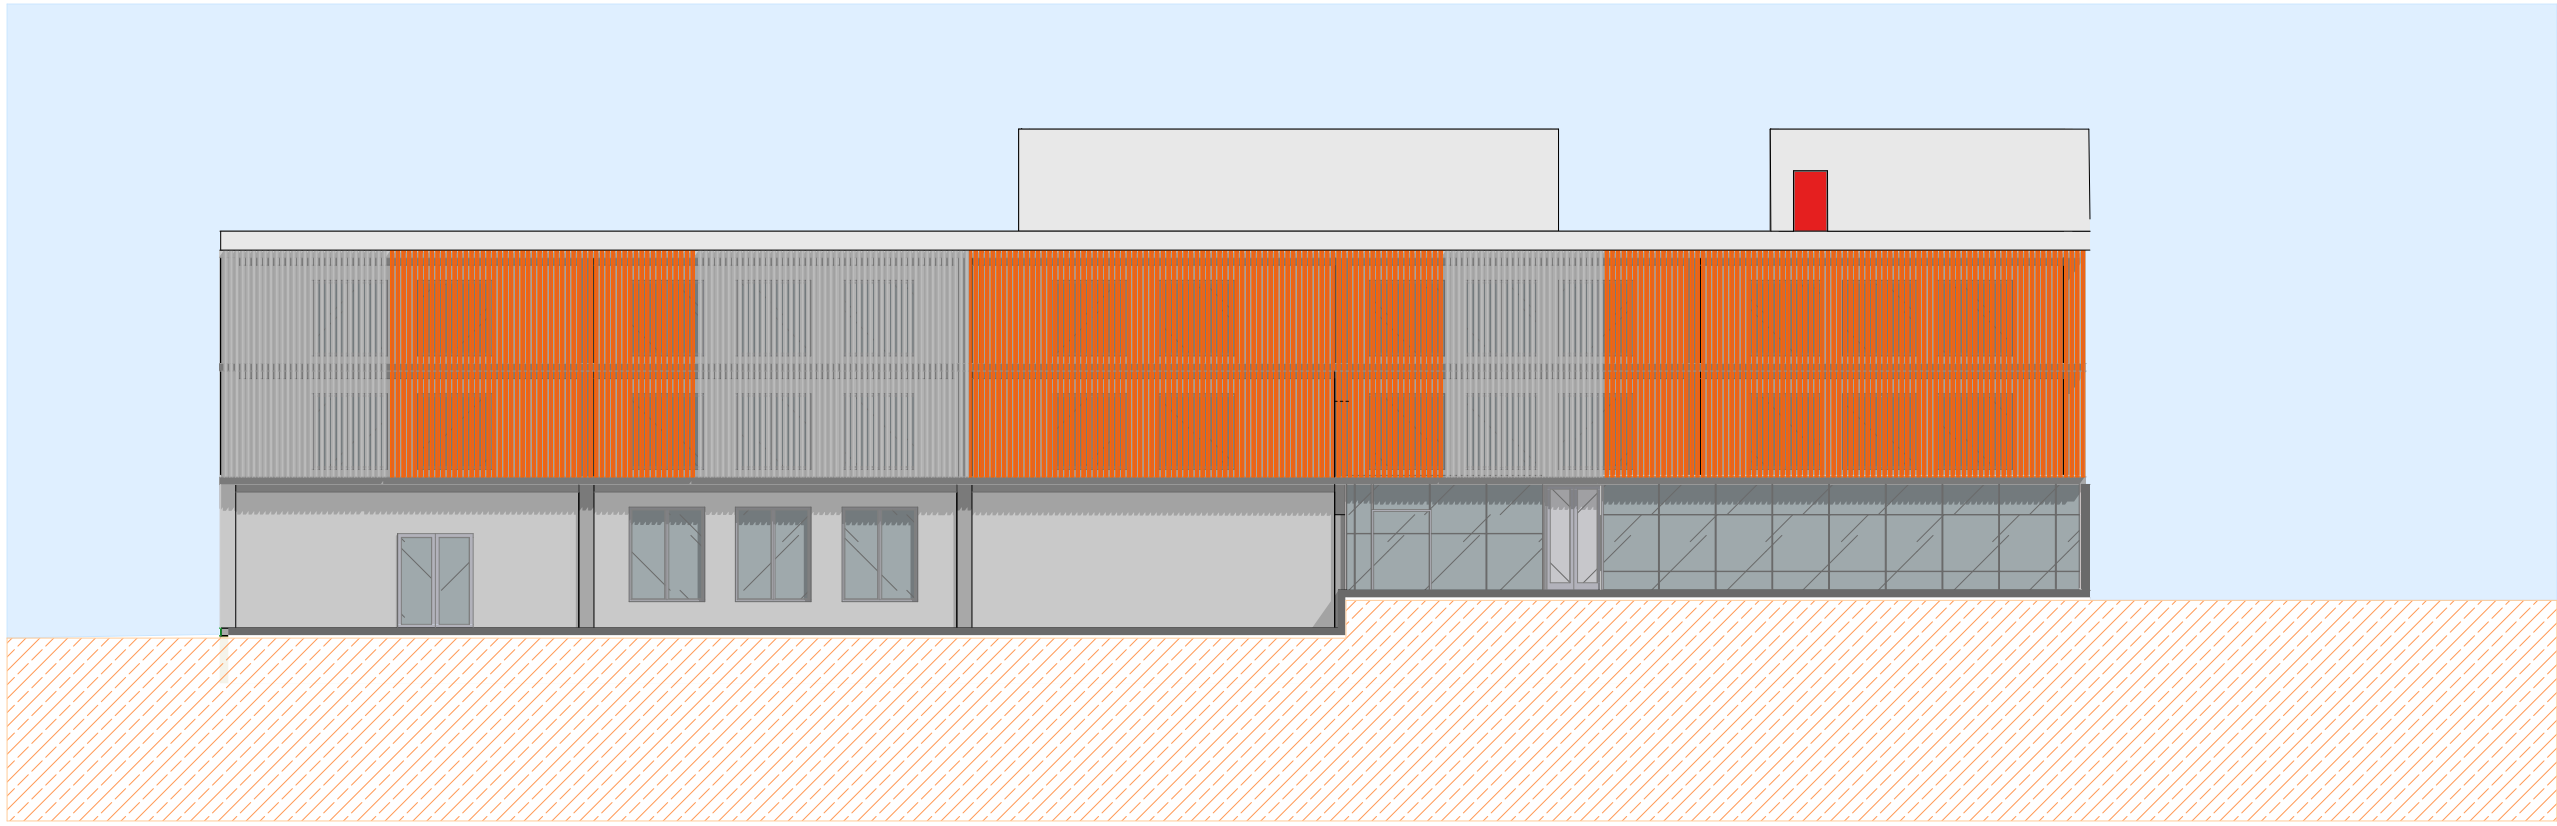

4 ELEVÇÃO 04
1:200

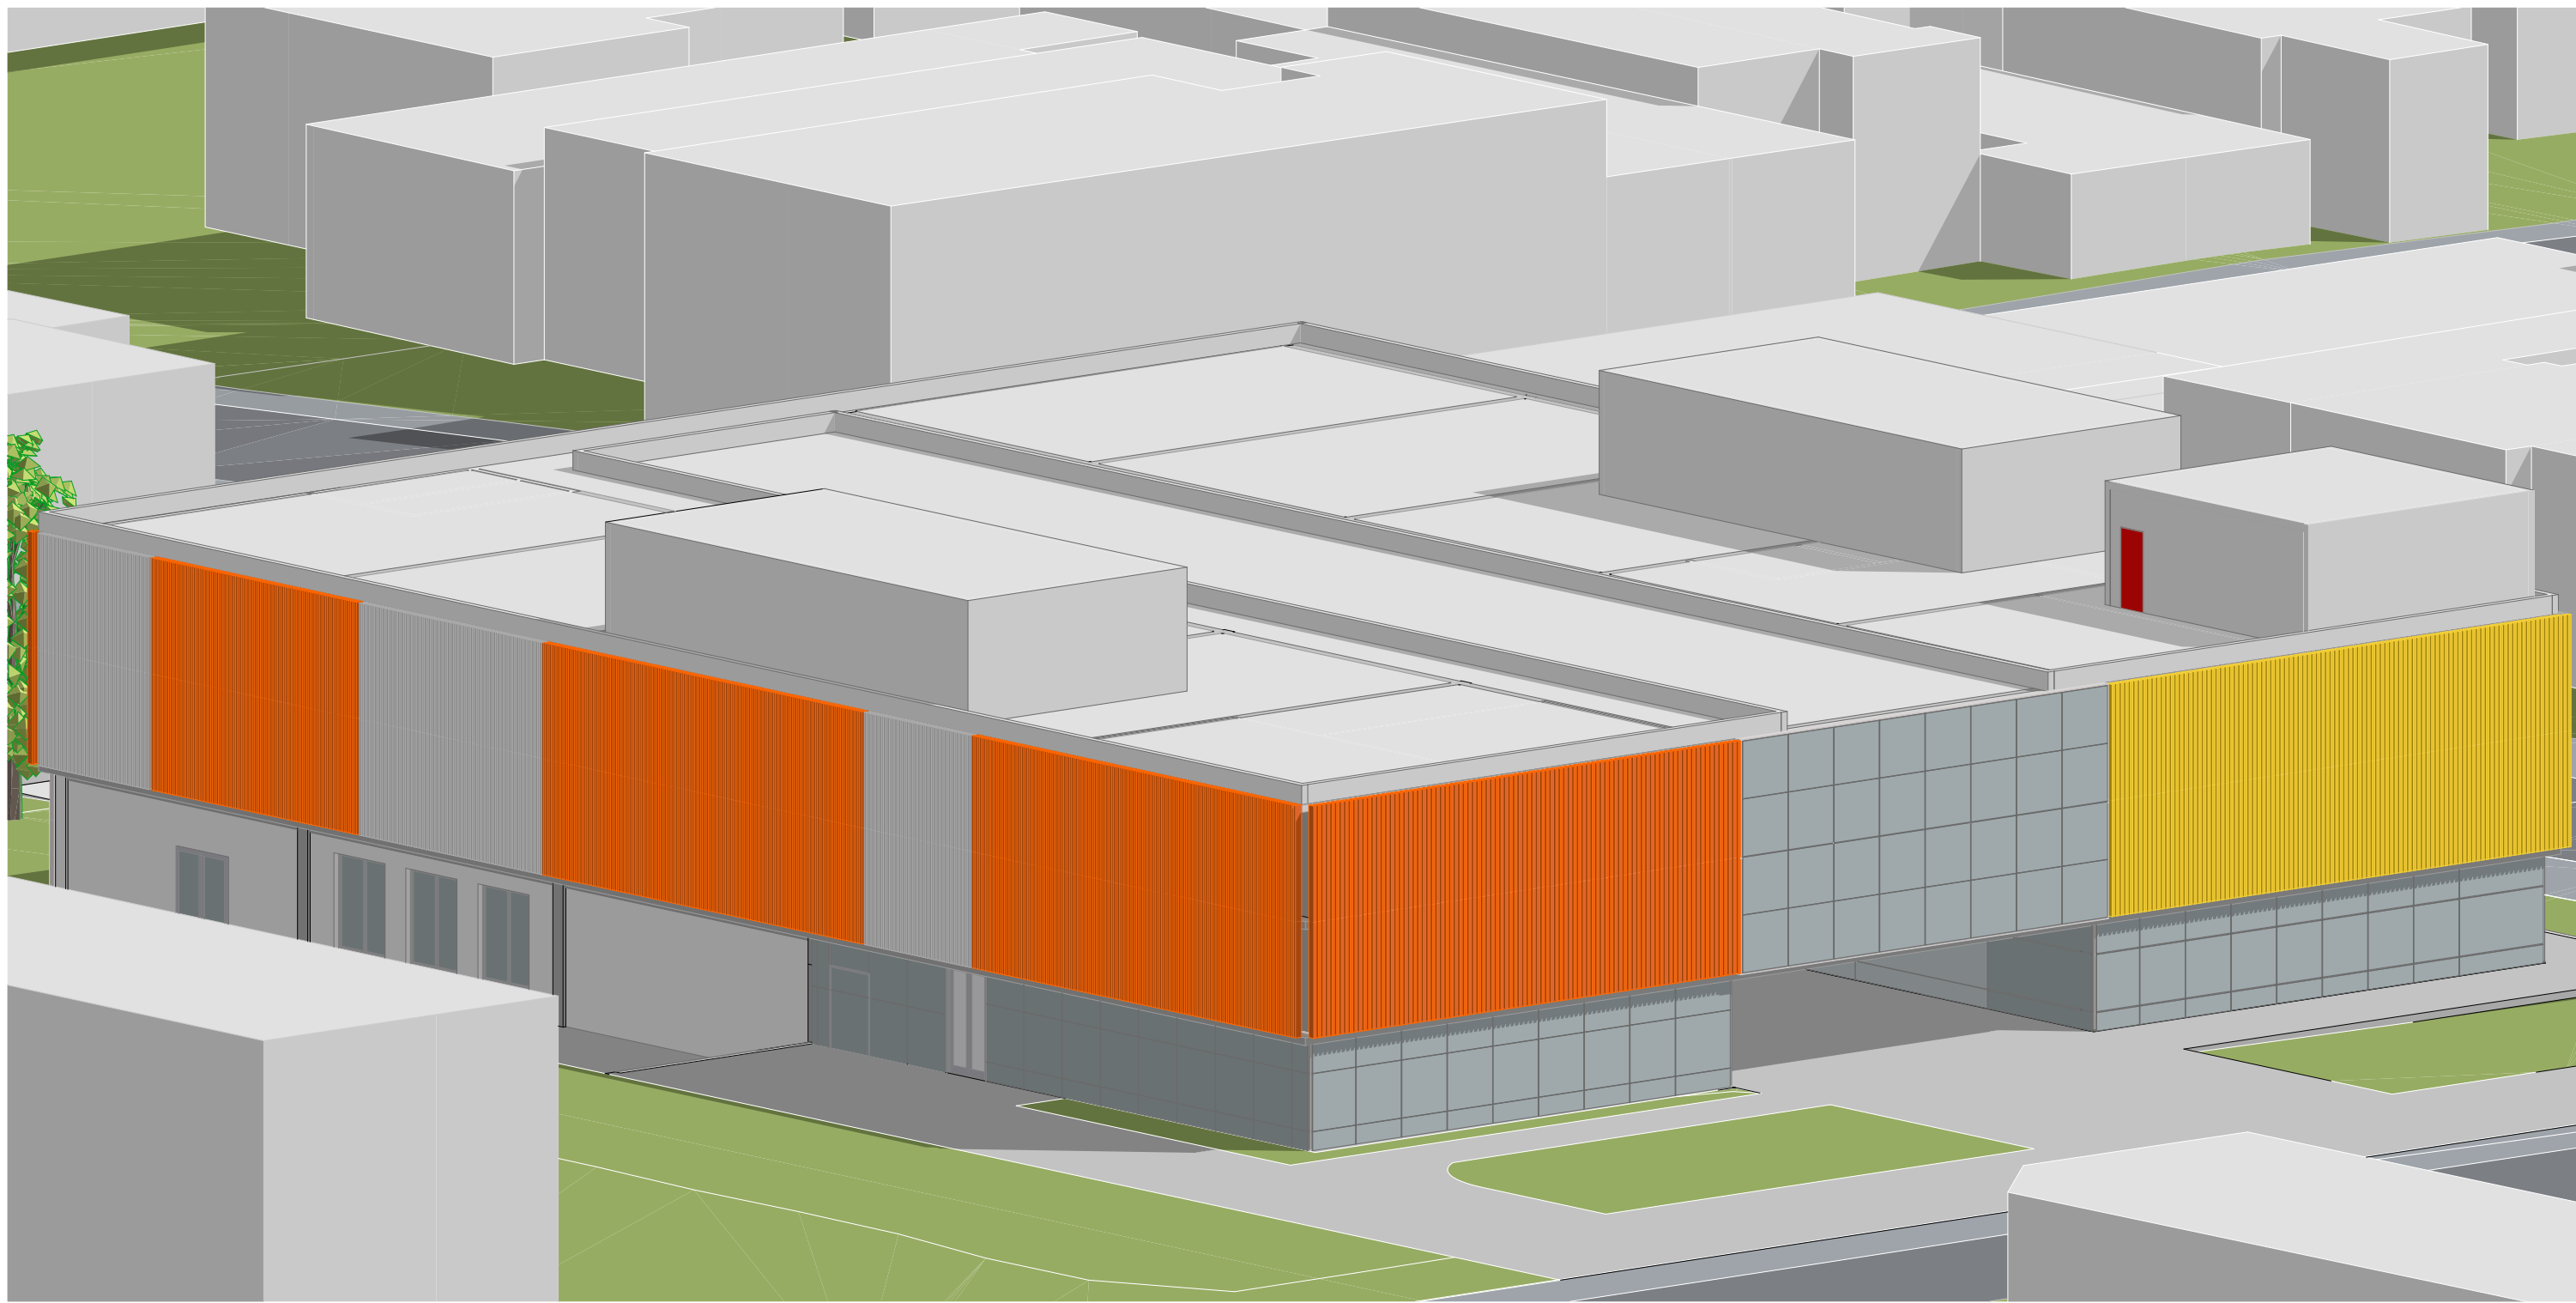

05 ISOMETRIA 01
1:200

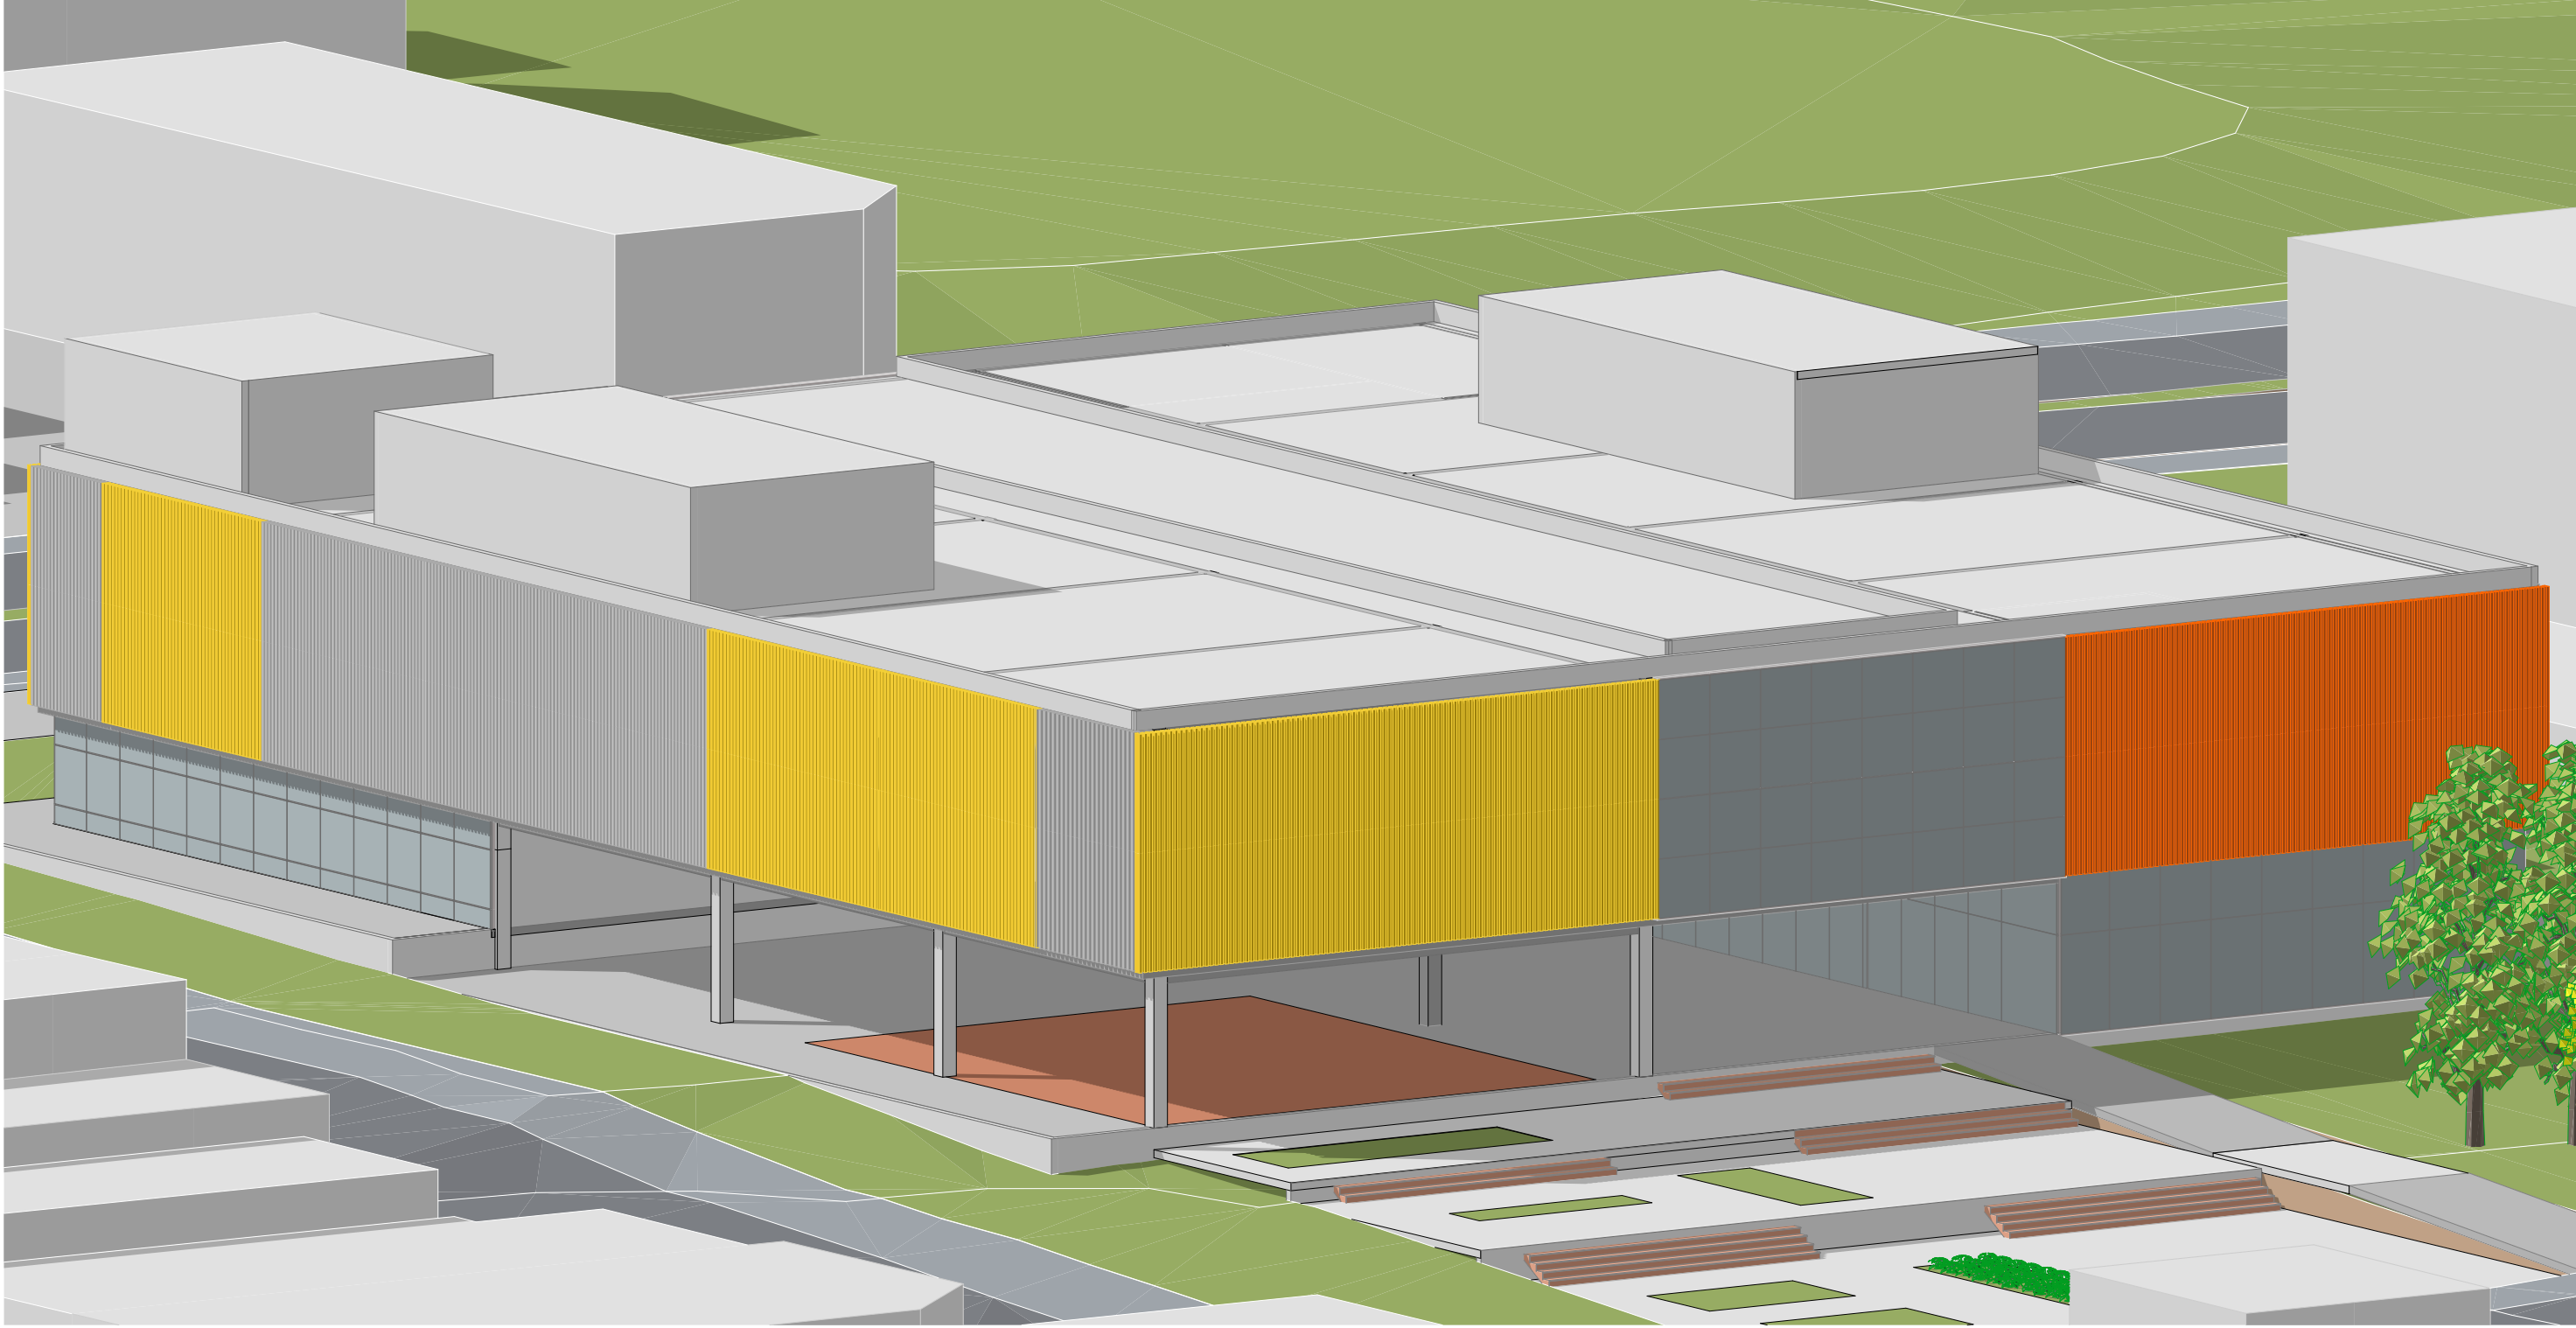

06 ISOMETRIA 02
1:200