

QUADRO DE ÁREAS

ÁREA DO TERRENO	3.019 M²
C.A MÁXIMO	12.076 M²
C.A DO PROJETO	12.137 M²
T.O (LEI)	2.113 M²
T.O (PROJETO)	865,95 M²
T.P (LOJAS / GALERIA)	
T.P (ESCRITÓRIOS)	

DEMONSTRATIVO DE RECUOS


42 - 6 / 10 = 3,60 M


CALCULO DA POPULAÇÃO

ÁREA LOJAS / GALERIAS	866,95 M² / 3	289 PESSOAS
ESCRITÓRIOS POR ANDAR	866,95 M² / 7	124 PESSOAS
TOTAL DE 14 ANDARES	10.403,40 / 7	1.487 PESSOAS


CALCULO ESCADAS E CORREDORES

N= 128/60 = 2,13
N= 2,13*0,55 = 1,17

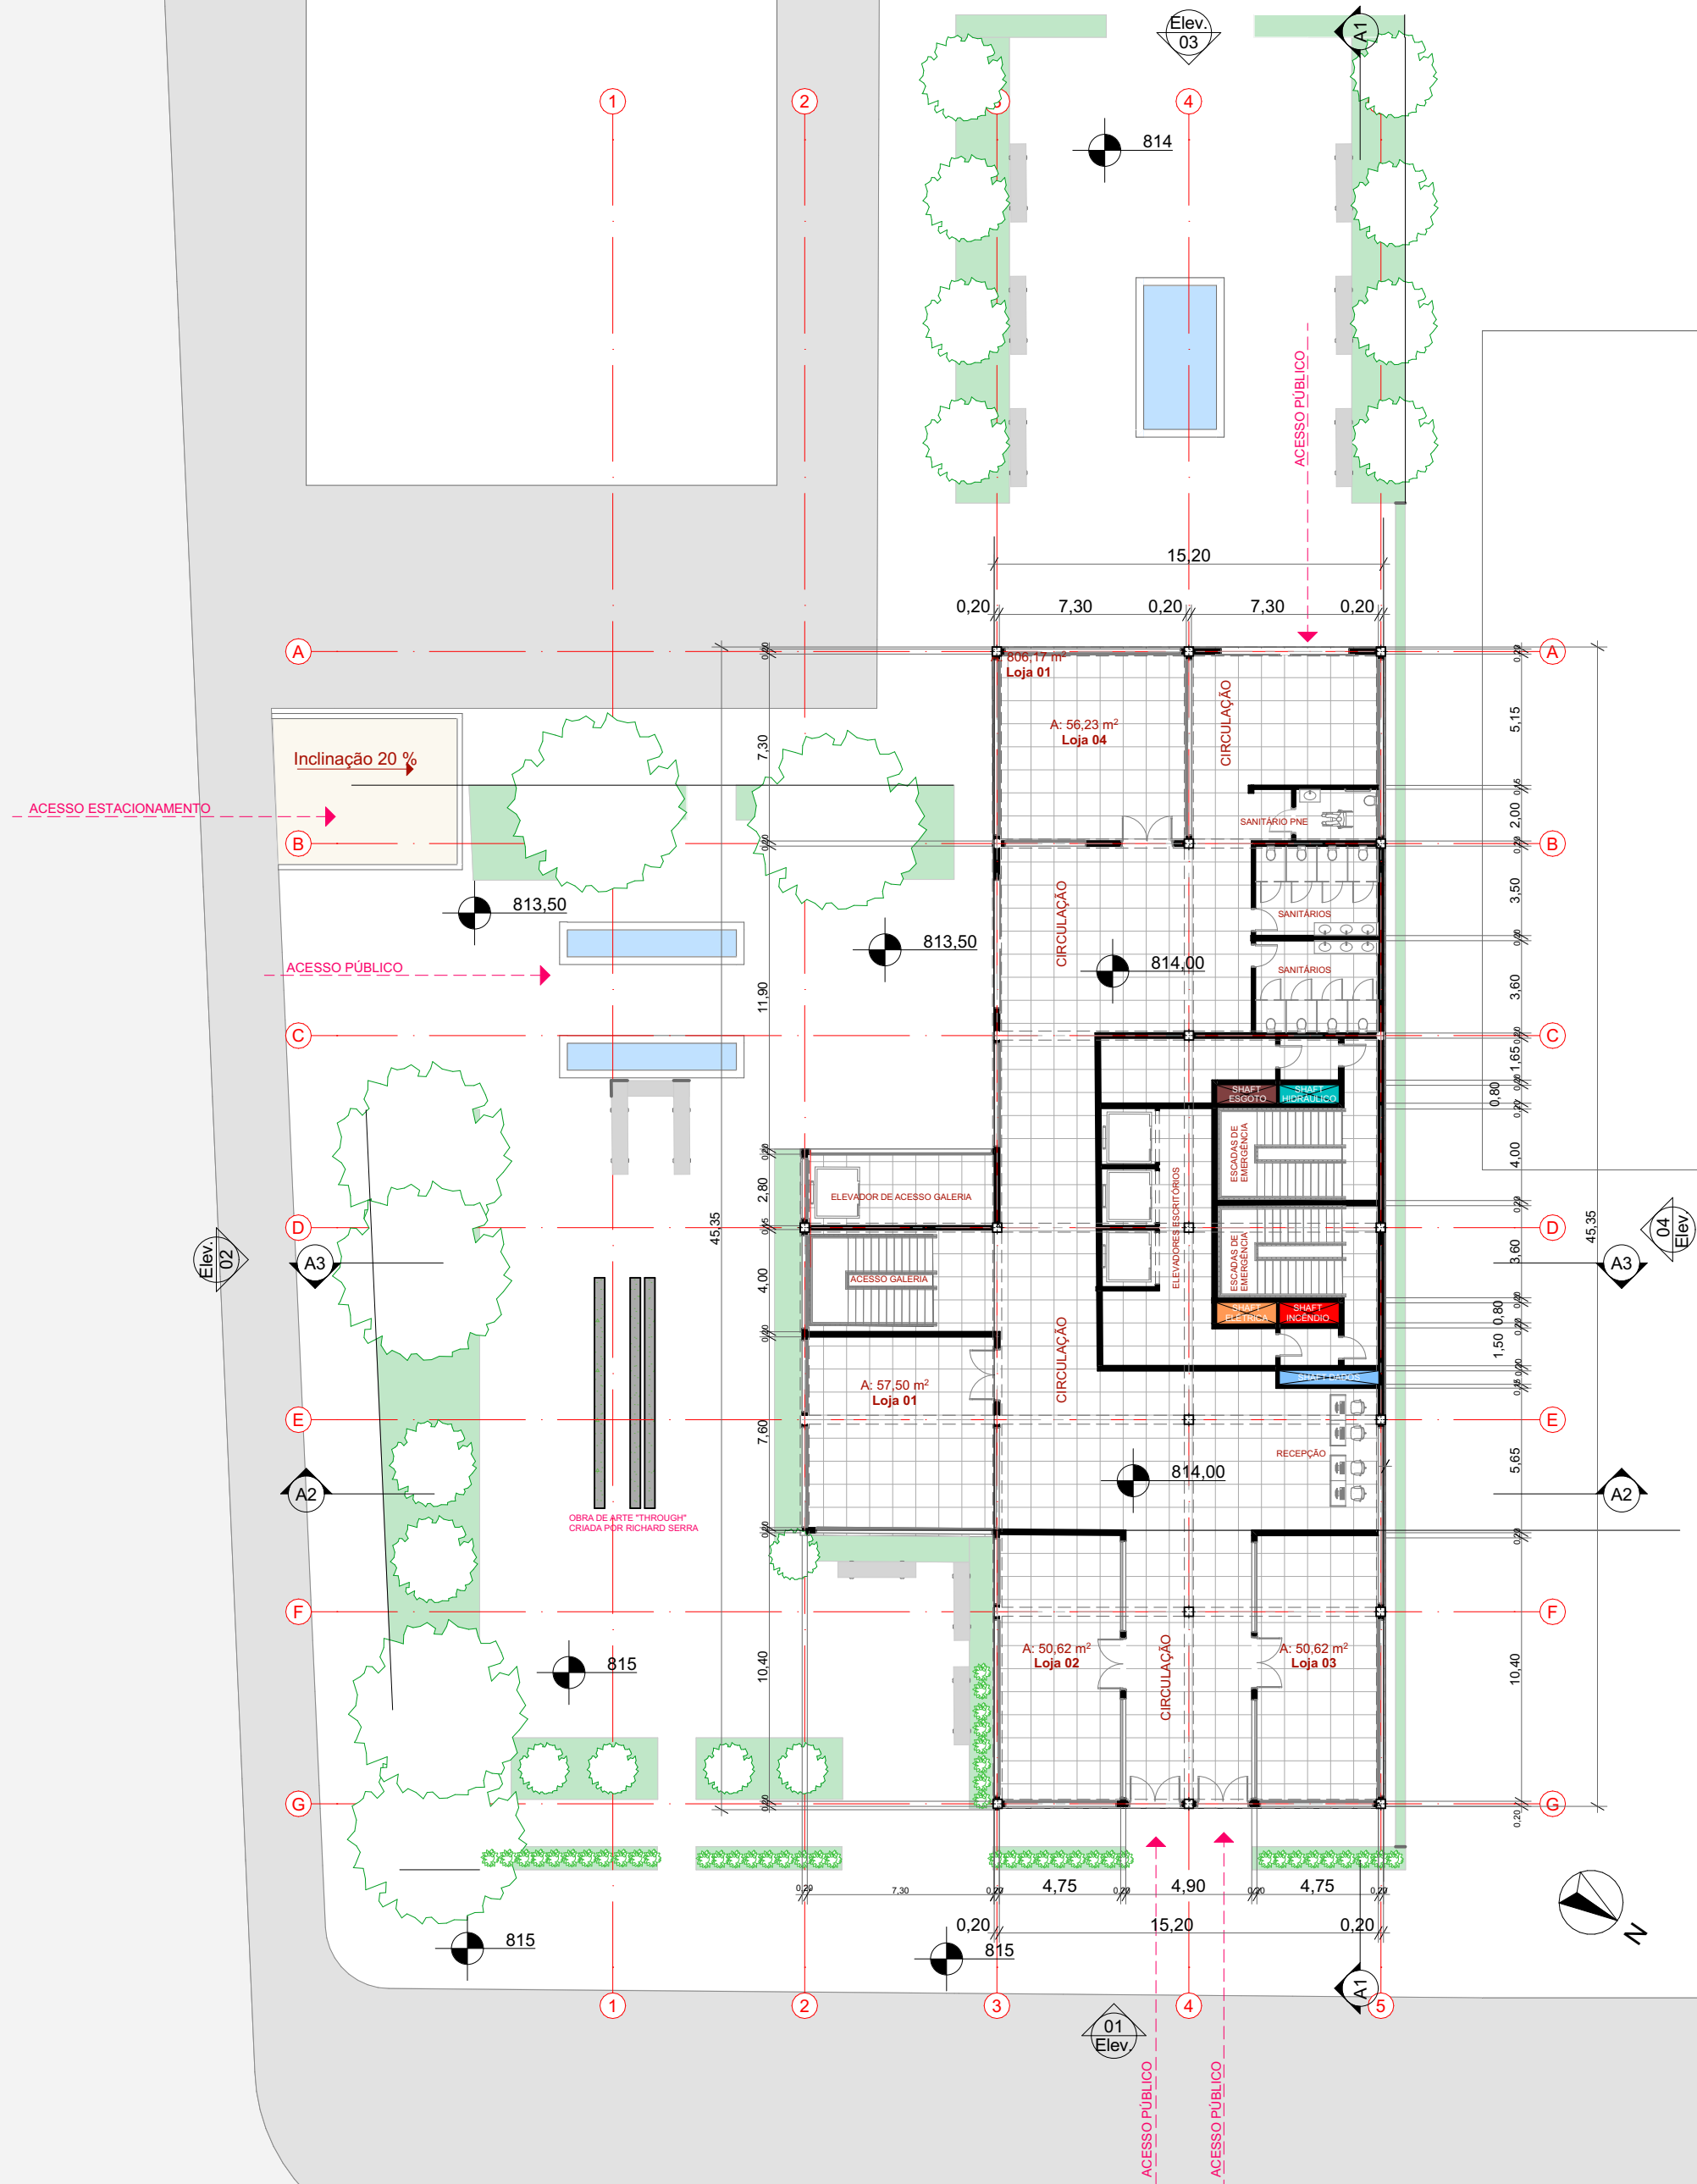


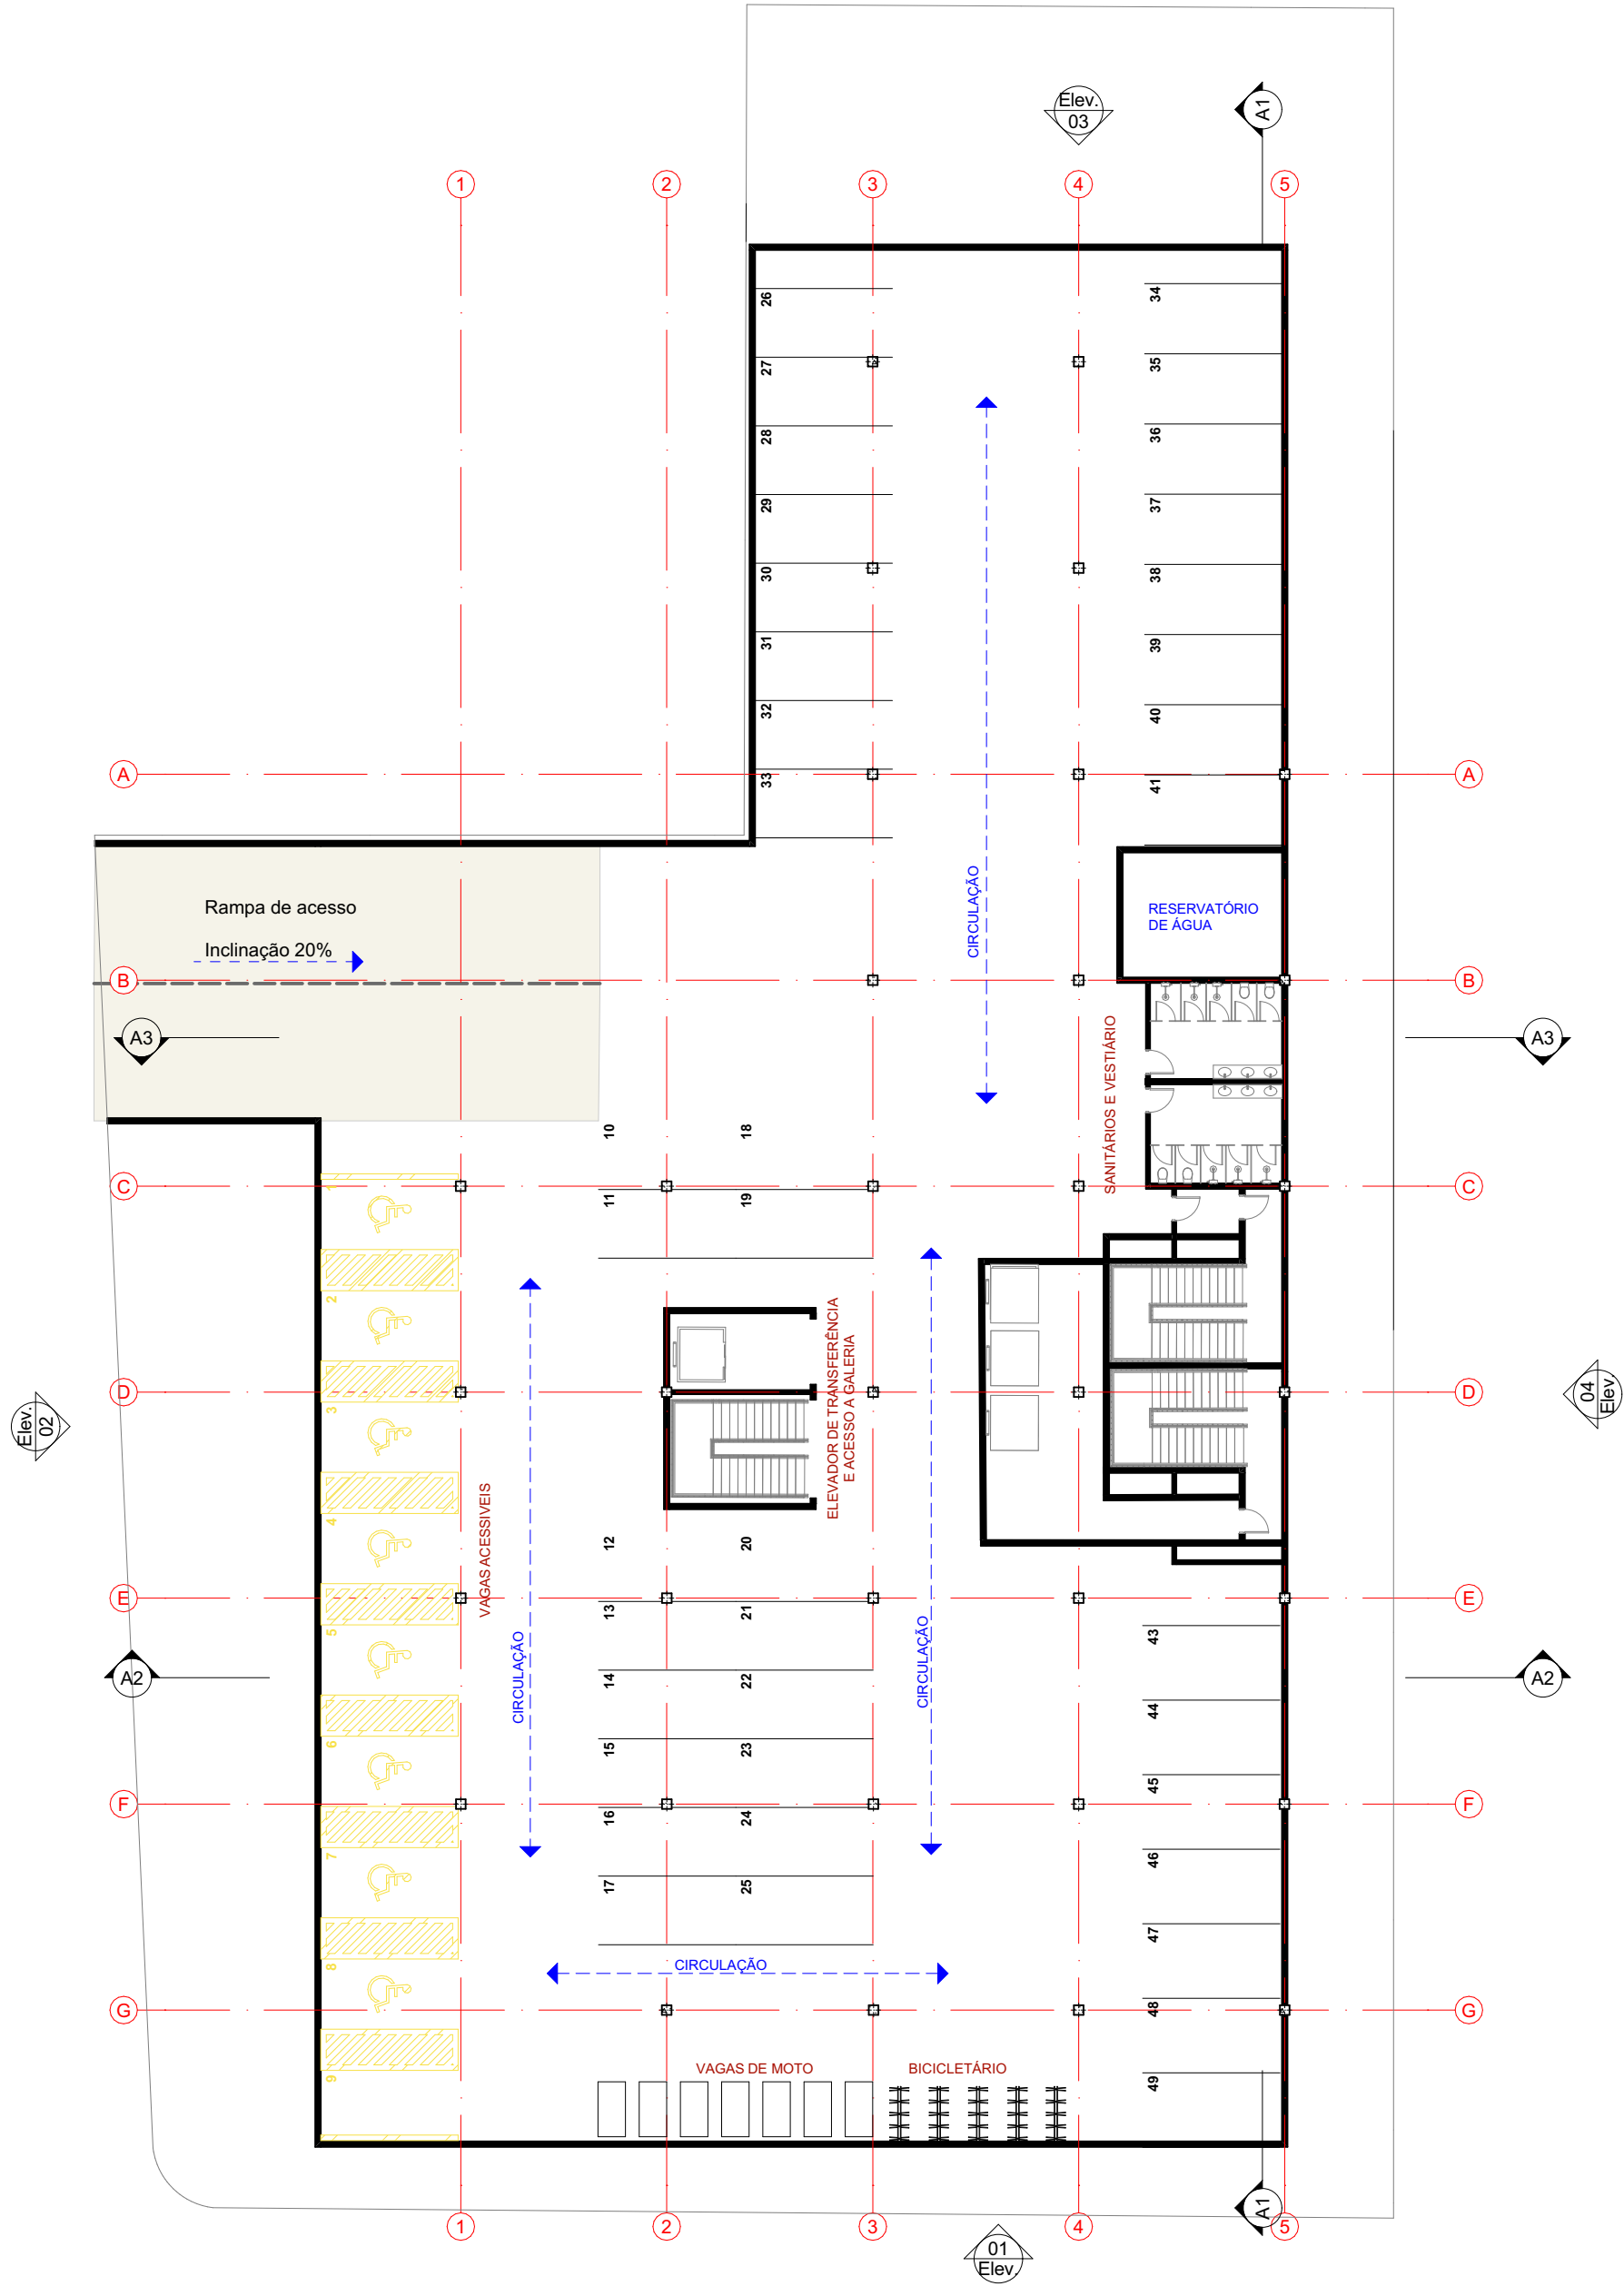

1 PAVIMENTO ESTACIONAMENTO 1:250

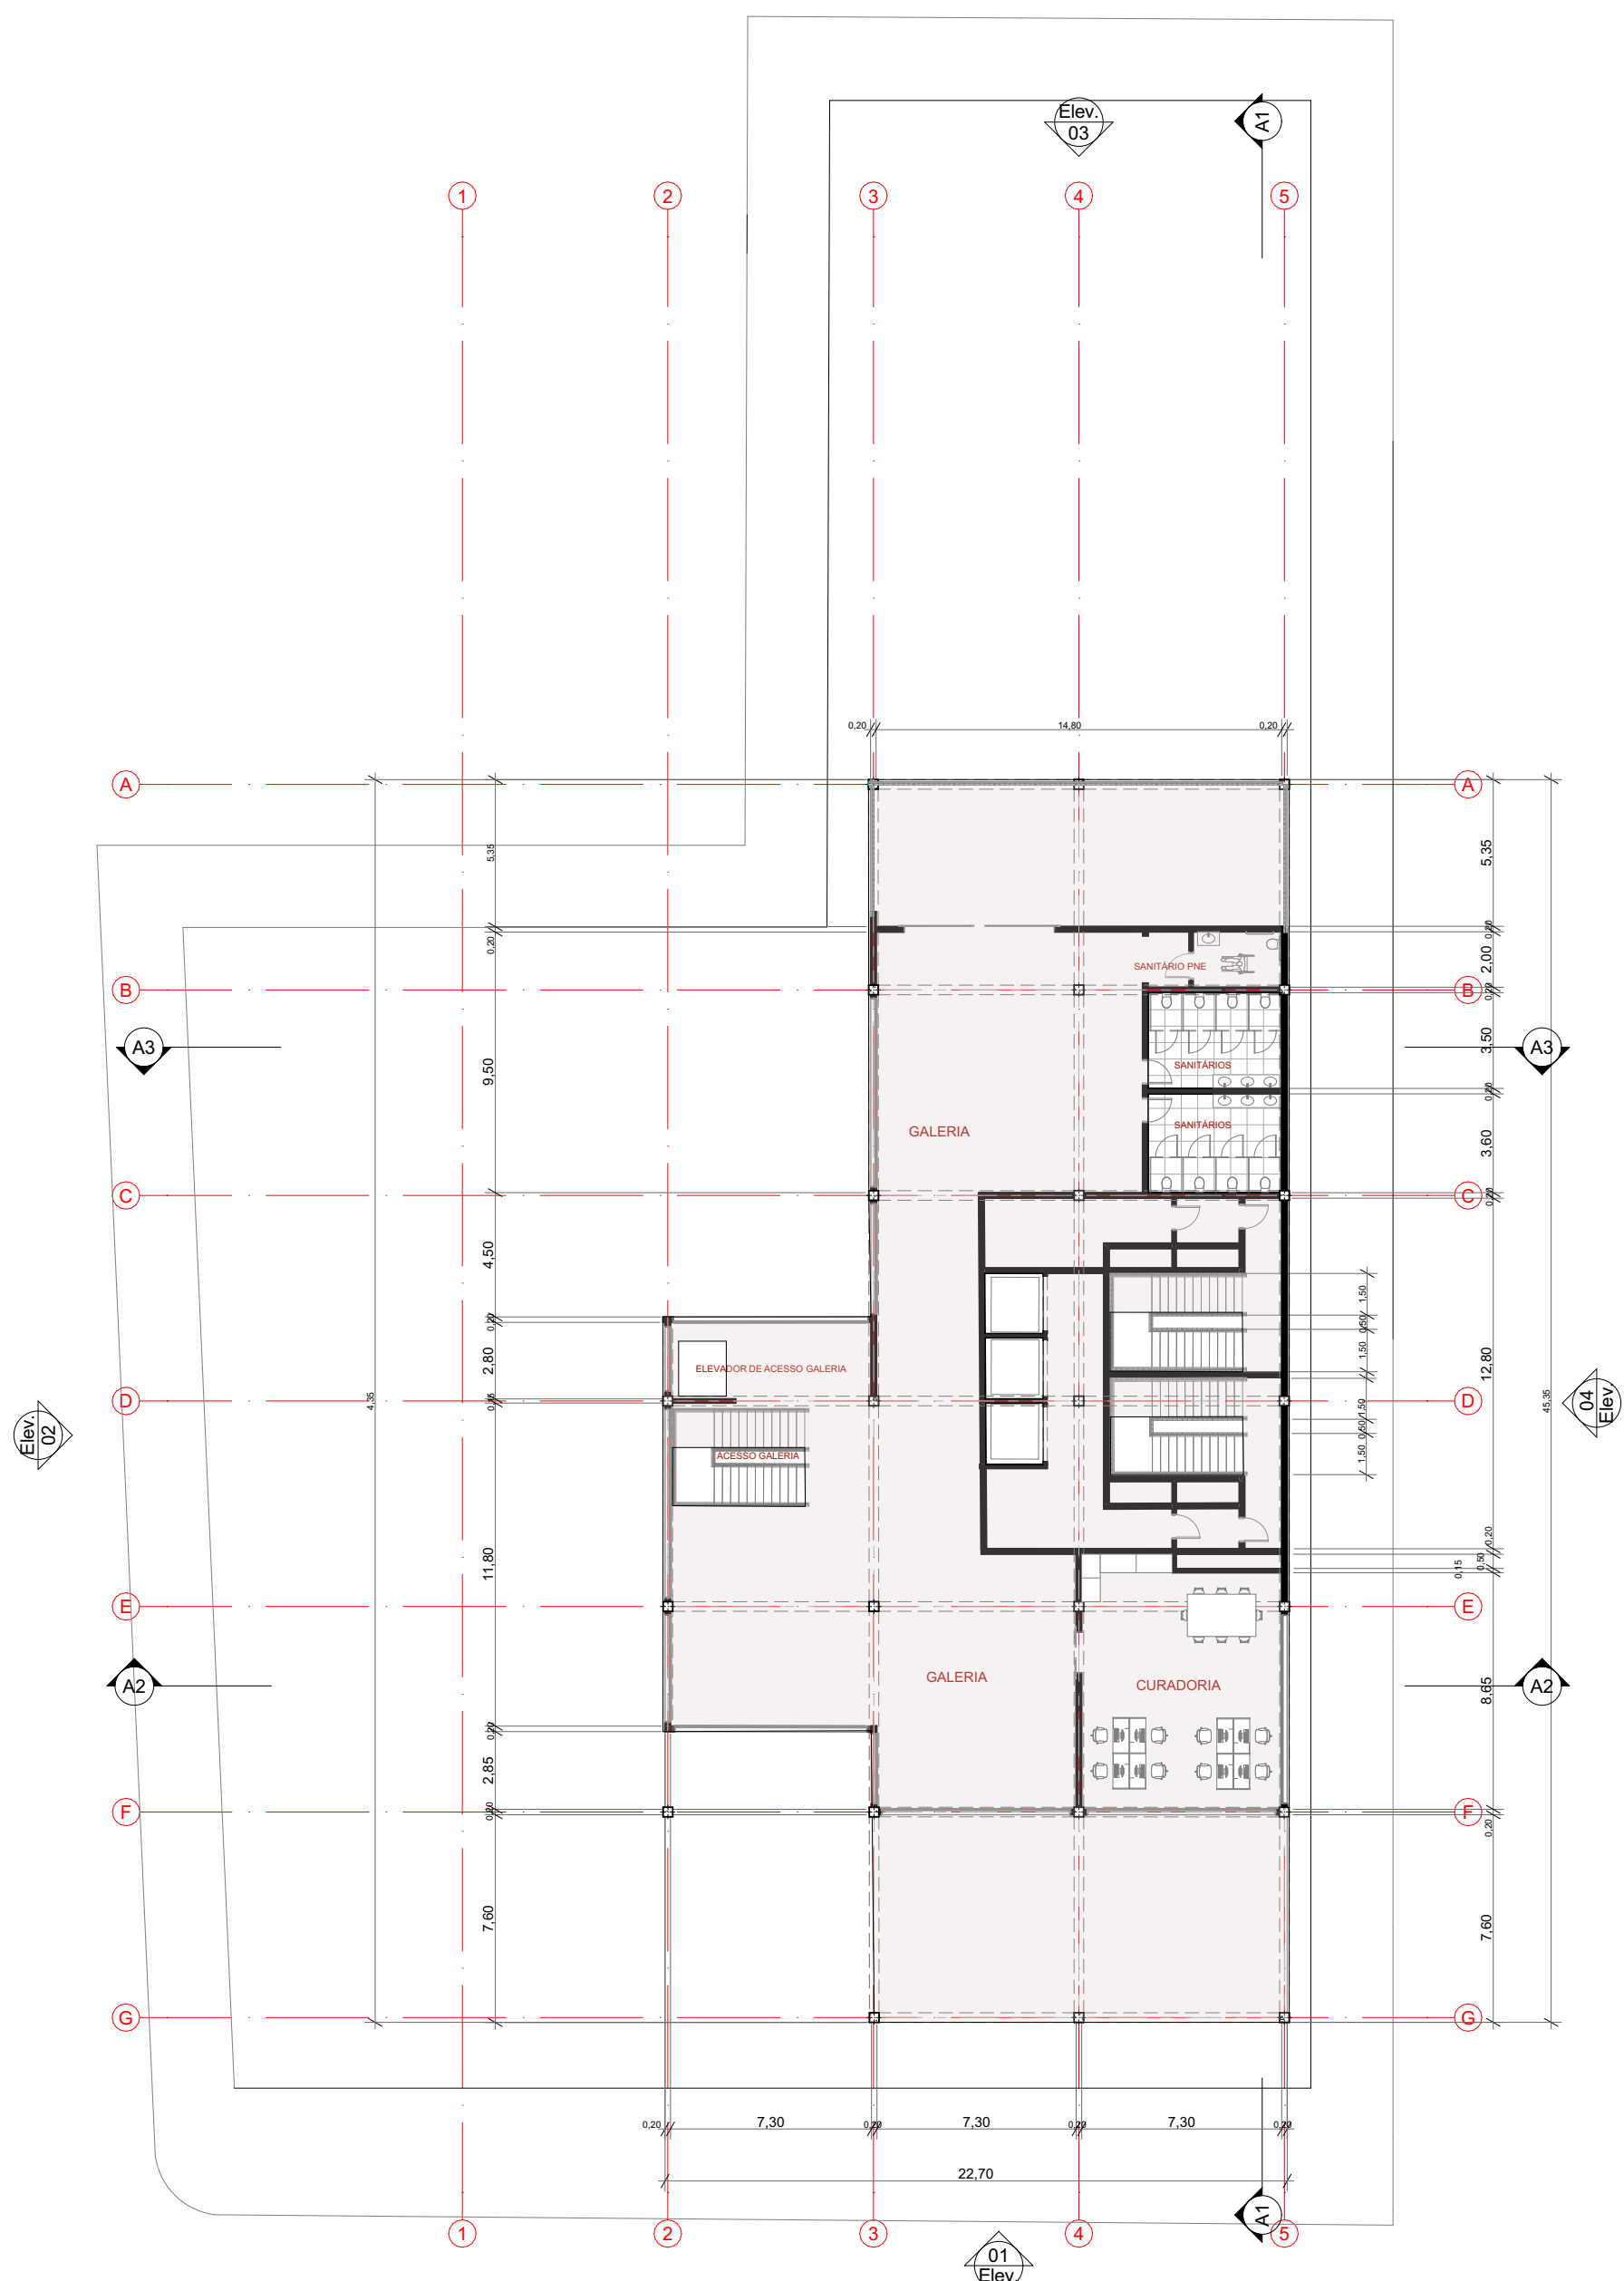


2 PAVIMENTO GALERIA 1:250

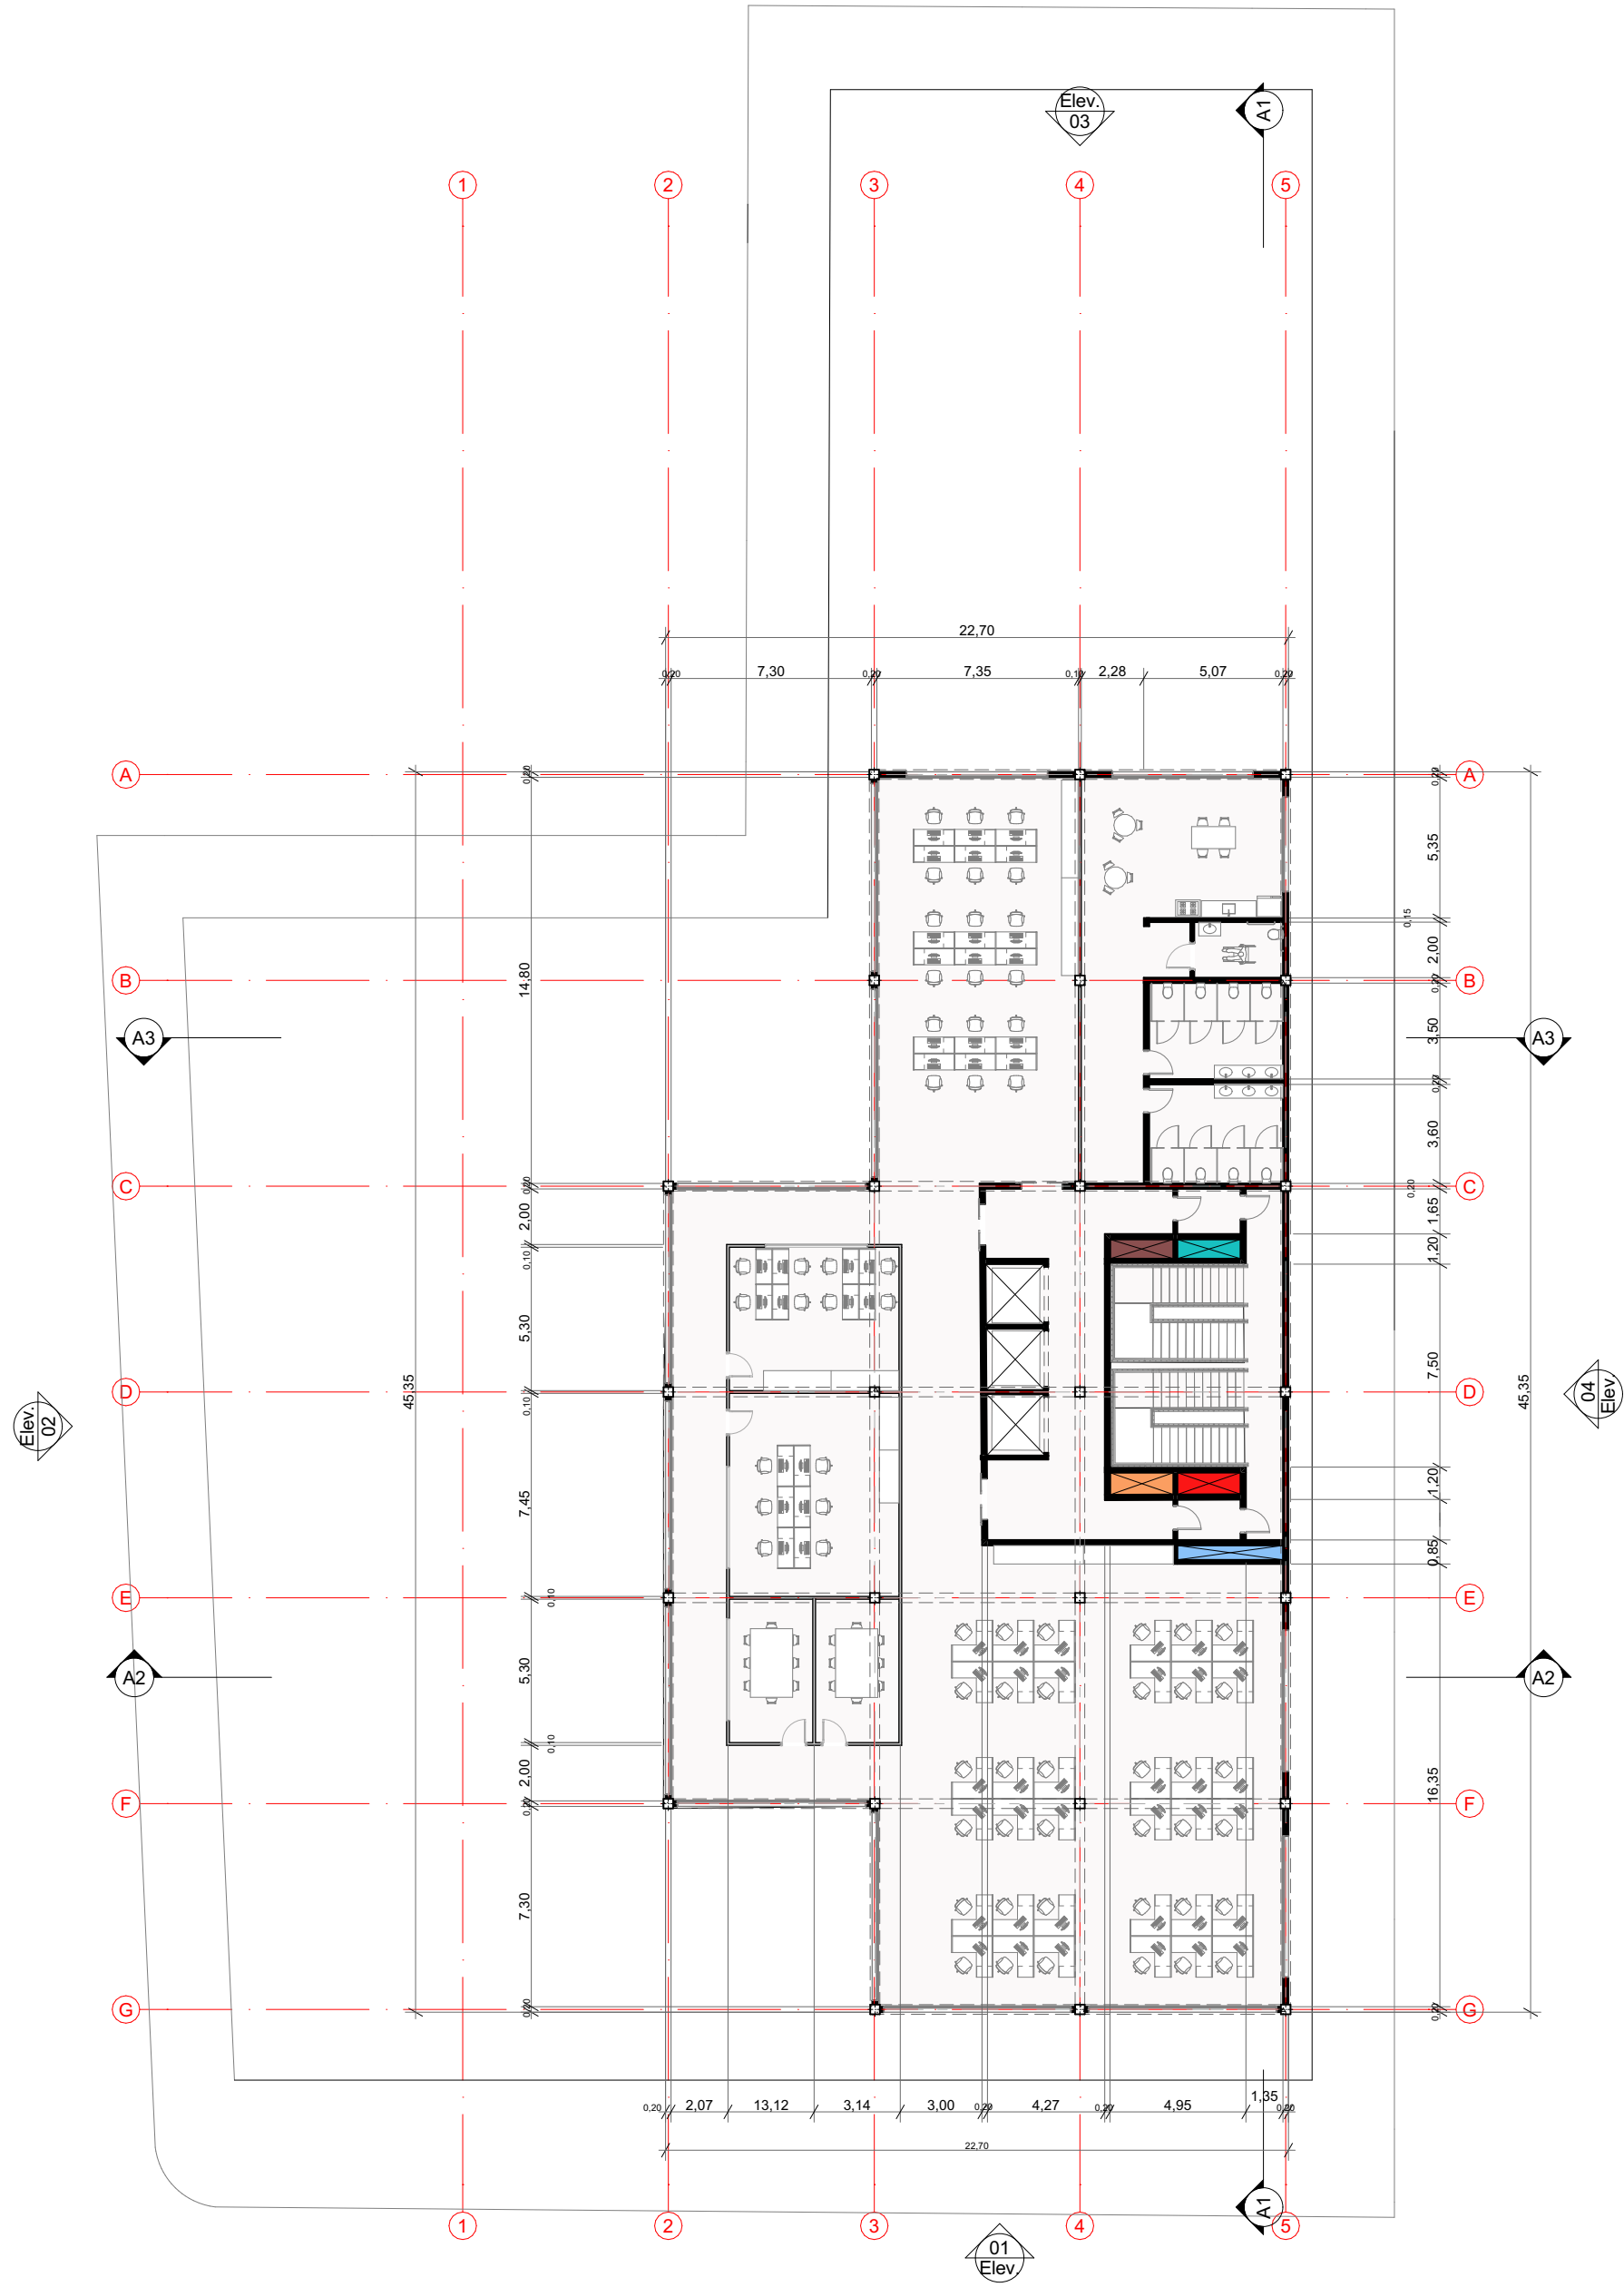


3


PAVIMENTO TIPO 1
1:250

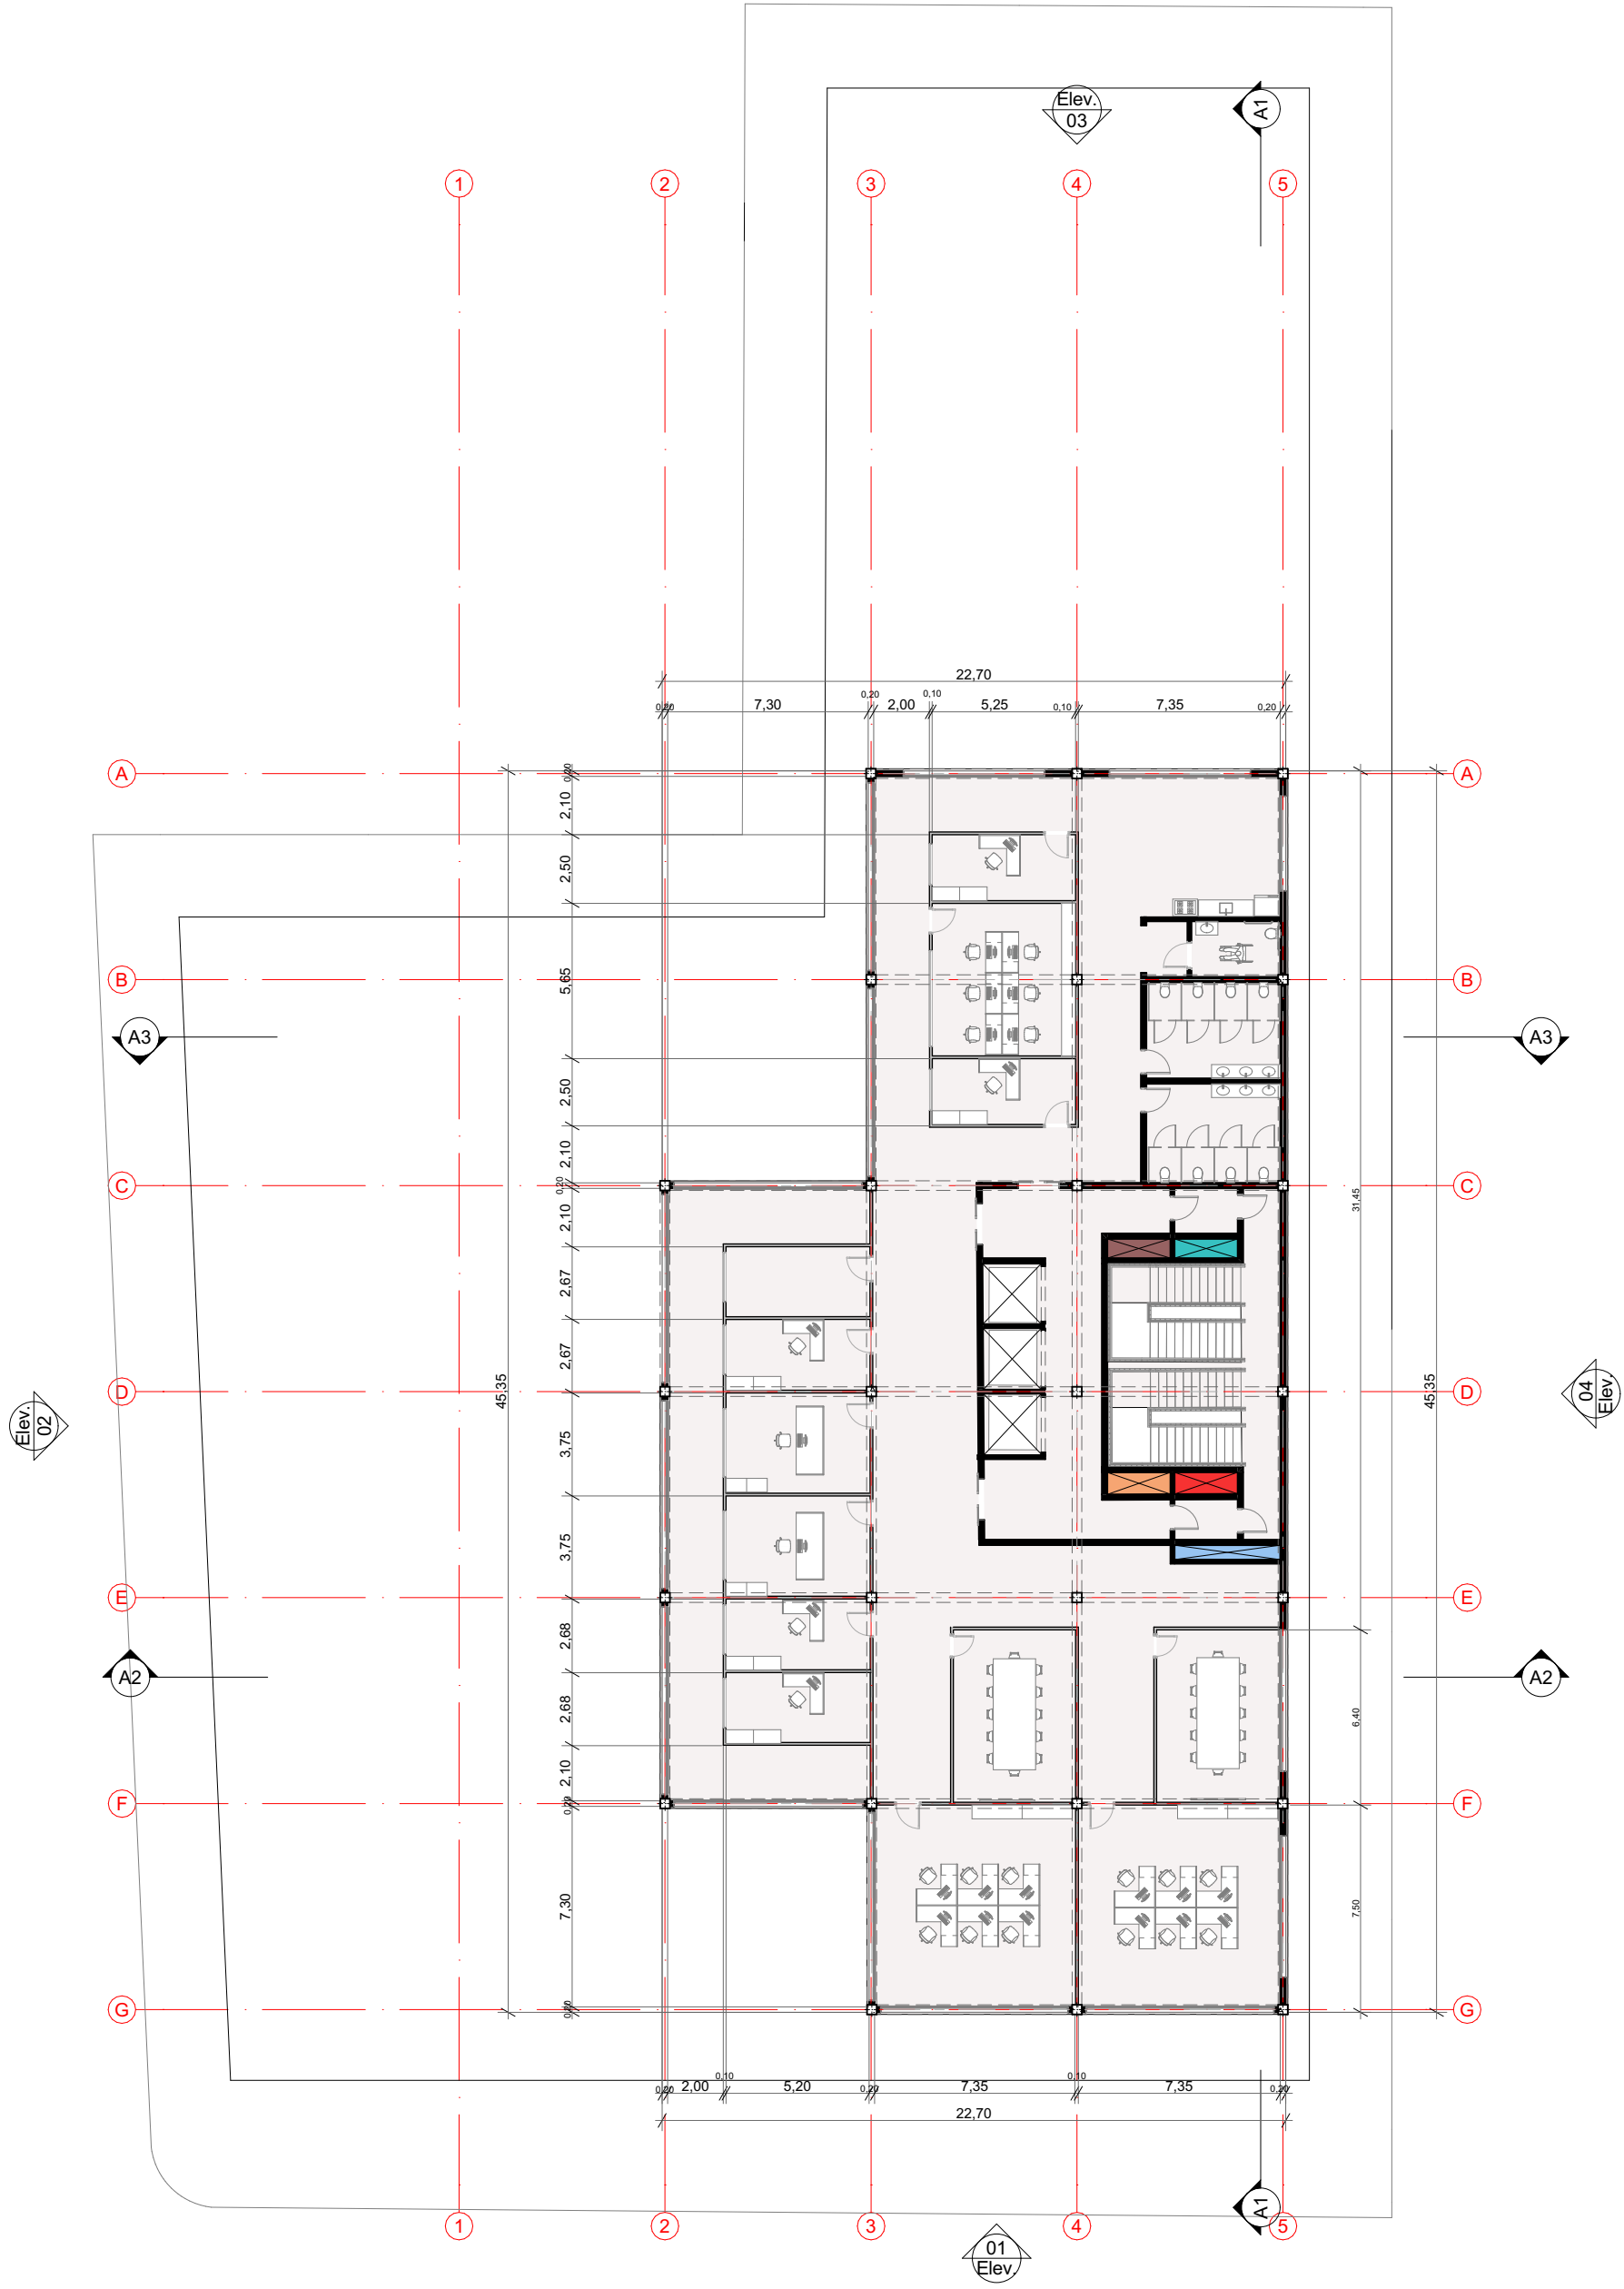


4


PAVIMENTO TIPO 2
1:250

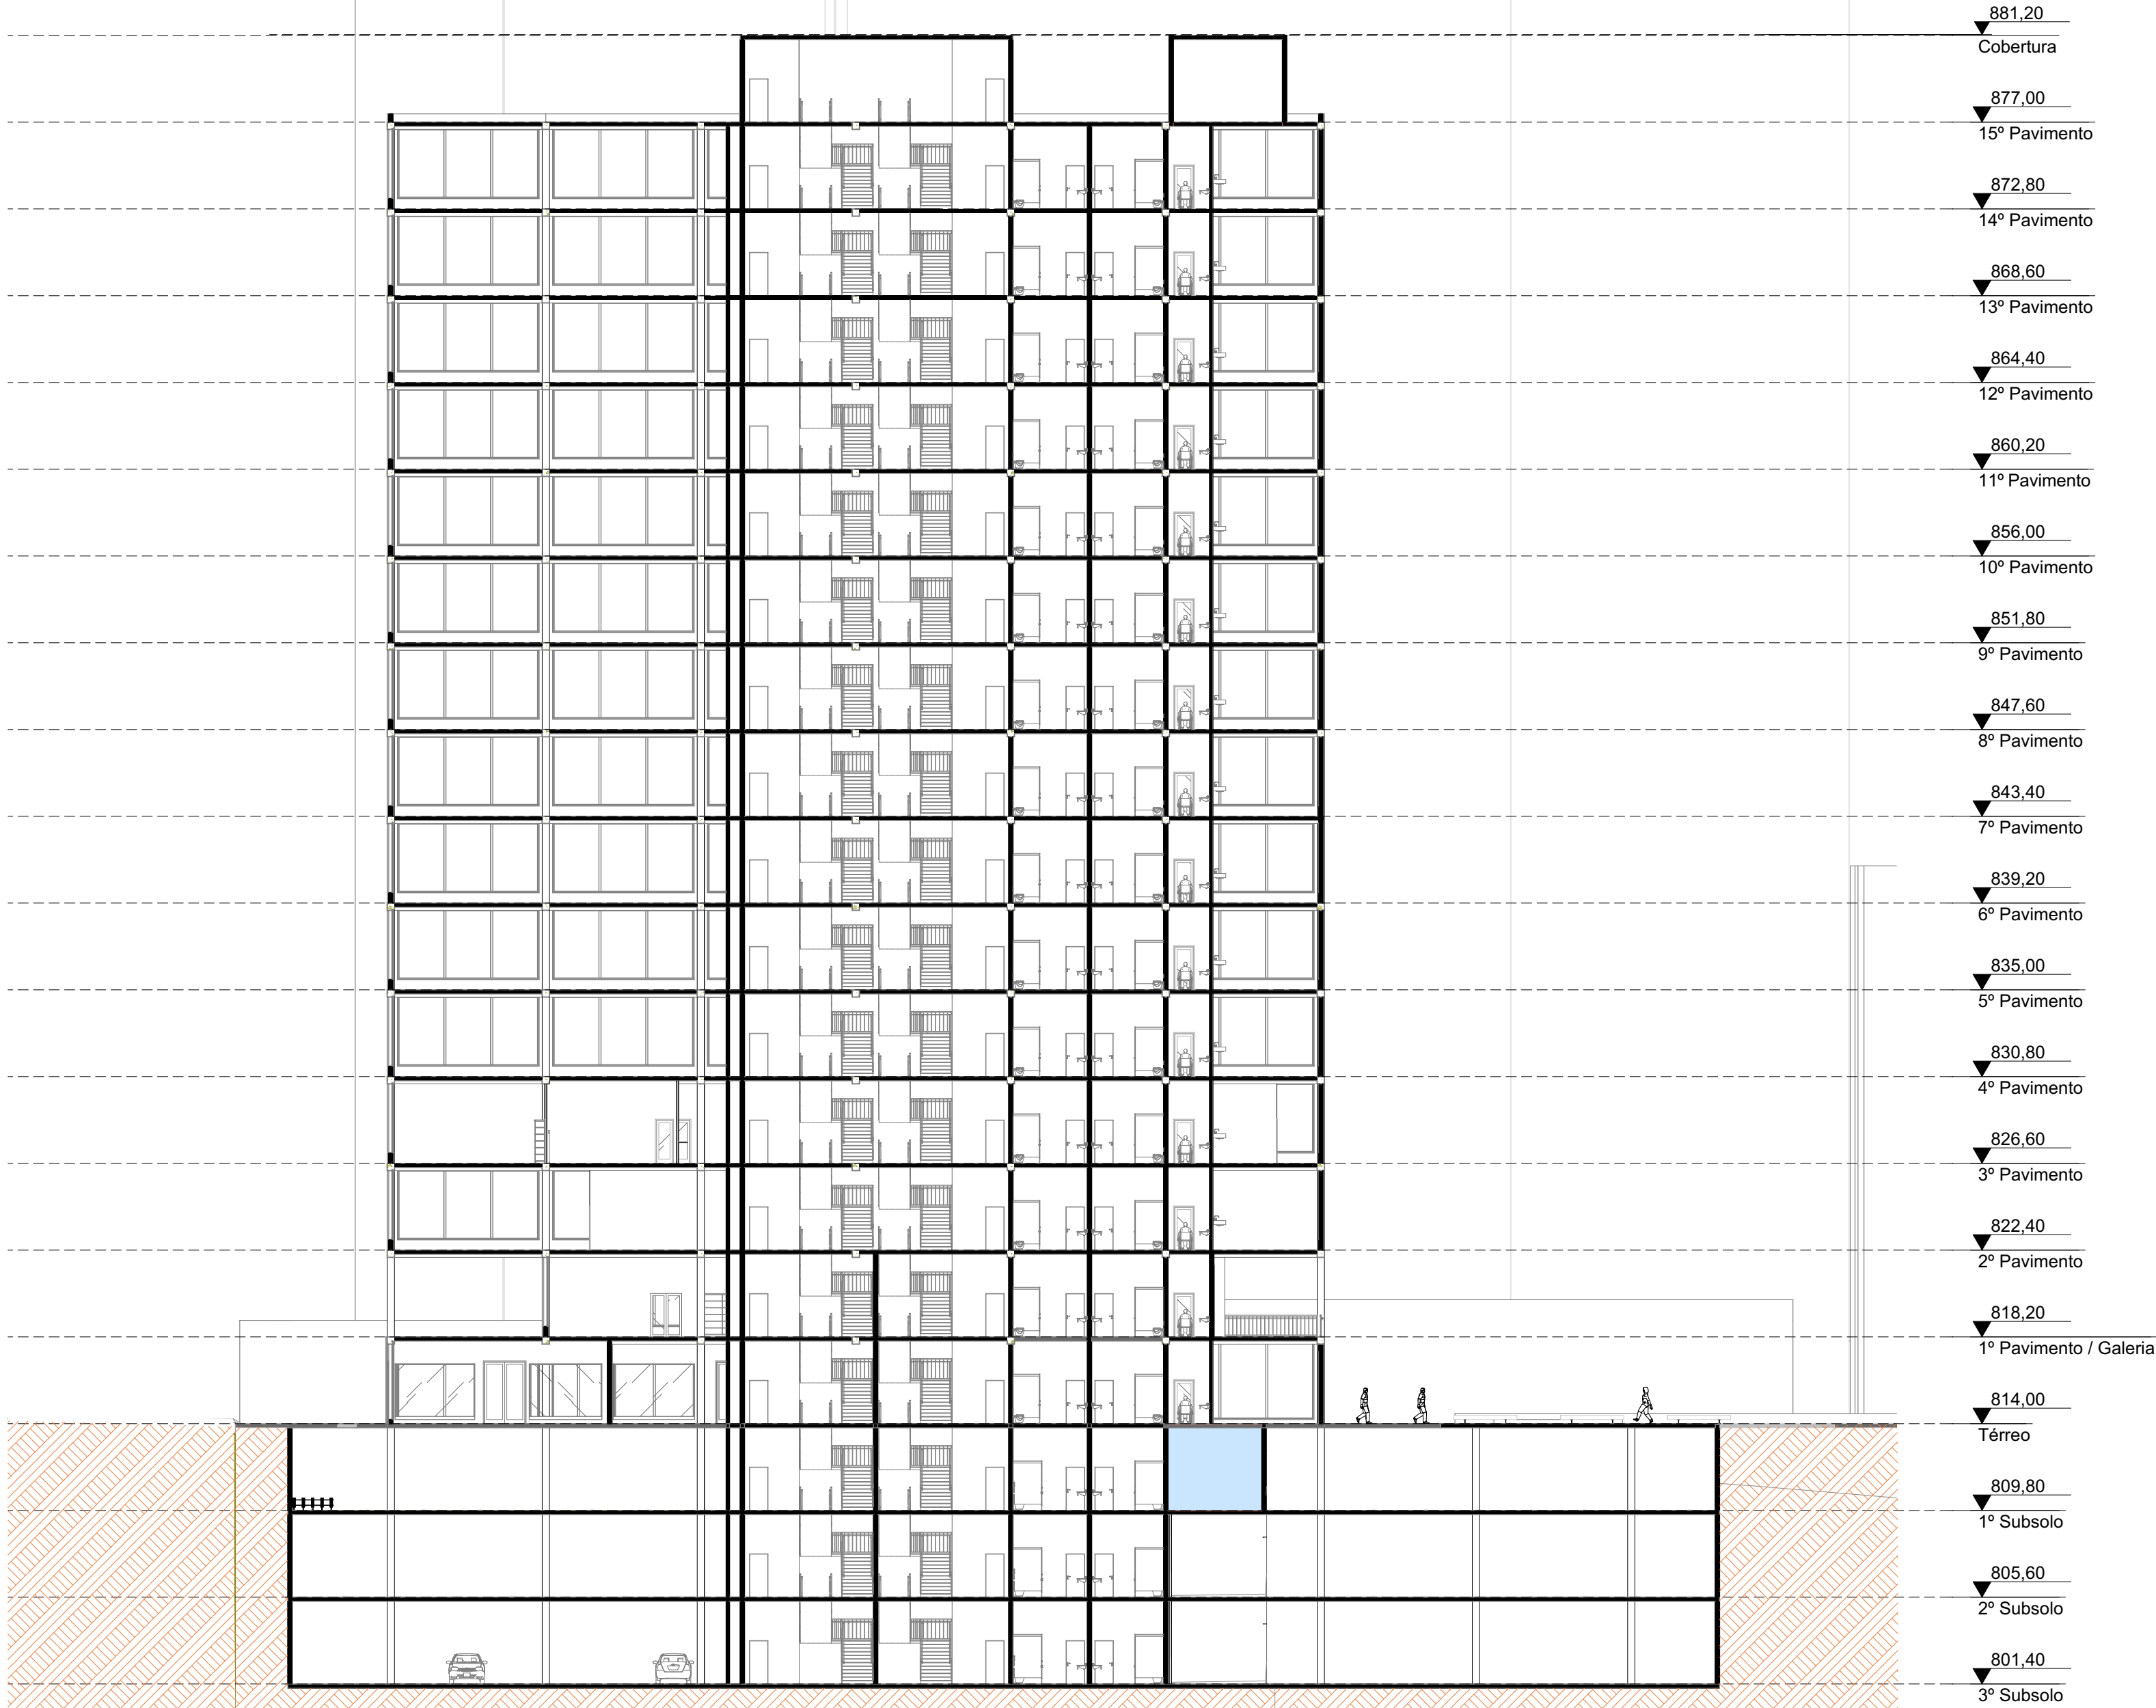

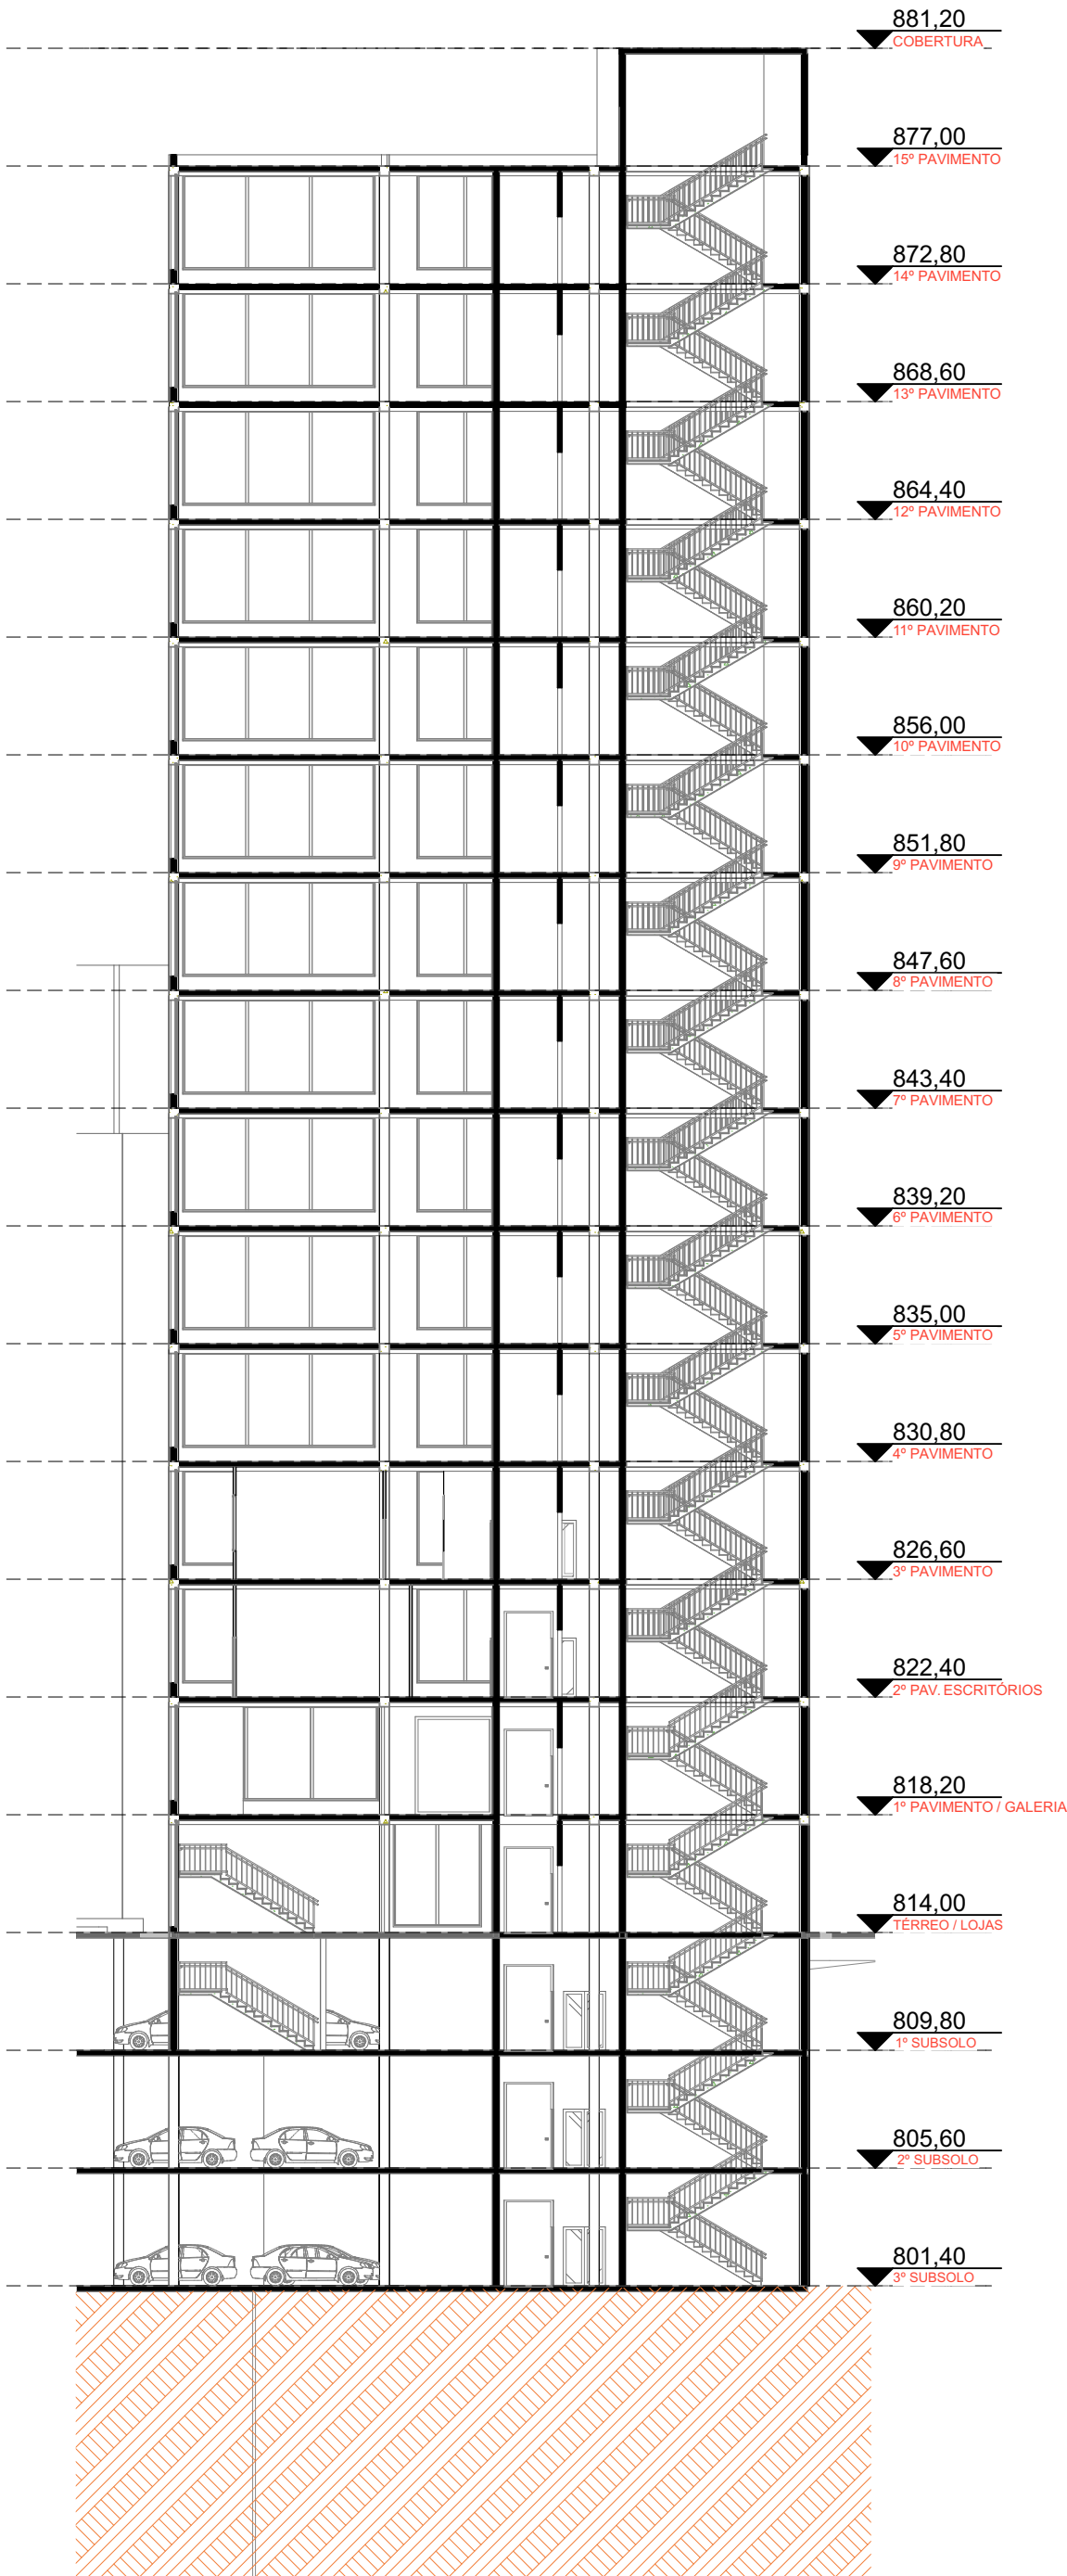

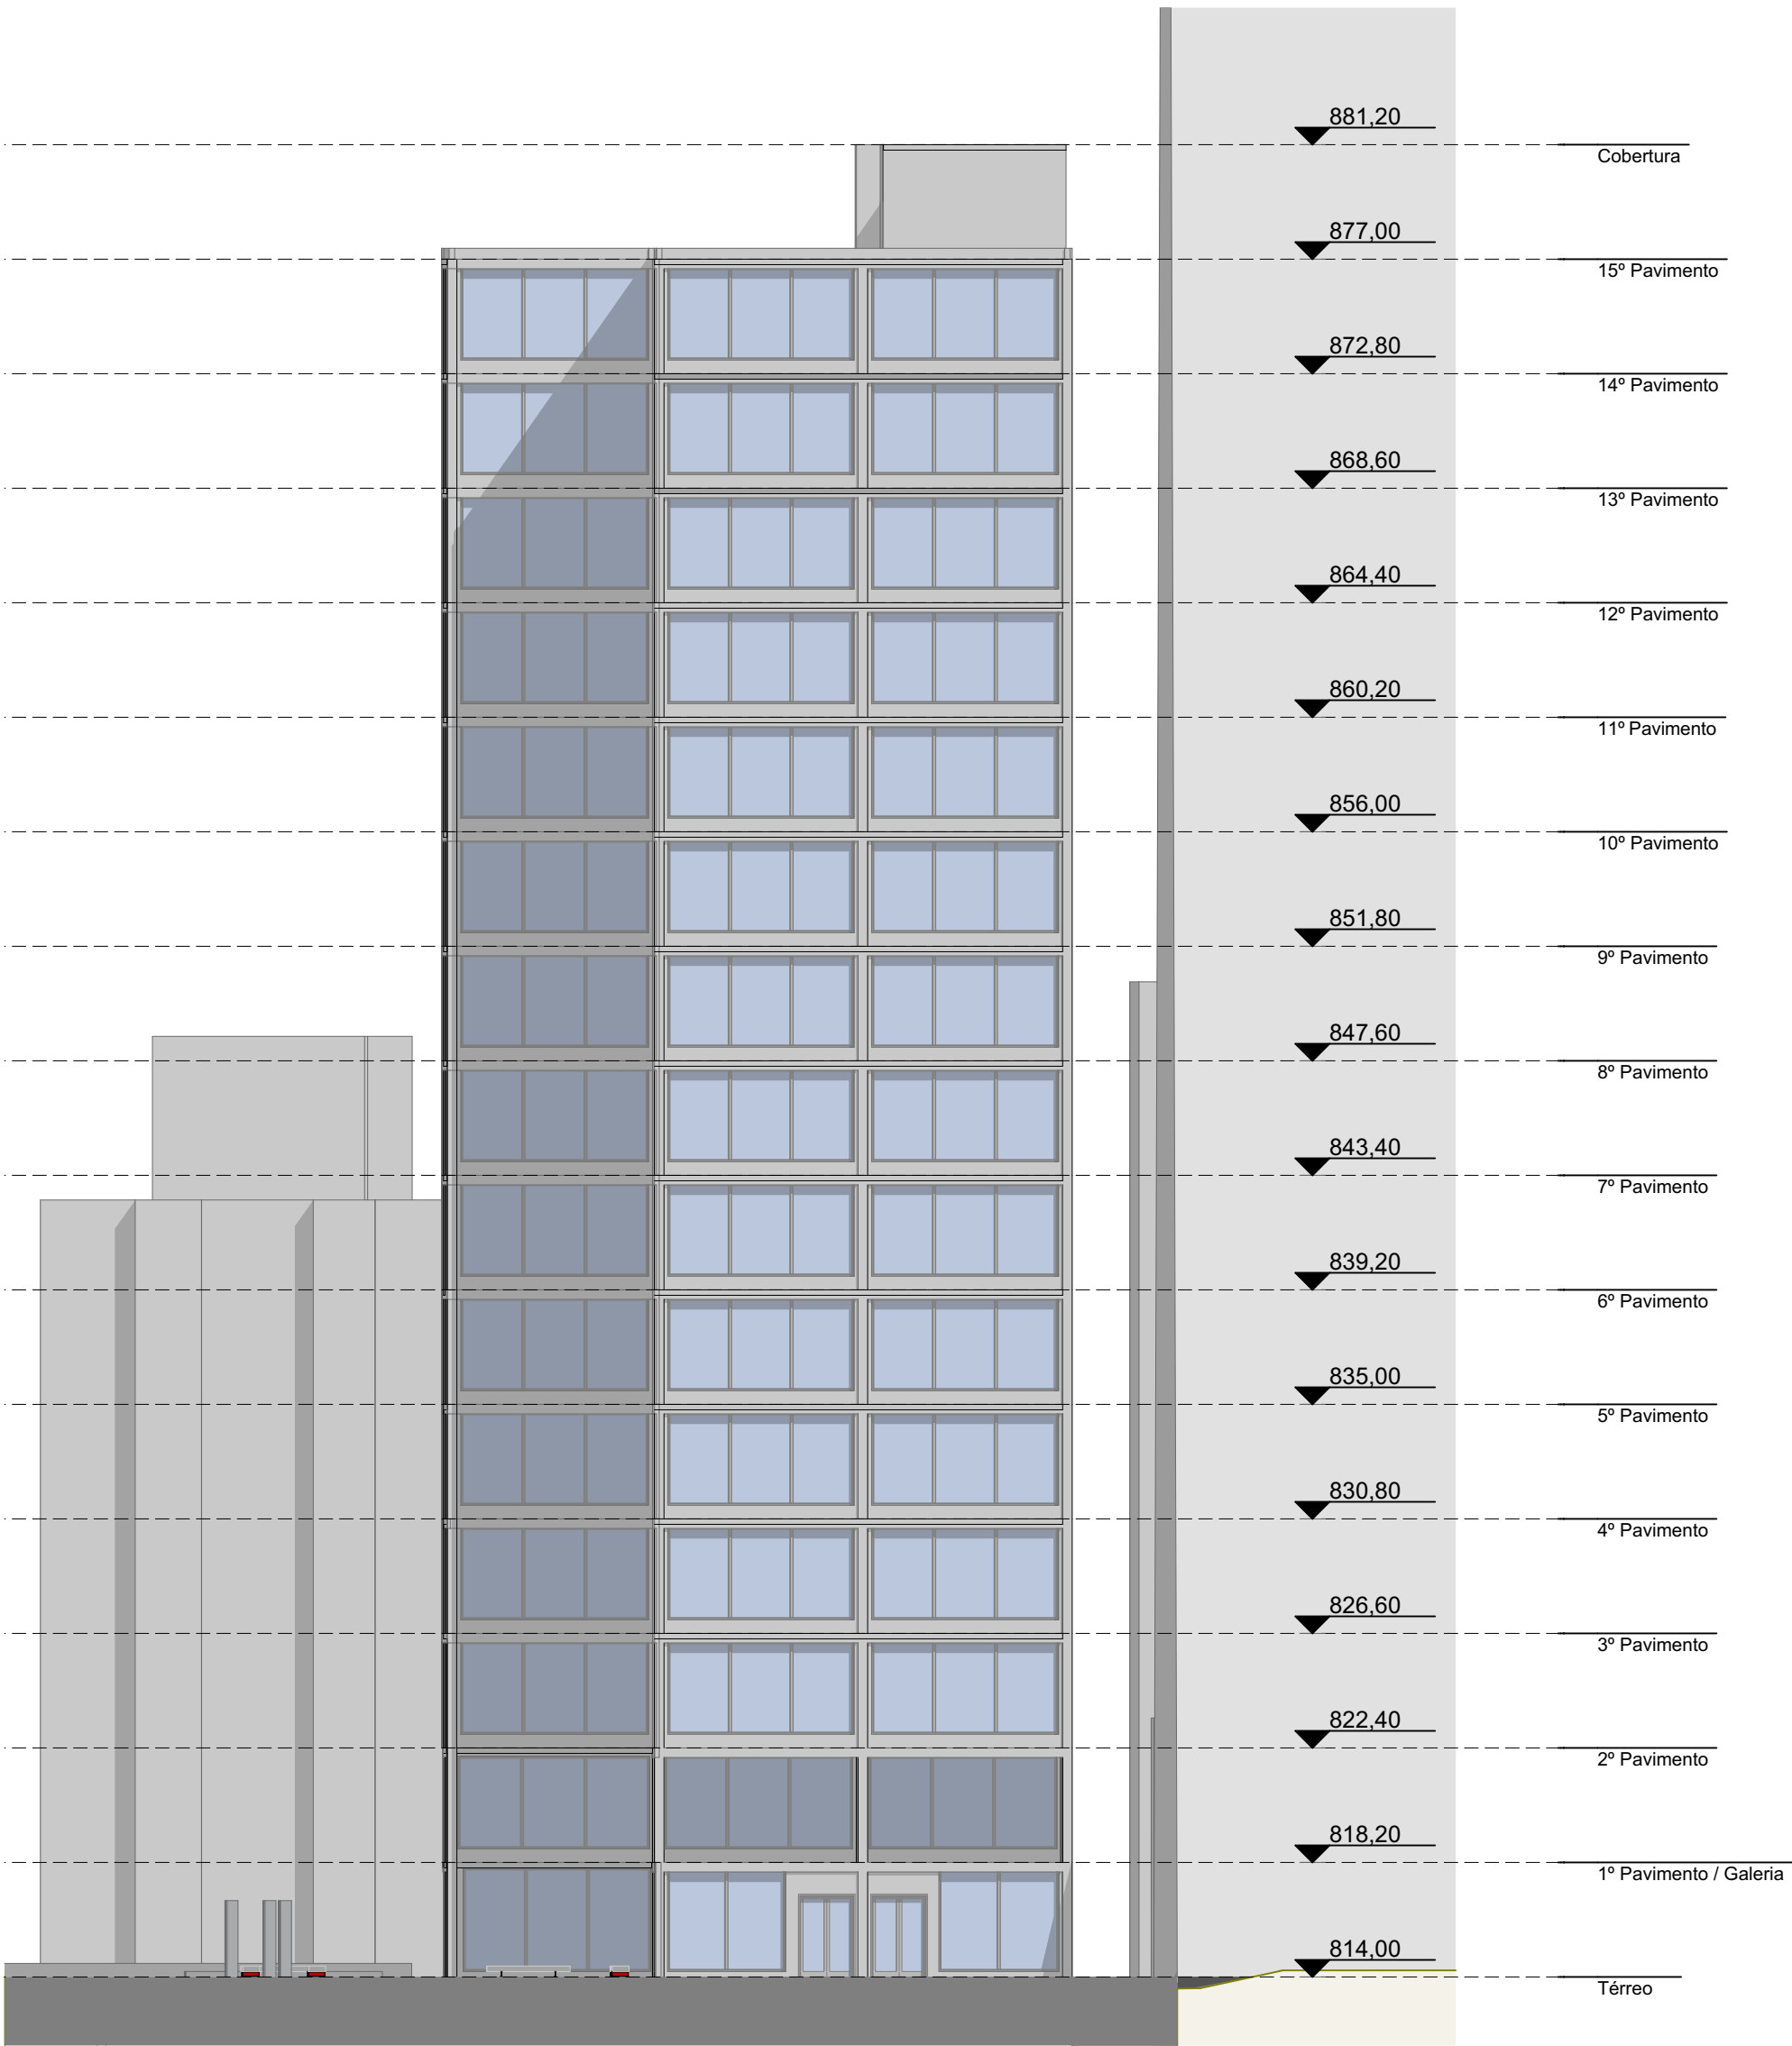

01 ELEVÇÃO FRETE 1:250

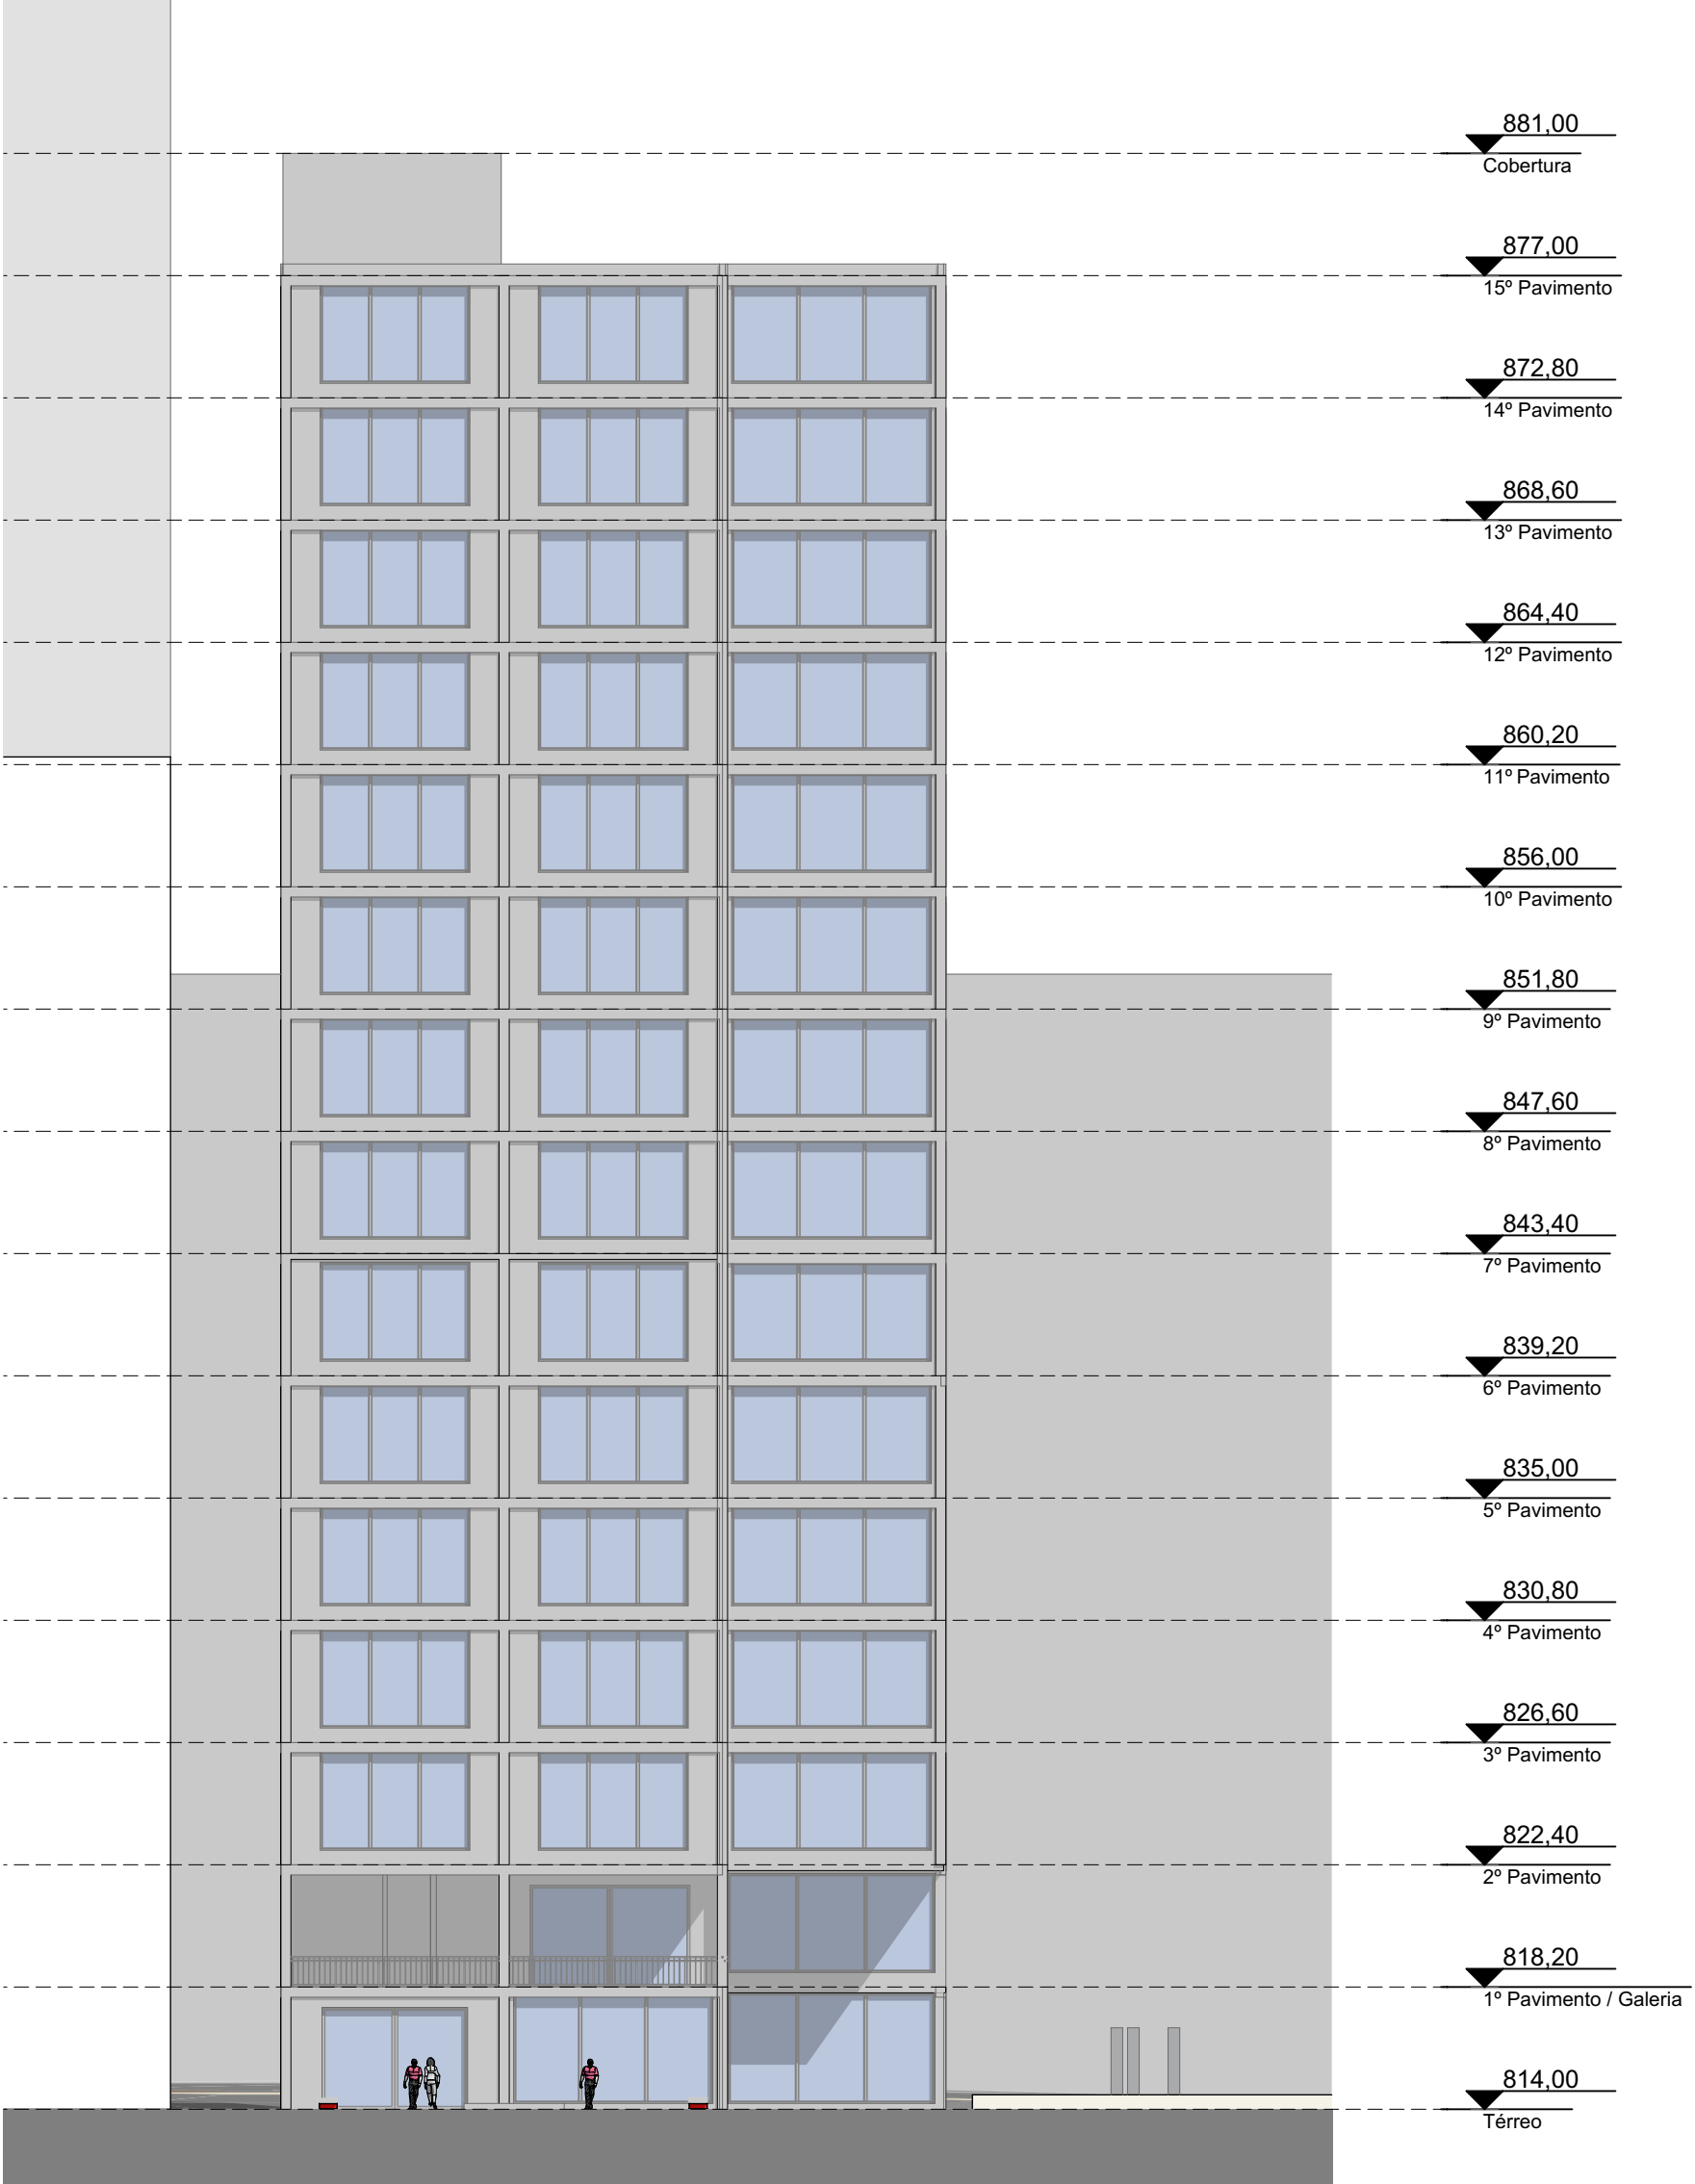

03 POSTERIOR 1:250



