
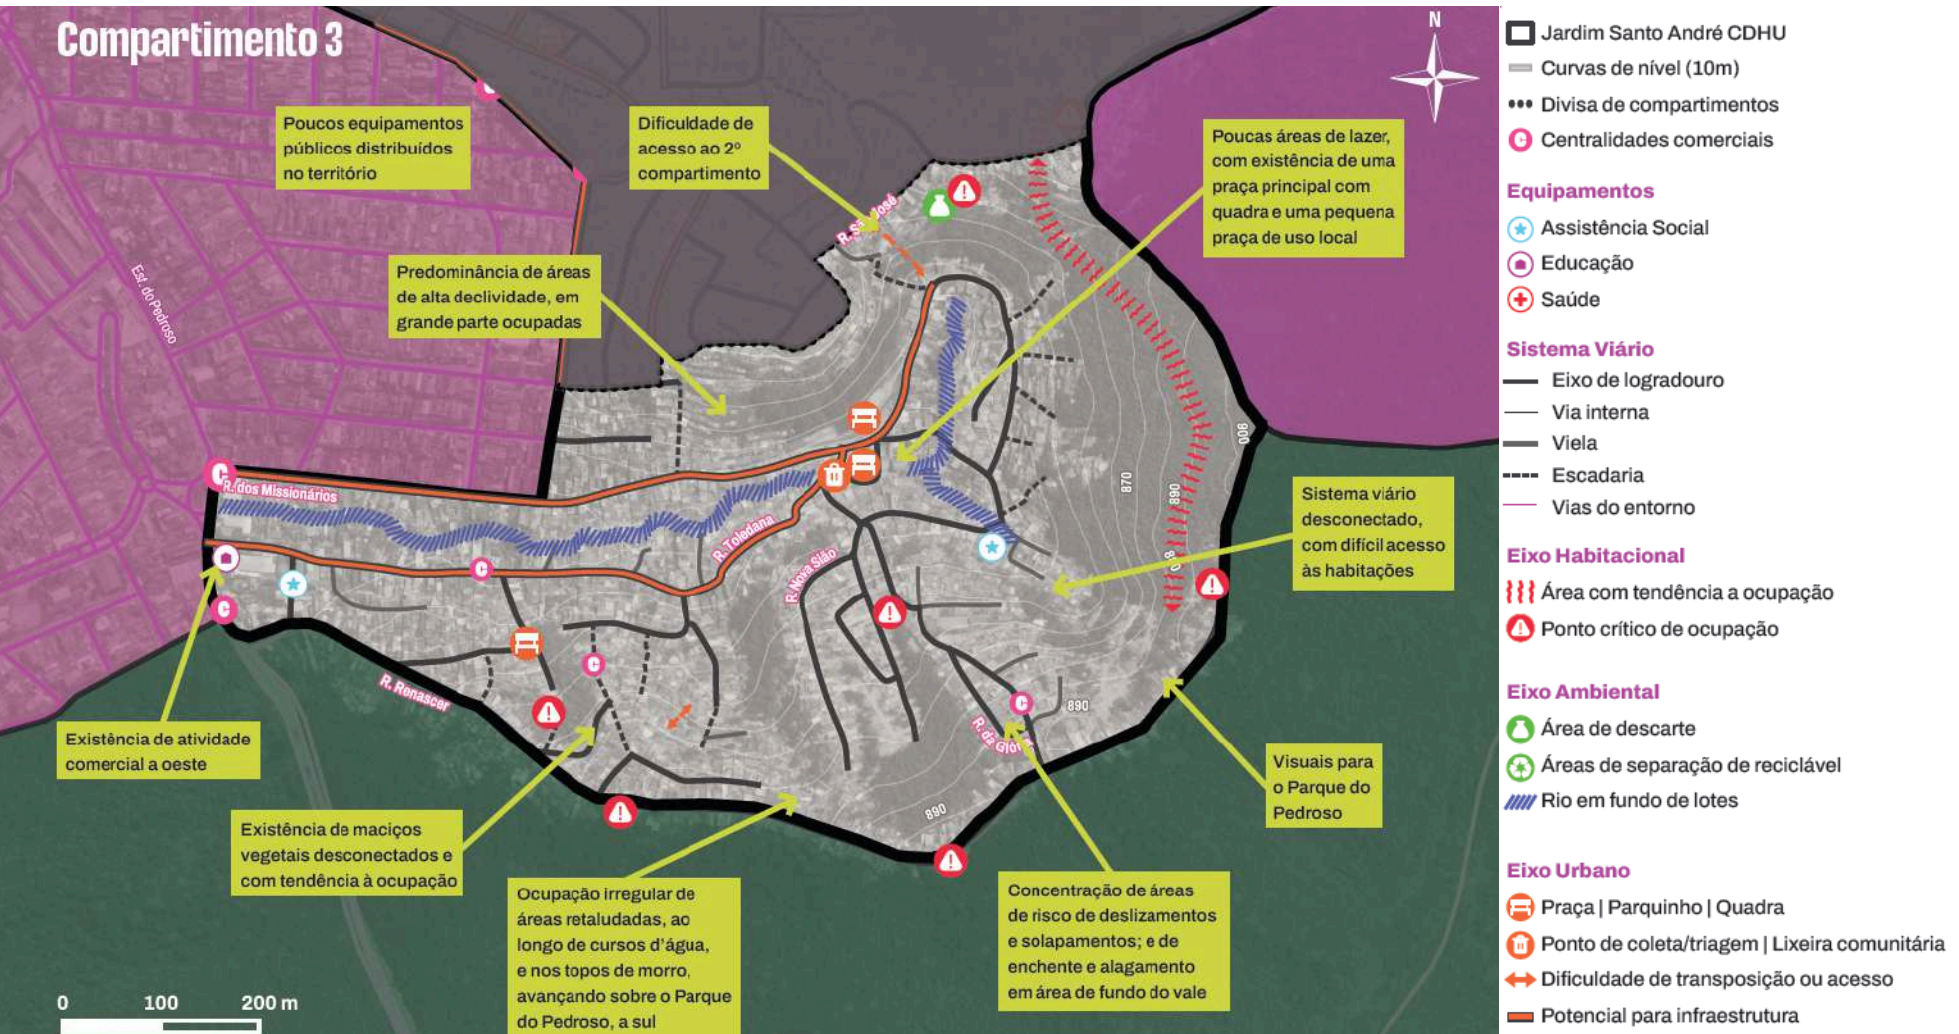


INTERVENÇÃO PREFEITURA:

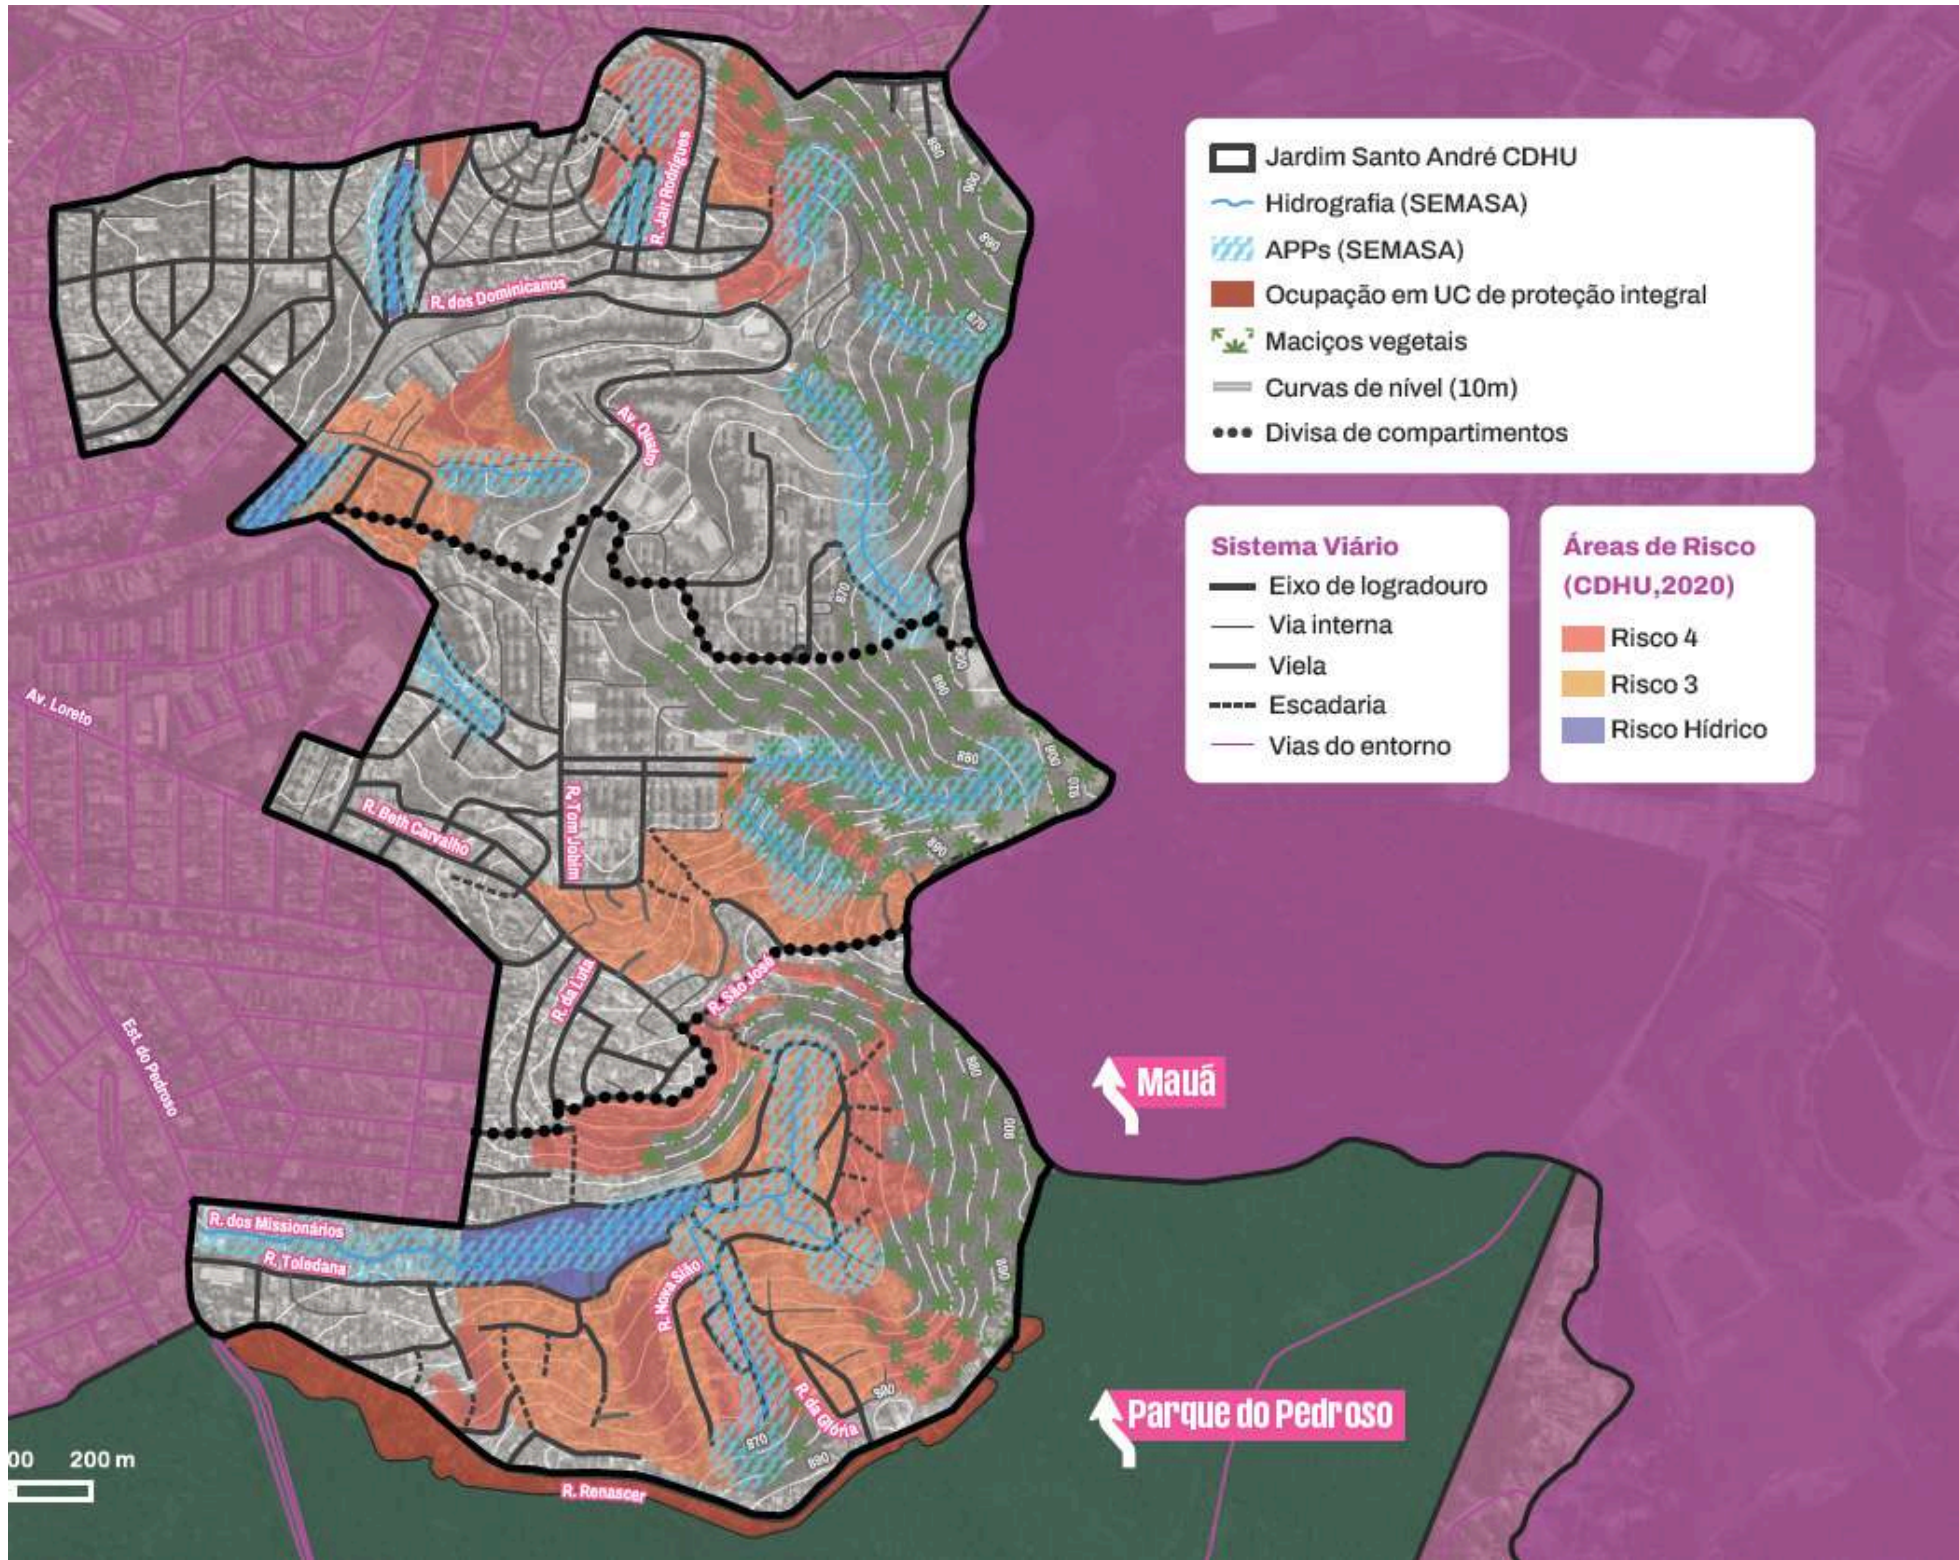

FONTE: Prefeitura Municipal Santo André

PROGRAMA DE NECESSIDADES|QUADRO DE ÁREAS:

Categoria	Áreas	Função/Descrição	Justificativa/ Objetivo Urbano
Habitação	HIS Uso público: 7.167m². Uso privado: 17.332,30m².	Conjunto de moradias destinadas à realocação das famílias em situação de vulnerabilidade.	Promover moradia digna, segura e acessível, reduzindo áreas de risco e fortalecendo o vínculo da população com o território.
	Centro esportivo Uso público: 6.424m².	Estrutura para práticas esportivas, lazer e convivência comunitária.	Incentivar atividades físicas, promover saúde e integração social.
Equipamentos Públicos (Educação, Cultura e Lazer)	Playground e áreas recreativas	Espços de lazer ao ar livre, voltados ao público infantil e familiar.	Proporcionar áreas seguras e acessíveis para recreação e convívio.
	Parque linear Uso público: 33.085m².	Área verde contínua com trilhas, vegetação nativa e equipamentos de lazer leve ao longo do córrego.	Valorizar o córrego como elemento paisagístico e ecológico, ampliando a conexão ambiental e adotar soluções de drenagem sustentável.
Áreas Verdes e Ambientais	Remoção de residências e implantação da agrofloresta Uso público: 58.980m².	Substituição de áreas de ocupação irregular por agrofloresta comunitária.	Requalificar o território, promover sustentabilidade e gerar oportunidades produtivas e educativas.
	Áreas de reflorestamento Uso público: 41.961m².	Espços destinados à recomposição vegetal e proteção do solo.	Recuperar áreas degradadas, melhorar o microclima e fortalecer a biodiversidade local.
	Áreas de preservação permanente (APP)	Faixa de proteção ao longo do córrego e encostas.	Garantir proteção ambiental e equilíbrio entre urbanização e natureza.
	Áreas de preservação permanente (APP)	Faixa de proteção ao longo do córrego e encostas.	Garantir proteção ambiental e equilíbrio entre urbanização e natureza.
Mobilidade e Acessos	Vias de circulação e acessos principais	Reestruturação e aplicação das vias locais e de conexão com o entorno.	Garantir acessibilidade, segurança viária e integração com a malha urbana existente.
	Ruas de pedestres e ciclovias	Caminhos de mobilidade ativa e sustentável.	Reduzir o uso de automóveis e incentivar deslocamentos não motorizados.
	Passarelas e pontes sobre o córrego	Conexões seguras entre as margens opostas.	Facilitar a circulação e promover continuidade urbana.
Infraestrutura e Serviços Urbanos	Sistema de drenagem sustentável	Implantação de soluções de escoamento e retenção de águas pluviais.	Minimizar riscos de enchentes e erosões, garantindo sustentabilidade ambiental.
	Redes de saneamento, energia e iluminação pública	Ampliação e qualificação das infraestruturas básicas urbanas.	Promover salubridade e segurança, integrando a área ao tecido urbano consolidado.

FONTE: Elaboração Autoral

Projeto de Intervenção Urbanística e Arquitetônica
Jardim Santo André

CONCEITO E PARTIDO:

Memorial Descritivo: Projeto de Intervenção Urbanística e Arquitetônica – Jardim Santo André CDHU. O Projeto de Intervenção Urbanística e Arquitetônica visa atuar na área localizada entre a Rua dos Missionários e a Rua Toledana, no bairro Jardim Santo André CDHU. O local é atualmente ocupado de forma irregular às margens de um córrego, por famílias em situação de vulnerabilidade. O principal objetivo é desenvolver uma proposta preliminar de Habitação de Interesse Social (HIS), garantindo moradia digna, segurança e integração urbana.

DIRETRIZES DO PROJETO:


As diretrizes do projeto enfatizam o respeito à Área de Preservação Permanente (APP) do córrego, promovendo uma faixa de proteção que possa ser reabilitada. O projeto busca conciliar a topografia natural, minimizando a necessidade de grandes cortes e aterros. Há uma forte valorização ambiental com a adoção de drenagem sustentável, paisagismo e criação de espaços de convivência.

A estrutura da intervenção é categorizada, incluindo Habitação, Equipamentos Públicos (Educação, Cultura e Lazer), Áreas Verdes/Ambientais, Mobilidade e Acessos e Infraestrutura e Serviços Urbanos.

ELEMENTOS DA INTERVENÇÃO:

- Equipamentos Públicos Comunitários – Visando o Fortalecimento Comunitário e a Integração Social: Edifício Esportivo (Uso Público): Com uma área de 6.424 m² de Uso público. Sua finalidade é incentivar atividades físicas e promover saúde e integração social. Playground e Áreas Recreativas: São espaços de lazer ao ar livre, voltados ao público infantil e familiar. O objetivo é proporcionar áreas seguras e acessíveis para recreação e convívio.

DIAGRAMA DE REMOÇÃO:

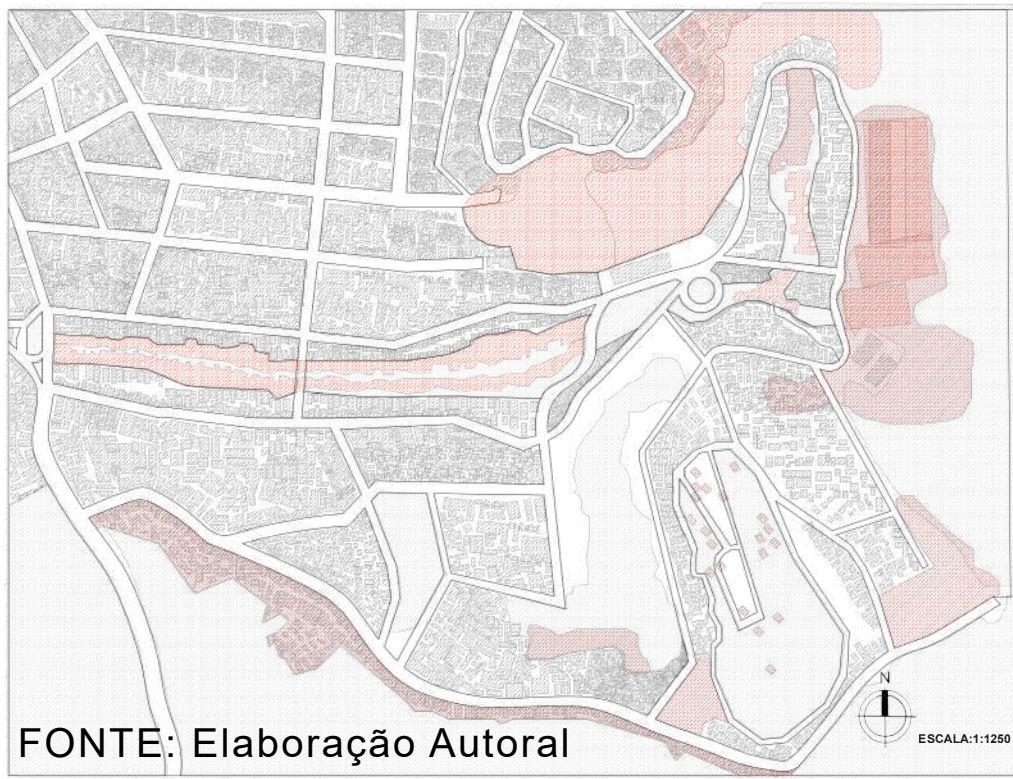

FONTE: Elaboração Autoral

2. Habitação de Interesse Social (HIS):

As unidades habitacionais são destinadas à realocação das famílias em situação de vulnerabilidade, promovendo moradia digna, segura e acessível, e reduzindo áreas de risco. O local tem a previsão de remoção de 2.576 famílias. As moradias são implementadas através de edifícios, acompanhando a topografia. A área de Habitação de Interesse Social (HIS) prevista é de 7.167 m² para Uso público e 17.332,30 m² para Uso privado.

LEGENDA:

● ÁREAS DE REMOÇÃO

DIAGRAMA DE AREAS VERDES:

3. Áreas Verdes e Ambientais:

A requalificação ambiental é um pilar central do projeto, com a adoção de soluções de drenagem sustentável:

- Parque Linear (Uso Público): Com 33.085 m², consiste em uma área verde contínua com trilhas, vegetação nativa e equipamentos de lazer leve. Seu objetivo é valorizar o córrego como elemento paisagístico e ecológico, além de ampliar a conexão ambiental.
- Agro floresta (Uso Público): Esta intervenção, com 58.980,00 m², consiste na substituição de áreas de ocupação irregular por um sistema agroflorestal comunitário. O objetivo é requalificar o território, promover sustentabilidade e gerar oportunidades produtivas e educativas.
- Áreas de Reflorestamento (Uso Público): Com 41.961 m², são espaços destinados à recomposição vegetal e proteção do solo. O intuito é recuperar áreas degradadas, melhorar o microclima e fortalecer a biodiversidade local.



FONTE: Elaboração Autoral

LEGENDA:

● ÁREA DE REFORESTAMENTO
● ÁREA VERDE JÁ EXISTENTE
● ÁREAS VERDES PROPOSTAS


DIAGRAMA DE INSOLAÇÃO E VENTILAÇÃO:



FONTE: Elaboração Autoral

O diagrama indica a direção dos ventos predominantes e a incidência solar ao longo do dia. Essas informações orientam o posicionamento das novas edificações e áreas verdes, garantindo melhor conforto térmico e ventilação natural na área.

DIAGRAMA DE USO DO SOLO E MOBILIDADE:

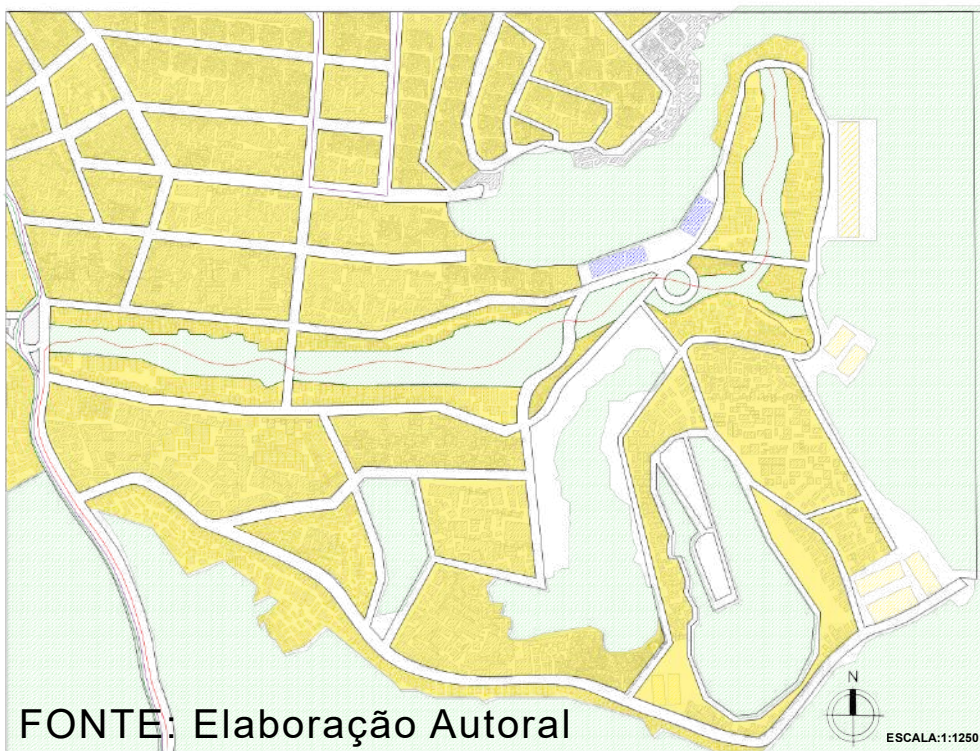

FONTE: Elaboração Autoral

LEGENDA:

● USO RESIDENCIAL
● USO SOCIAL E INSTITUCIONAL
● CICLOVIA PROPOSTA
● LINHA DE ONIBUS MUNICIPAL
● LINHA DE ONIBUS INTERMUNICIPAL


4. Mobilidade e Infraestrutura:

O projeto promove a reestruturação da malha urbana para garantir acessibilidade e segurança viária:

- Vias de Circulação e Acessos principais: Reestruturação e ampliação das vias locais e de conexão, garantindo acessibilidade, segurança viária e integração com a malha urbana existente.
- Ruas de pedestres e ciclovias: Promovem a mobilidade ativa e sustentável. O objetivo é reduzir o uso de automóveis e incentivar deslocamentos não motorizados.
- Passarelas e pontes sobre o córrego: Garantem conexões seguras entre as margens opostas, facilitando a circulação e promovendo continuidade urbana.
- Infraestrutura Urbana:


Ampliação e qualificação das redes de infraestrutura básica, incluindo sistemas de drenagem sustentável (para minimizar enchentes e erosões), água, esgoto, energia e iluminação pública para promover salubridade e segurança, integrando a área ao tecido urbano consolidado.

A proposta de intervenção no Jardim Santo André CDHU se estrutura como um processo de urbanização inclusiva e sustentável, conciliando habitação de qualidade, mobilidade urbana e valorização ambiental, promovendo a permanência qualificada da população em seu território.

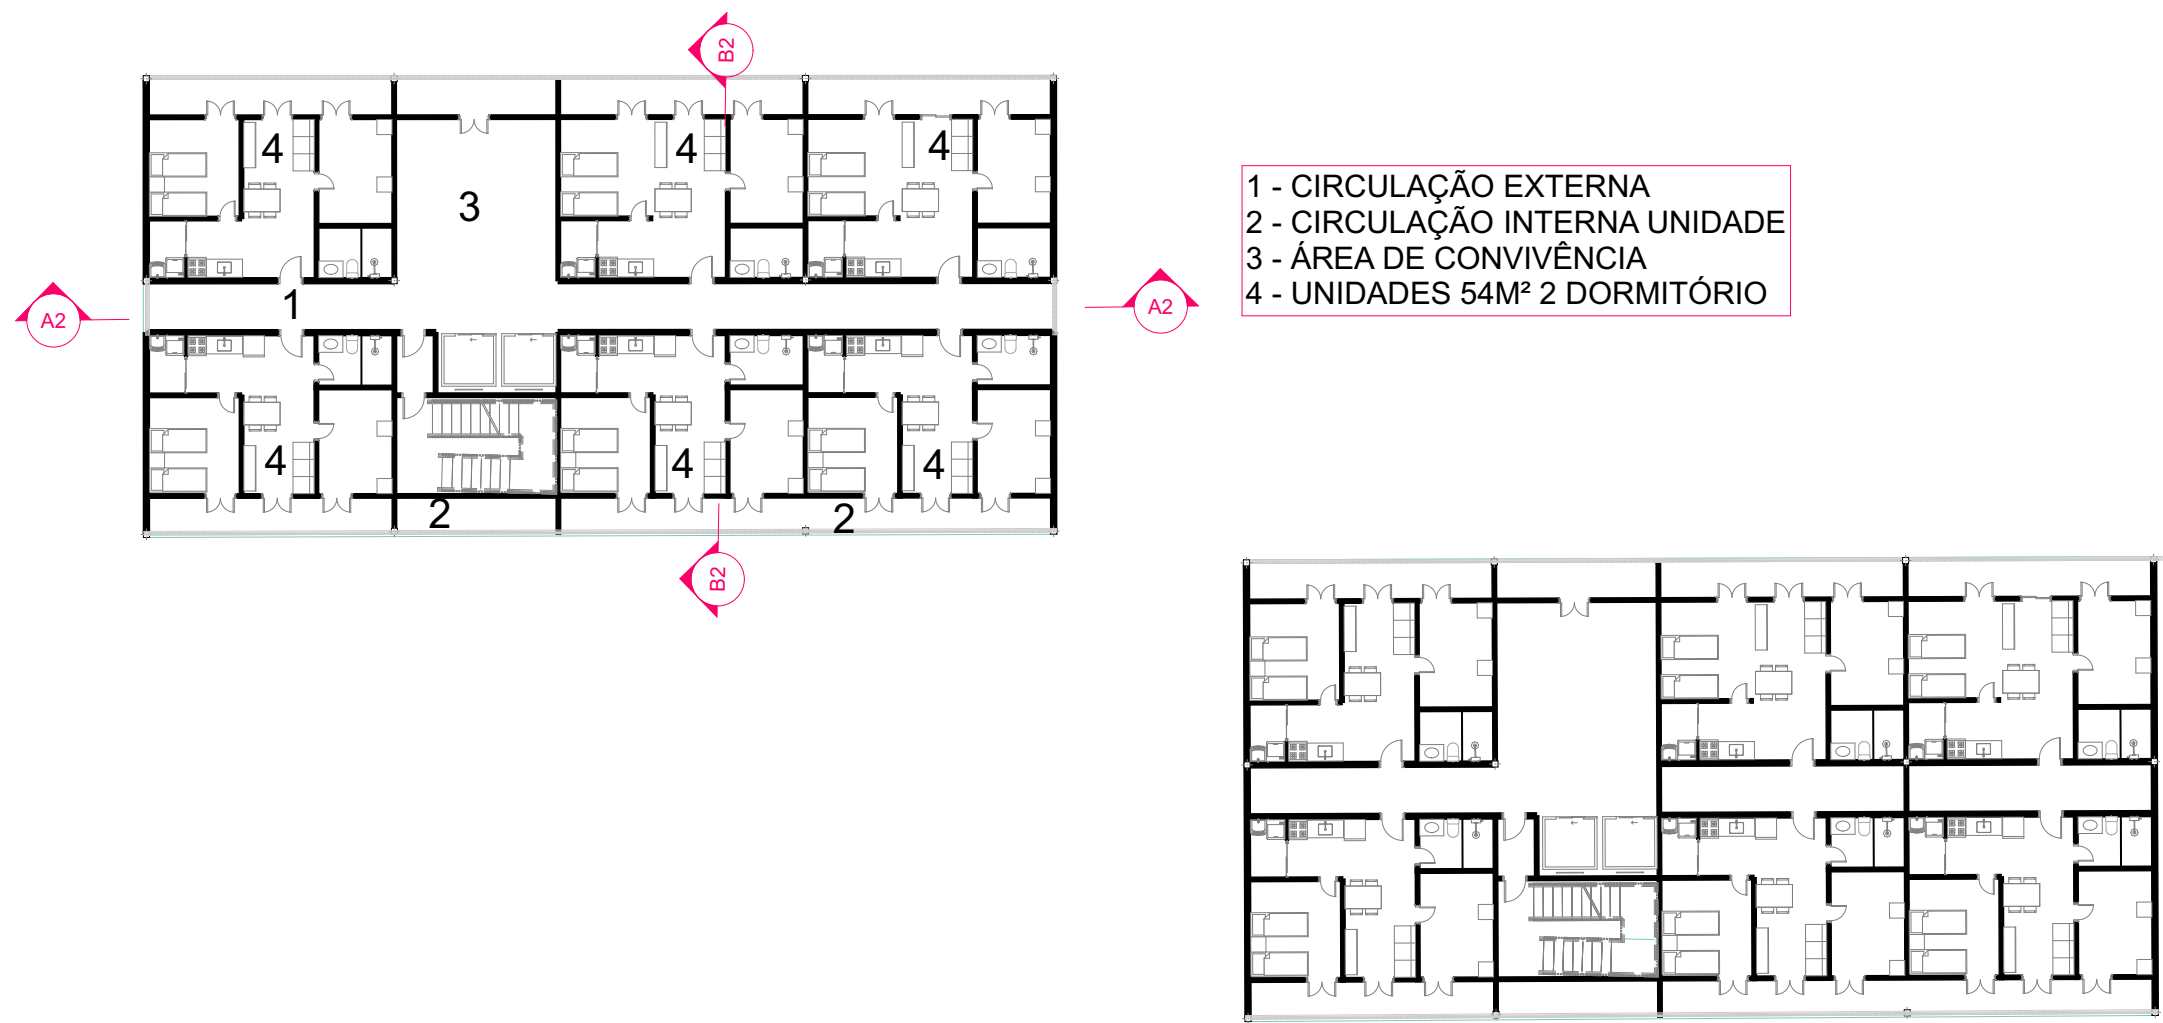

PAVIMENTO TIPO

1:250

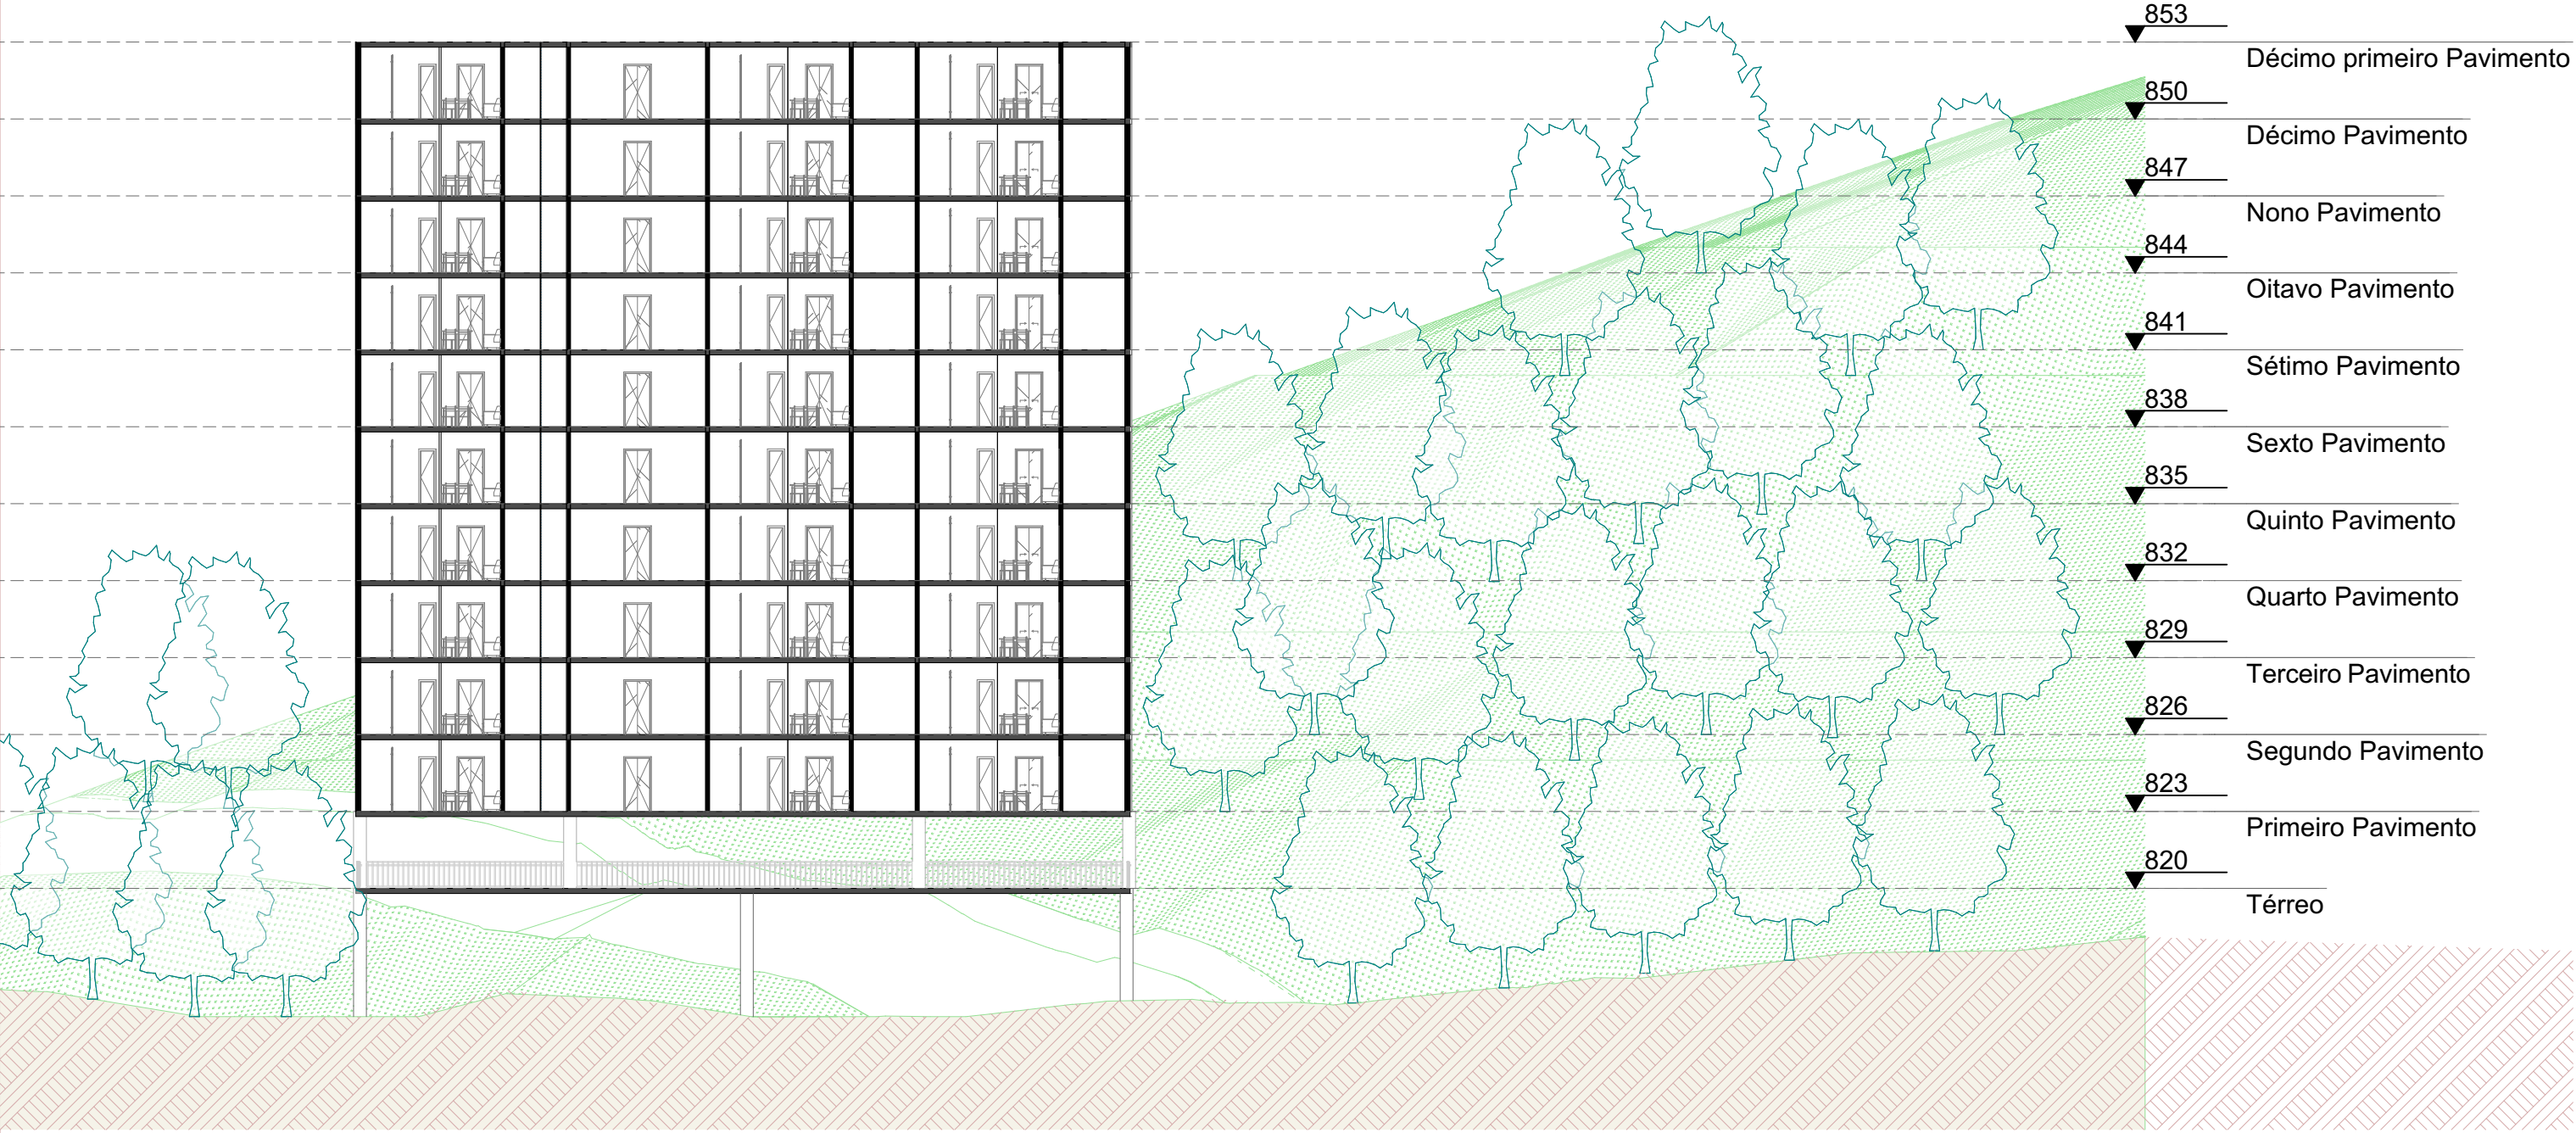

CORTE A1

1:250




PERSPECTIVA 1

1:400



PERSPECTIVA 2

1:600

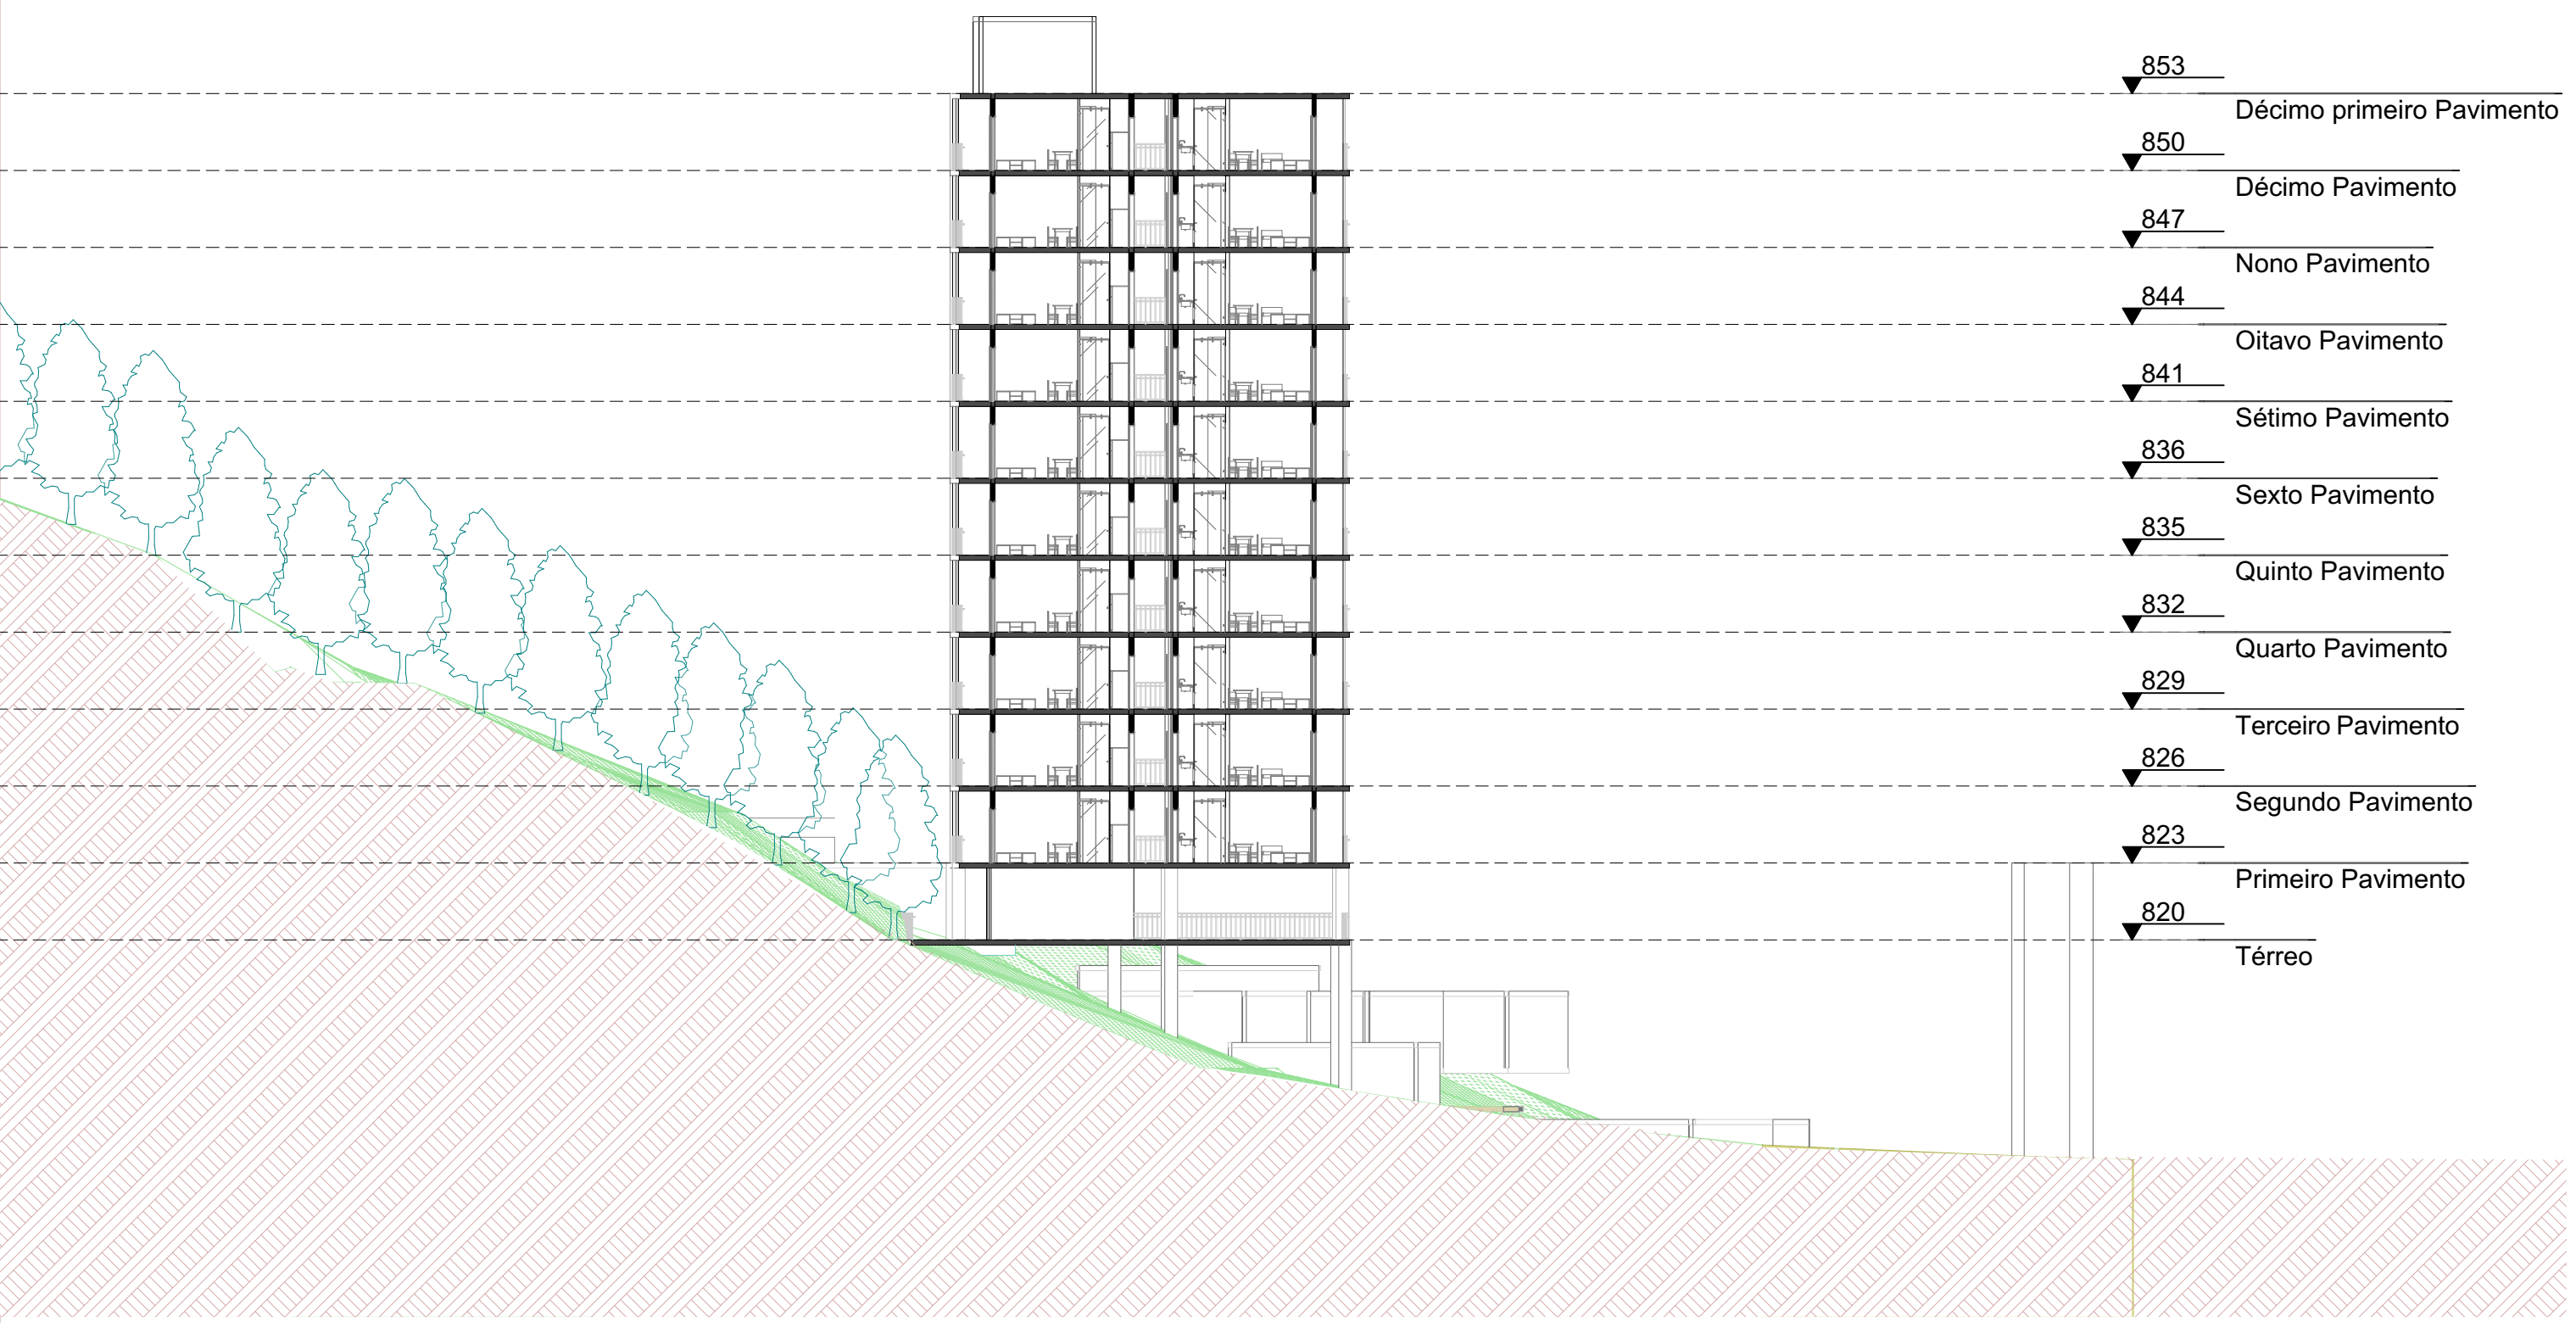

CORTE B2

1:250

MEMORIAL DESCRITIVO

O Conceito central na construção de Habitação de Interesse Social no **Jardim Santa André** CDHU é o desenvolvimento de moradia qualificadas. Este conceito foca na transformação de áreas de ocupação irregular e risco em assentamentos urbanos seguros e integrados.

A habitação é um dos pilares da intervenção, cujo objetivo é a realocação das famílias em situação de vulnerabilidade que atualmente ocupam áreas de risco. O conceito não é simplesmente fornecer um abrigo, buscamos promover moradia digna, segura e acessível, garantindo a redução das áreas de risco e a integração ao tecido urbano consolidado.

1. Partido Arquitetônico

O Partido Arquitetônico estabelecido para as unidades habitacionais está diretamente vinculado à topografia do terreno e à necessidade de oferecer unidades eficientes e confortáveis, garantindo segurança das famílias realocadas. O projeto contempla a construção de **120 unidades habitacionais**.

- **Implantação:** As moradias são implementadas através de edifícios multifamiliares, cuja disposição acompanha a topografia natural do local, minimizando a necessidade de grandes intervenções de corte e aterro.
- **Verticalização:** Cada pavimento dos edifícios foi planejado para abrigar 6 unidades habitacionais por andar.

2. Tipologia e Conforto Familiar


A tipologia das unidades foi pensada para maximizar o conforto e a funcionalidade, atendendo ao propósito social do projeto.

- **Área por Unidade:** Cada unidade habitacional possui uma área privativa de **54,45 m²**.
- **Objetivo de Ocupação:** O dimensionamento das unidades, com 54,45 m², tem como intuito primordial apresentar moradias que atendam de uma forma confortável uma família de 4 pessoas, promovendo bem-estar e qualidade de vida.

3. Integração e Sustentabilidade (Contexto do HIS)

Embora o foco seja na habitação, o Partido Arquitetônico se insere em um contexto mais amplo de qualificação urbana e ambiental. As edificações são concebidas em um entorno que prioriza a valorização ambiental e o respeito à Área de Preservação Permanente (APP) do córrego.


A infraestrutura básica associada à entrega das unidades (HIS) inclui a qualificação das redes de saneamento, energia e iluminação pública, essenciais para promover a salubridade e segurança da nova vizinhança, integrando-a ao tecido urbano consolidado. O projeto busca conciliar a provisão de habitação de qualidade com um processo de urbanização inclusiva e sustentável.

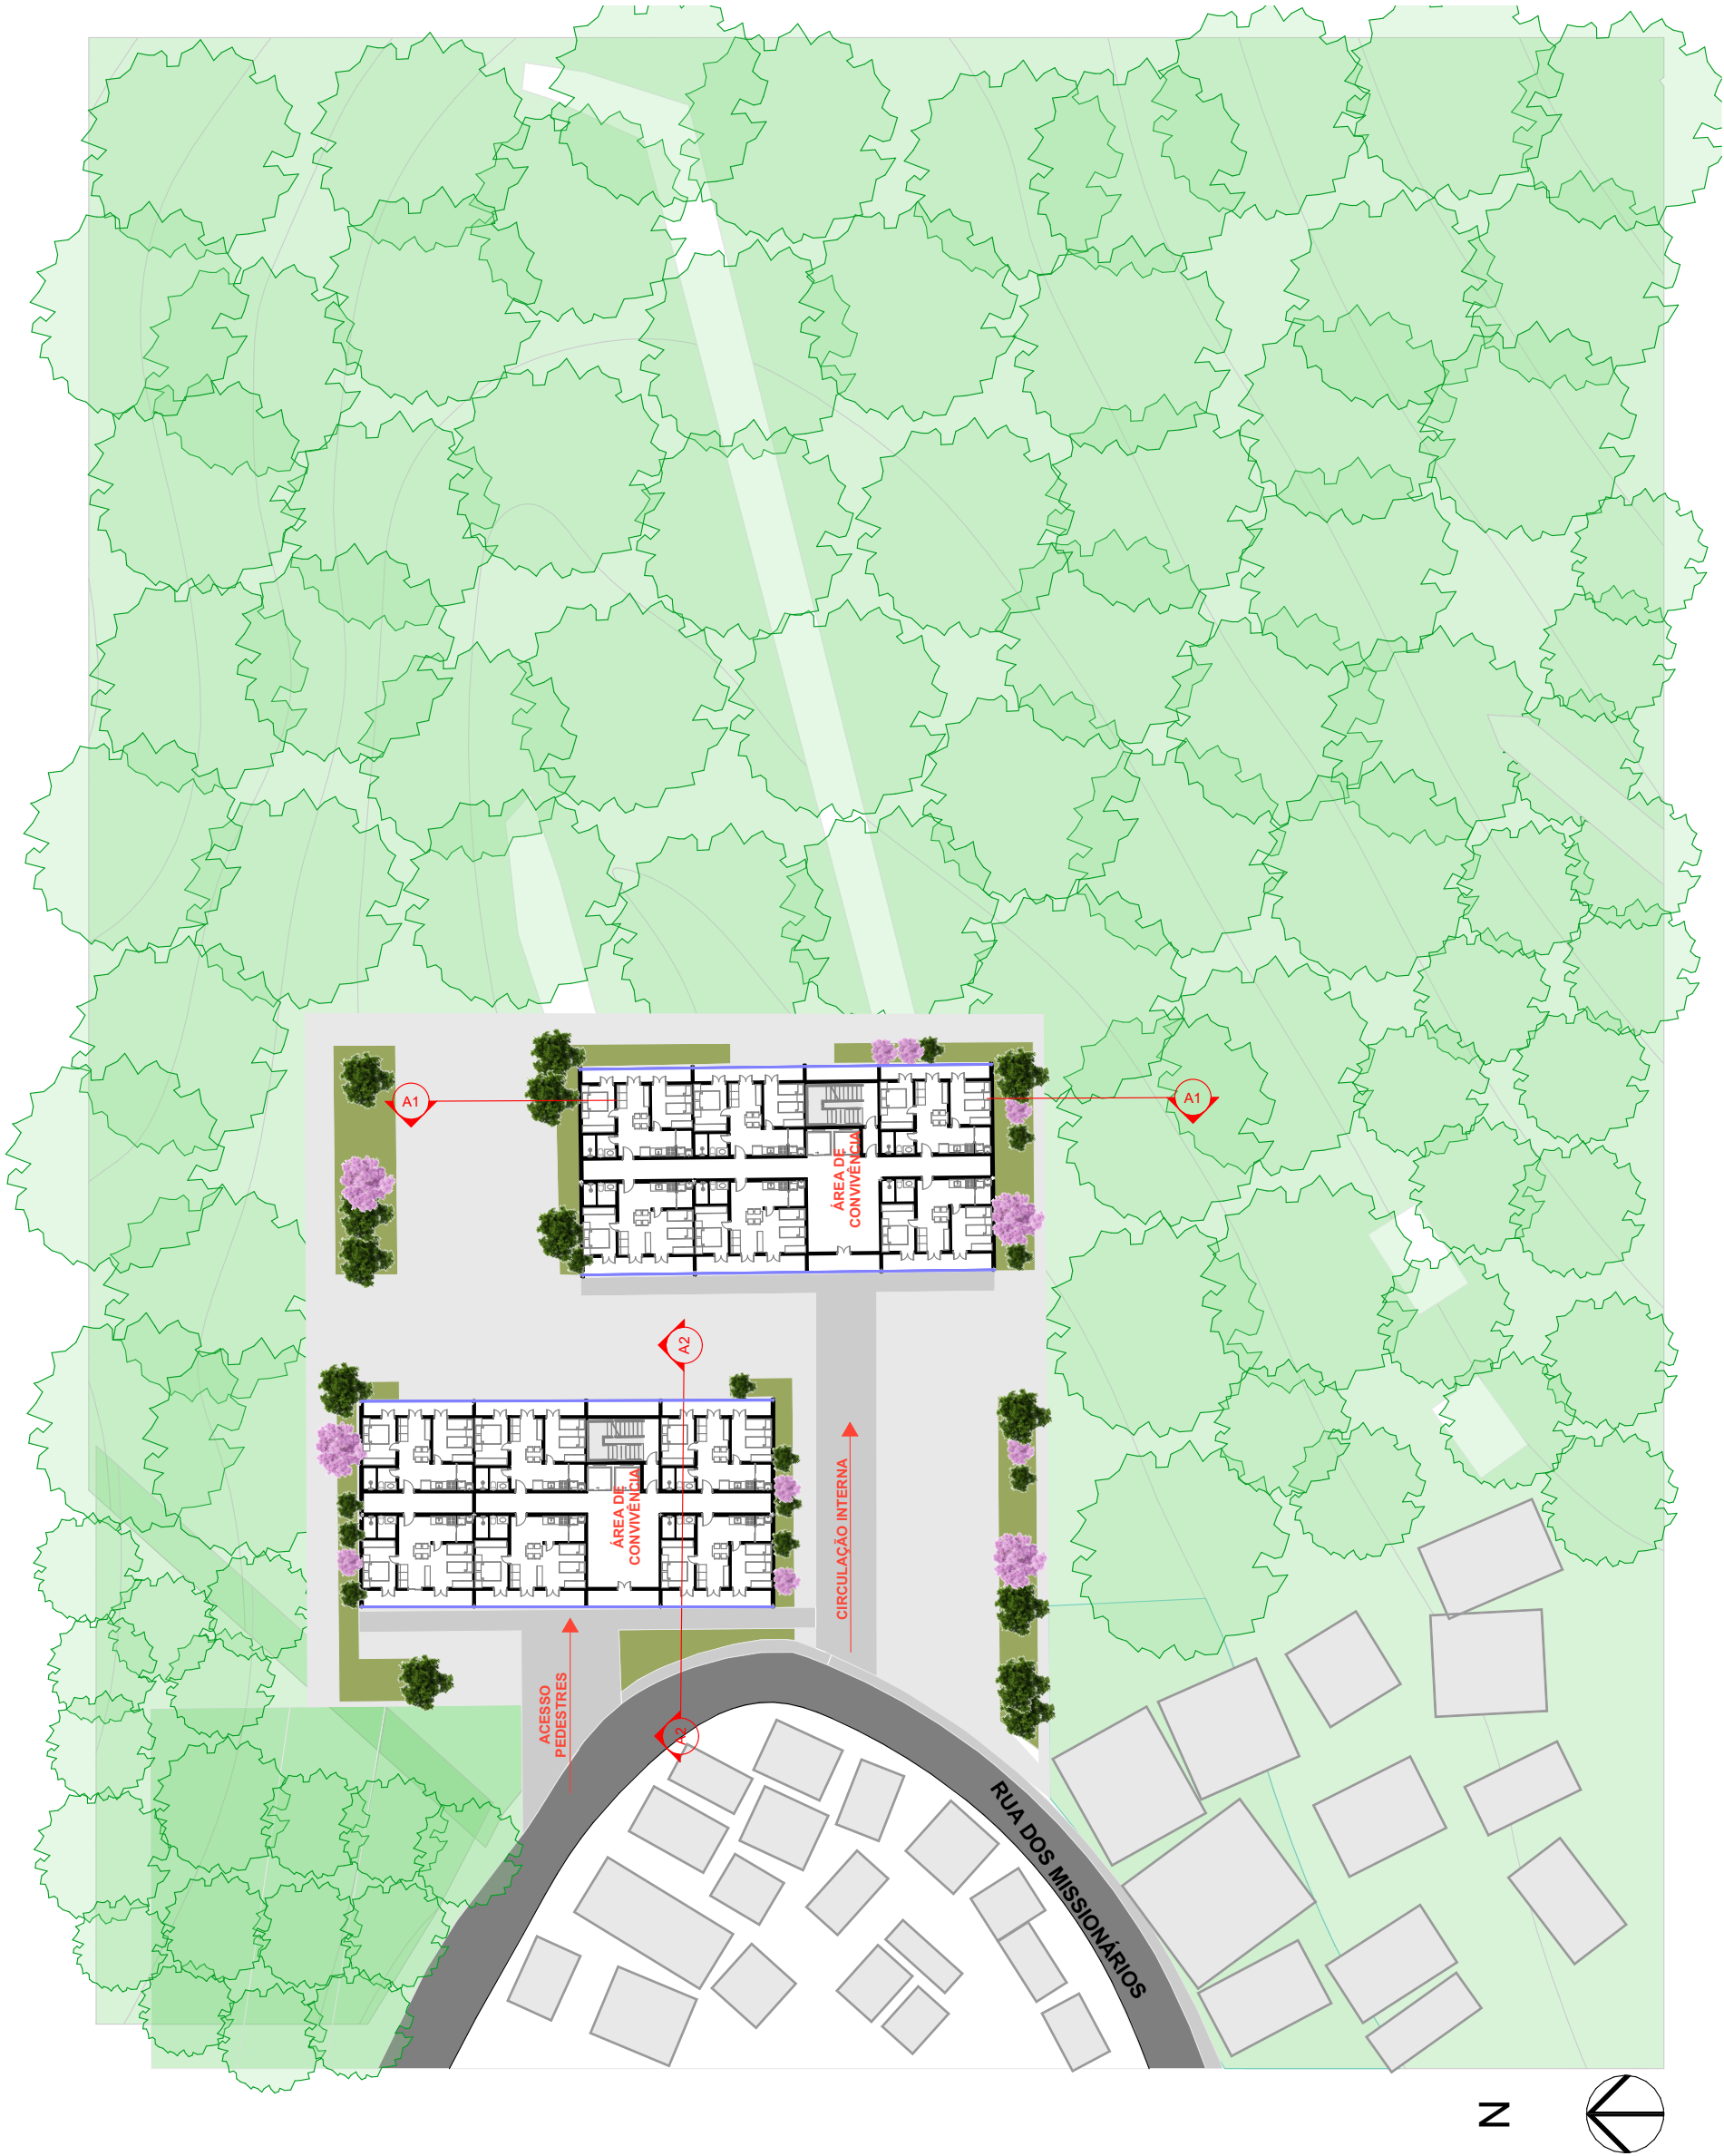


01 IMPLANTAÇÃO 1:500



02 CORTE A1 1:500

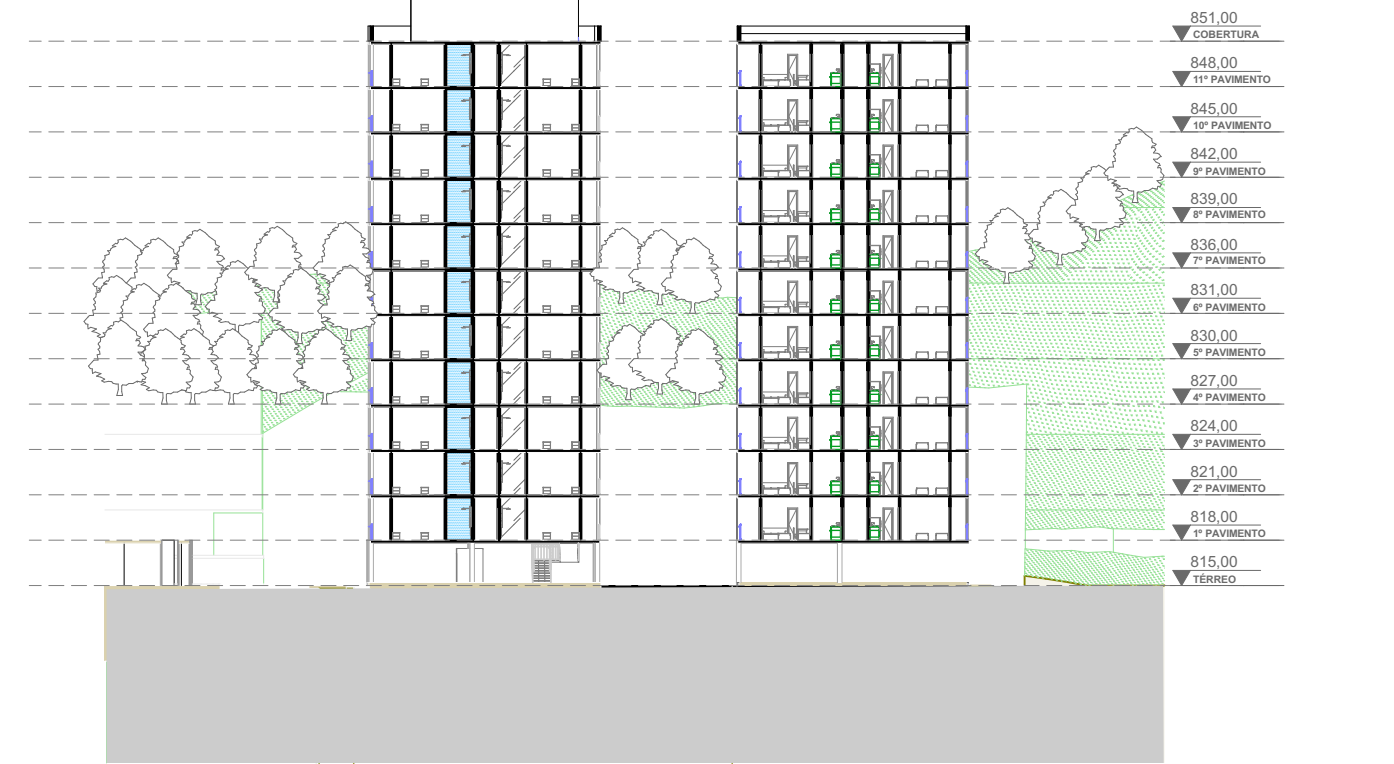

03 CORTE A2 1:500

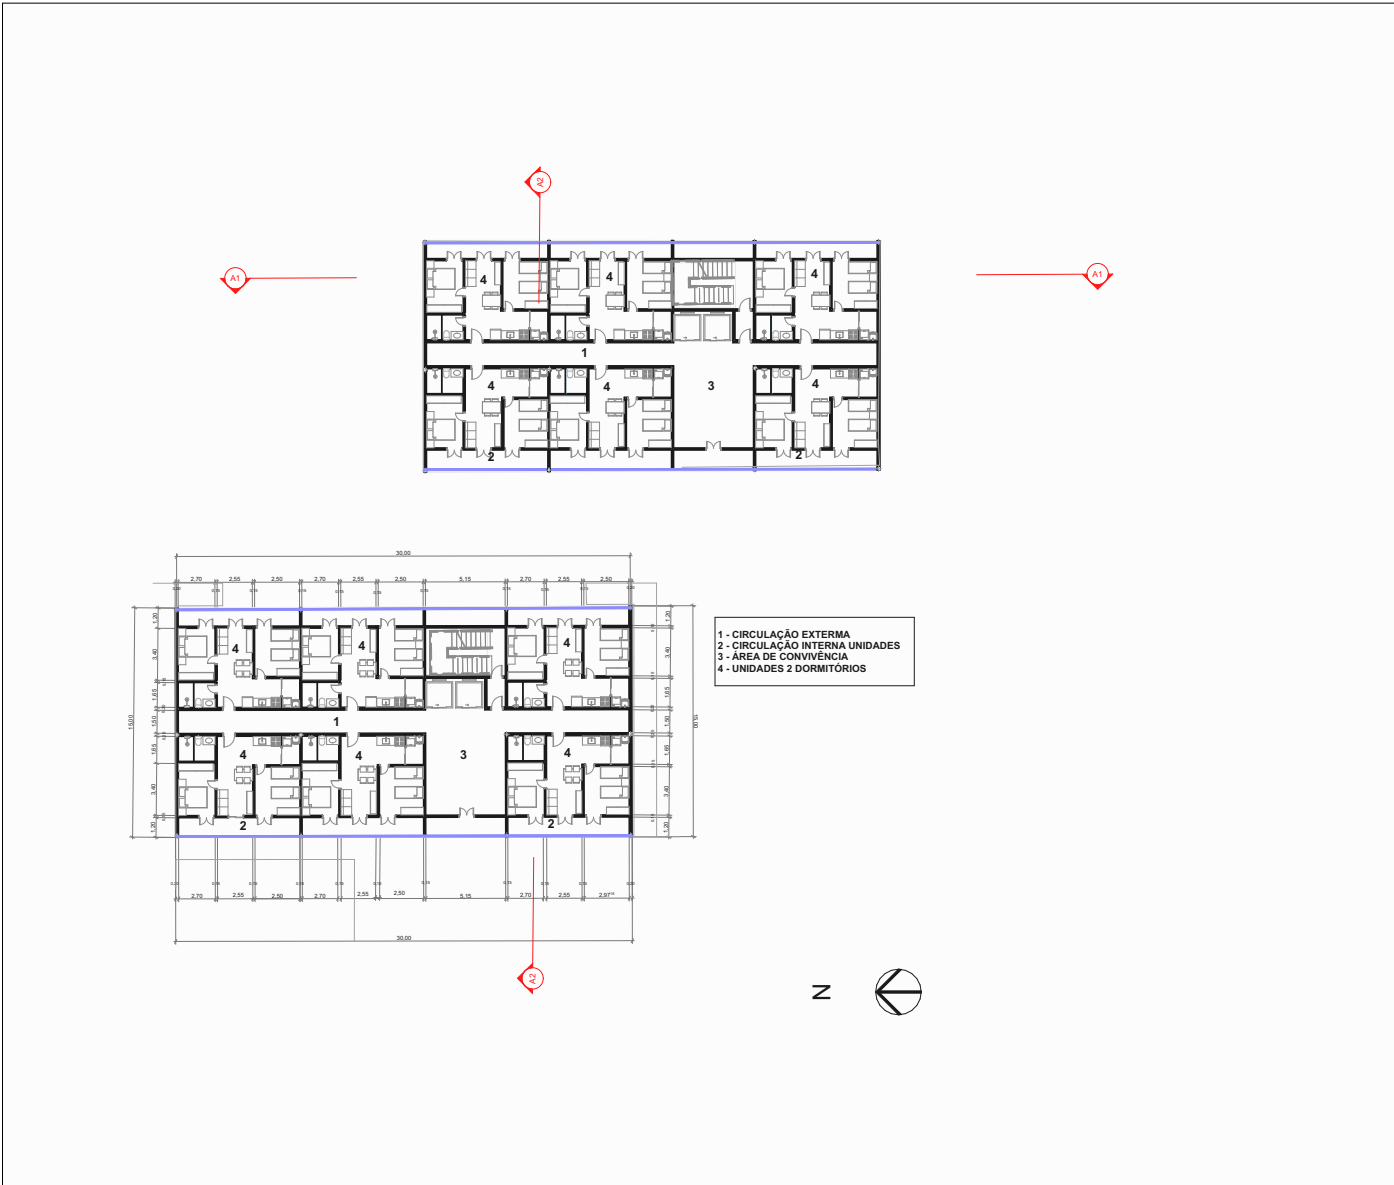

04 PAVIMENTO TIPO 1:500



05 MAPA DE LOCALIZAÇÃO 1:500



06 PERSPECTIVA 1 1:1000

07 PERSPECTIVA 2 1:1000

